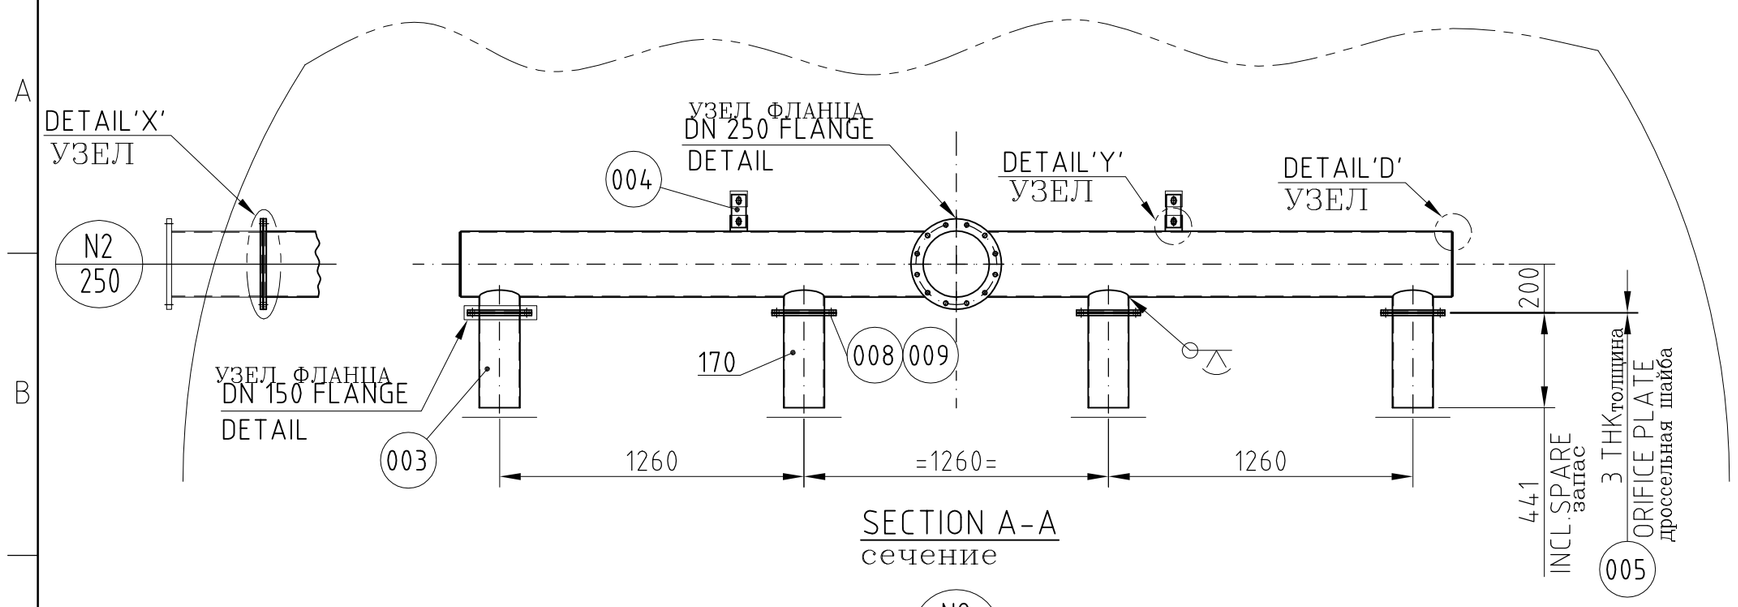

SECTION A-A
сечение

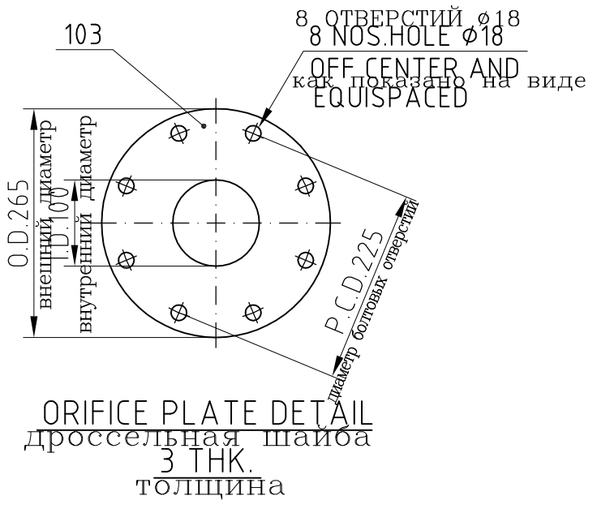

ORIFICE PLATE DETAIL
дроссельная шайба
3 THK.
толщина

item list

item	qty.	spare	unit	drawing- or part-no.	description	remarks	material	масса [kg] wght. [kg]
000	1	-	PC	2139334-001-007	LTT Liq. Inlet T-shape -ID 6400mm труба ввода		1.4307/304L	288
001	56	-	PC	300000027	Arm channel with baffle канал с отражателем			
002	1	-	PC	300000210	Pipe with flange труба с фланцем & Lug			
003	4	-	PC	300000210	Pipe with flange труба с фланцем			
004	2	-	PC	300000029	Suspension подвеска			
005	4	-	PC	300000047	Orifice plate дроссельная шайба			
008	76	8	PC	10006646	Hex bolt DIN933 M16x60 болт		A-193Gr.B8	0.114
009	76	8	PC	10006683	Hex nut DIN934 M16 гайка		A-194Gr.8	0.033
010	8	2	PC	10002714	Washer 17/32x3 шайба		1.4307/304L	0.014
011	2	-	PC	10002899	Flange DN250x12 фланец		1.4307/304L	4.5
103	7.5	-	KG	10004456	Sheet 3x1500x3000 лист		1.4307/304L	-
105	3	-	KG	10004455	Sheet 6x1500x3000 лист		1.4307/304L	-
107	8	-	PC	10002901	Flange DN150x10 фланец		1.4307/304L	2.4
108	2	-	PC	10002899	Flange DN250x12 фланец		1.4307/304L	4.5
170	22	-	M	10005222	Pipe welded 6"x10S приварная труба		1.4307/304L	14
171	7	-	M	10005224	Pipe welded 10"x10S приварная труба		1.4307/304L	28

001 - 099: parts / 100 - 199: materials 001-099: детали / 100-199: материалы

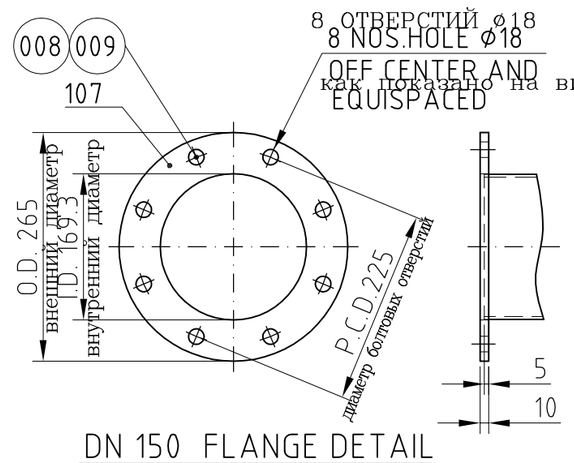

DN 150 FLANGE DETAIL
УЗЕЛ ФЛАНЦА

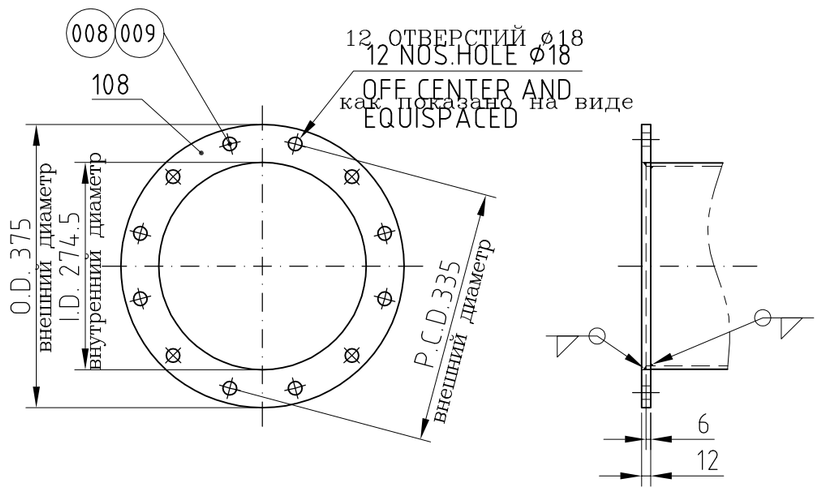

DN 250 FLANGE DETAIL
УЗЕЛ ФЛАНЦА

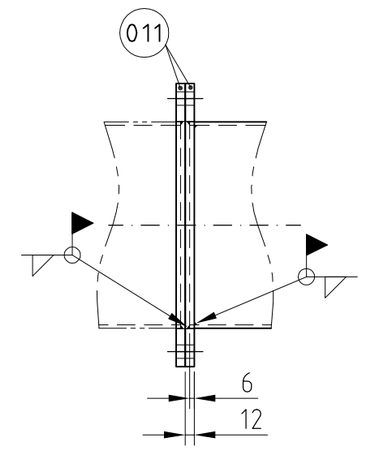

DETAIL 'X'
УЗЕЛ

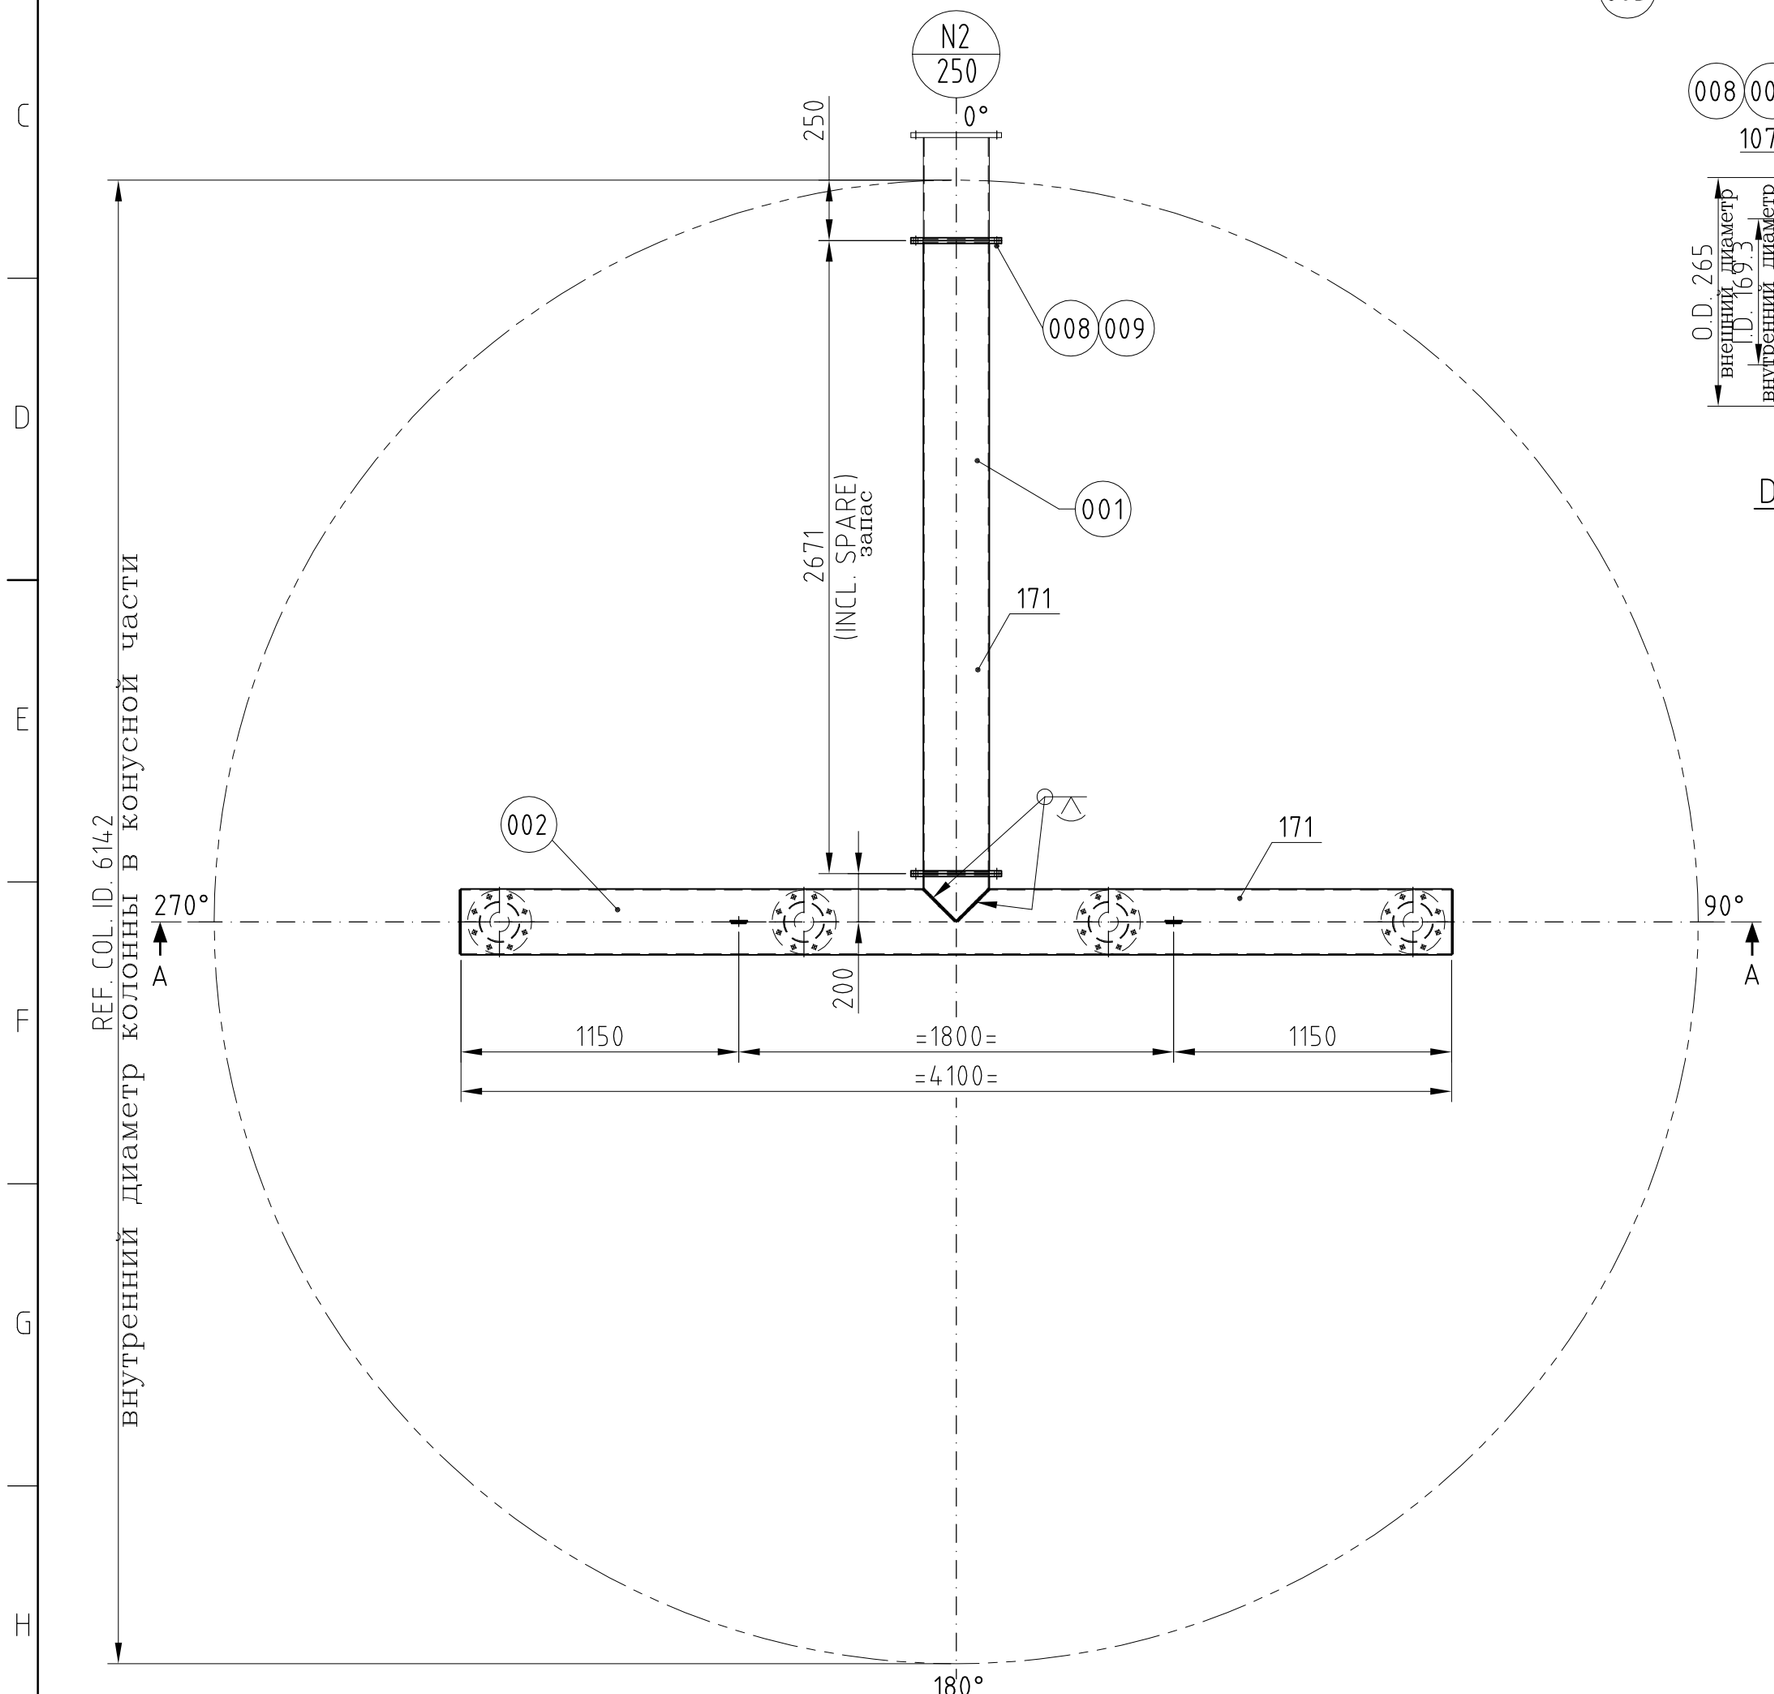

PLAN
ВИД

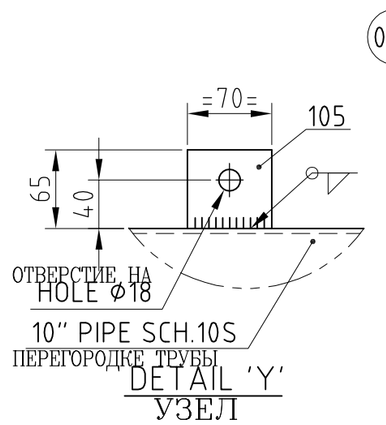

DETAIL 'Y'
УЗЕЛ

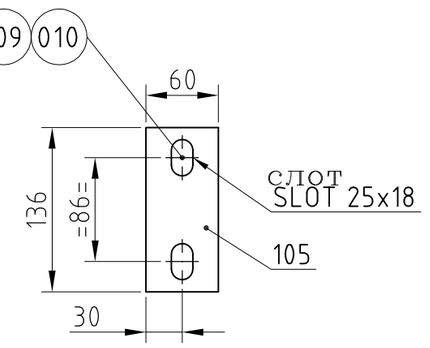

SUSPENSION
ПОДВЕСКА

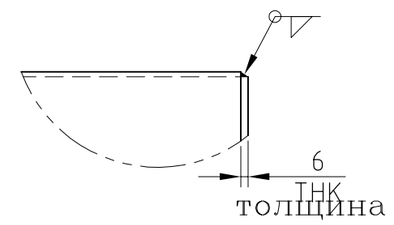

DETAIL 'D'
УЗЕЛ

NOTES -:ПРИМЕЧАНИЕ:
1. Все размеры в мм.
1. ALL DIMENSIONS ARE IN mm.
2. Все вварные проходят сквозь люк ø570мм.
2. ALL INTERNALS ARE TO PASS THROUGH MANHOLE ID.570 mm.

ПРИМЕЧАНИЯ	GENERAL NOTES
Все узлы должны проходить через люк с внутр. диам. 570 мм	All parts shall pass through man holes: 570 I.D
Все детали промаркированы ЗУЛЬЦЕРом	All components are marked by SULZER.
Сборочные узлы проверяются после изготовления	The assembled part is checked after manufact.
обработка поверхности:	surface treatment:
☐ без обработки ☒ только приварено	☐ without ☒ welding joints only
☐ протравлено ☐ нейтрализовано	☐ pickled ☐ degreased

shop data files:
1000089773

Изм.	Описание	Выполнил	Дата	Проверил	Дата	Утвердил	Дата
00	Original issue	PATILSH	27.01.2011	PURANIKMA	27.01.2011	PURANIKMA	27.01.2011
rev.	revision remarks	issued by	date	checked	date	approved	date

SAP# 213933406.00102002 C | Проект Project: 213933406 CACNEFT | формат AZ | масштаб scale: NTS
Sec-ID:6400 диаметр колонны | заказчик Customer: SALAVATNEFTEORGSINTHEZ JSC | customer-P.O.: 2139334.06
Col-NO.7 Tag:001 K-300 VACUUM T | установка Service/Unit: | customer-dwg.:
Bed:BED 1 | AB | блок Plant/Area: | End user:

Drawing-state: стадия
CERTIFIED FINAL

SULZER

LTT Liq. Inlet T-shape -ID 6400mm
Т-образная труба ввода жидкости

drawing-no.: номер чертежа
2139334-001-007-1/1

This document is entrusted to the recipient personally. The copyright remains with SULZER CHEMTECH. Recipients must obtain written authority of the said company before wholly or partly use or duplicating the contents or disclosing same to others. All rights reserved.

1000089772-DRW