item	qty.	spare	unit	drawing- or part-no.	description	remarks	material	wght. [kg]
000	1	-	PC	2139334-001-009	IV Predistributor -ID 6400mm предраспределитель		14000/4105	69
001	2	-	PC	300000256	Segments сегменты			
100	69	-	KG	10004364	Sheet 1.5x1500x4000 лист		14000/4105	-
101	2	-	PC	300000305	Connecting piece соединительная деталь			
102	4	-	PC	10007313	Hex bolt DIN933 M10x30 болт		A-193Gr.B6X	0.026
103	4	-	PC	10006678	Hex nut DIN934 M10 гайка		A-194Gr.6	0.012

001 - 099: parts / 100 - 199: materials 001–099: детали / 100–199: материалы

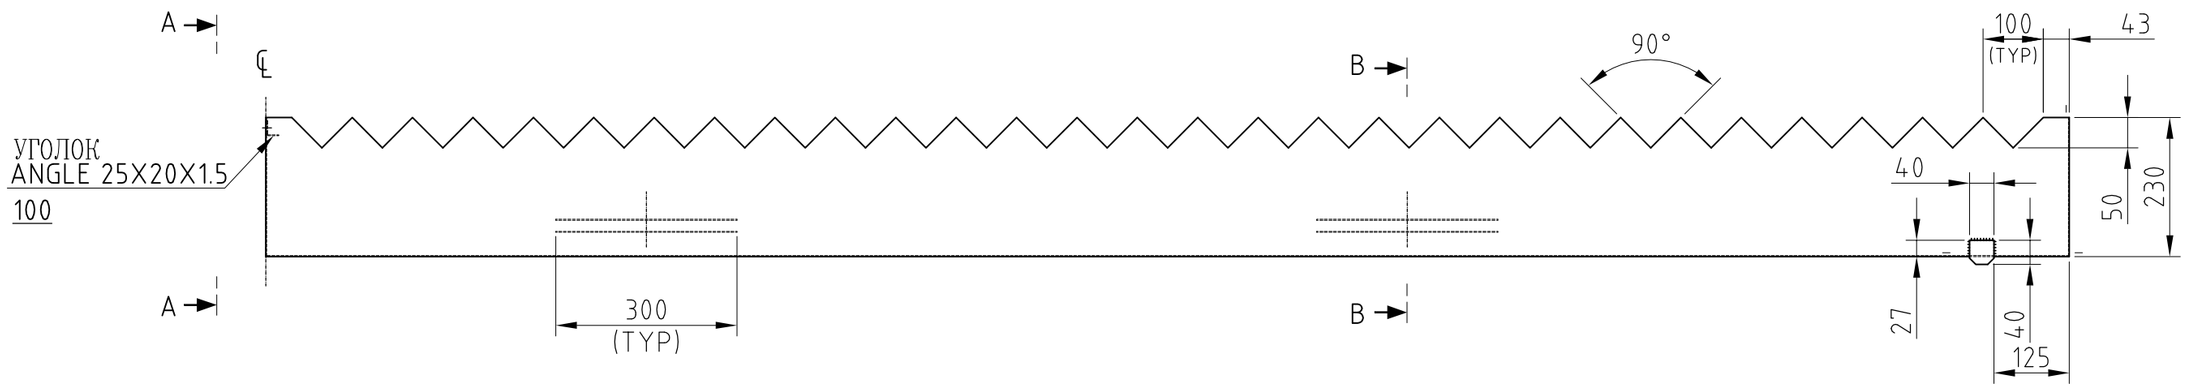

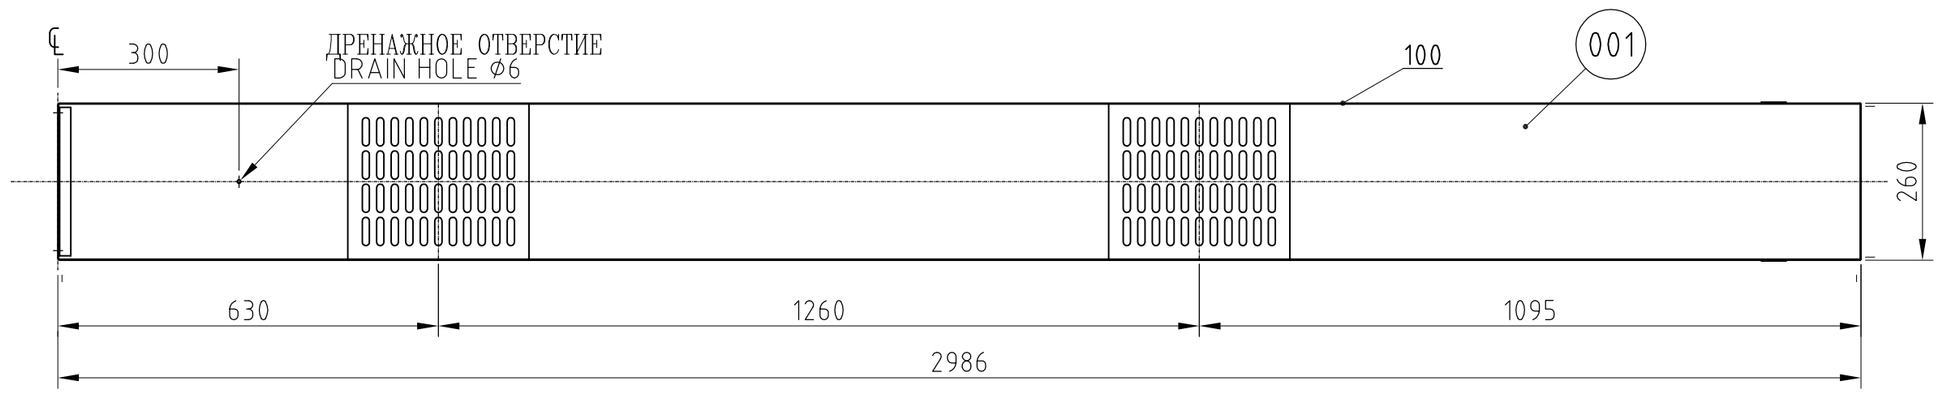

PLAN
ВИД

Характеристика предраспределителя

Pre Distributor Data

DN inlettube номинальный диаметр вводной трубы 150 [mm]
Number of Inlet Pipes: число вводных труб 4 [-]
Часть распределитель:
Belongs to Distributor: 2139334-001-005

	Flow [m3/h]	уровень над отверстием level above orifice [mm]
мин. min.	157.74	переполнение за вырезами overflow over notches
макс. max.	315.48	переполнение за вырезами overflow over notches

ПРИМЕЧАНИЯ

Все узлы должны проходить через люк с внутр. диам. 570 мм
Все детали промаркированы ЗУЛЬЦЕРом
Сборочные узлы проверяются после изготовления

обработка поверхности:

☐ без обработки ☒ только приварено
☐ протравлено ☐ нейтрализовано

GENERAL NOTES

All parts shall pass through man holes: 570 I.D.
All components are marked by SULZER.
The assembled part is checked after manufact.

surface treatment:

☐ without ☒ welding joints only
☐ pickled ☐ degreased

shop data files:
1000089775

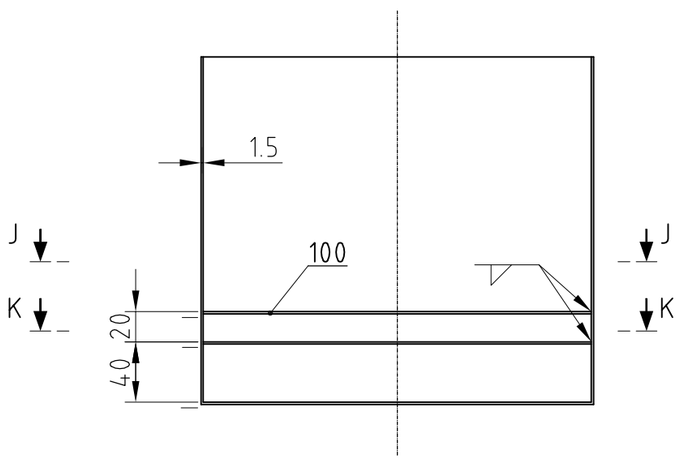

SECTION B-B
СЕЧЕНИЕ

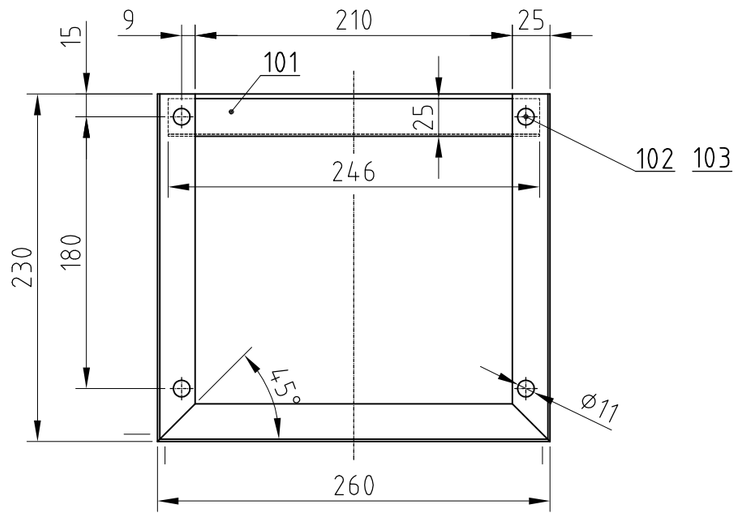

SECTION A-A
СЕЧЕНИЕ

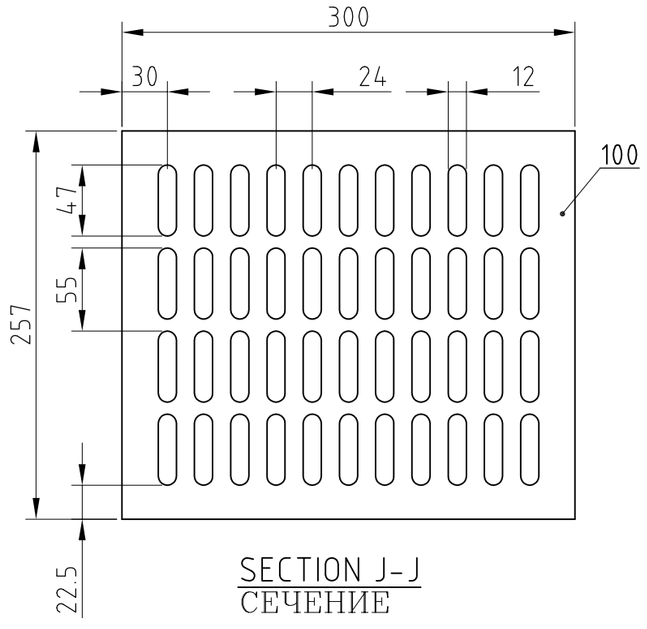

SECTION J-J
СЕЧЕНИЕ

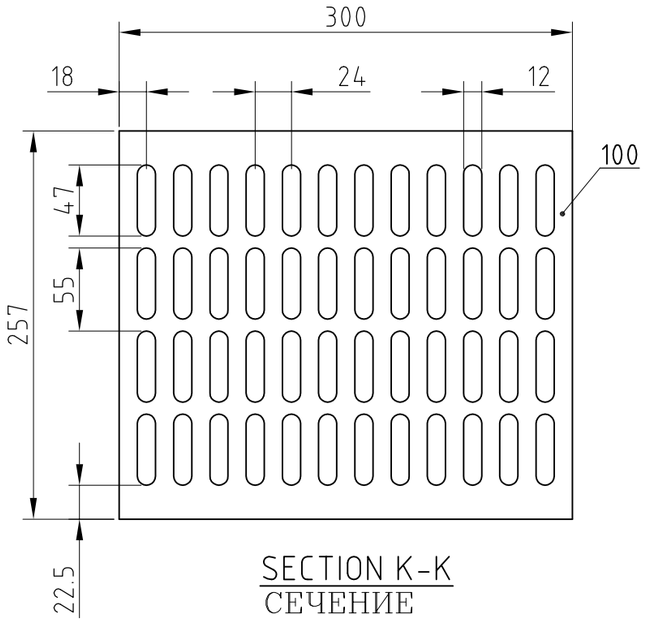

SECTION K-K
СЕЧЕНИЕ

Изм.	Описание	Выполнил	Дата	Проверил	Дата	Утвердил	Дата
00	Original issue	PATIL SH	25.01.2011	PURANKMA	25.01.2011	THAKAREAM	25.01.2011
rev.	revision remarks	issued by	date	checked	date	approved	date

SAP# 2139334.06.00102003 C | Проект Project: 2139334.06 CACNEFT | формат A2 | масштаб scale: NTS
Sec-ID: 6400 диаметр колонны | заказчик customer: SALAVATNEFTEORGSINTHEZ JSC | customer-P.O.: 2139334.06
Col-NO./Tag: 001 K-300 VACUUM T | установка Service/Unit: | customer-dwg.:
Bed: BED 1 | AB | район Plant/Area: | End user:

SULZER

IV Predistributor -ID 6400mm
Предраспределитель

drawing-no.: номер чертежа
2139334-001-009-1/1

Drawing-state: стадия
CERTIFIED FINAL

This document is entrusted to the recipient personally. The copyright remains with SULZER CHEMTECH. Recipients must obtain written authority of the said company before wholly or partly use or duplicating the contents or disclosing same to others. All rights reserved.

1000089774-DRW