


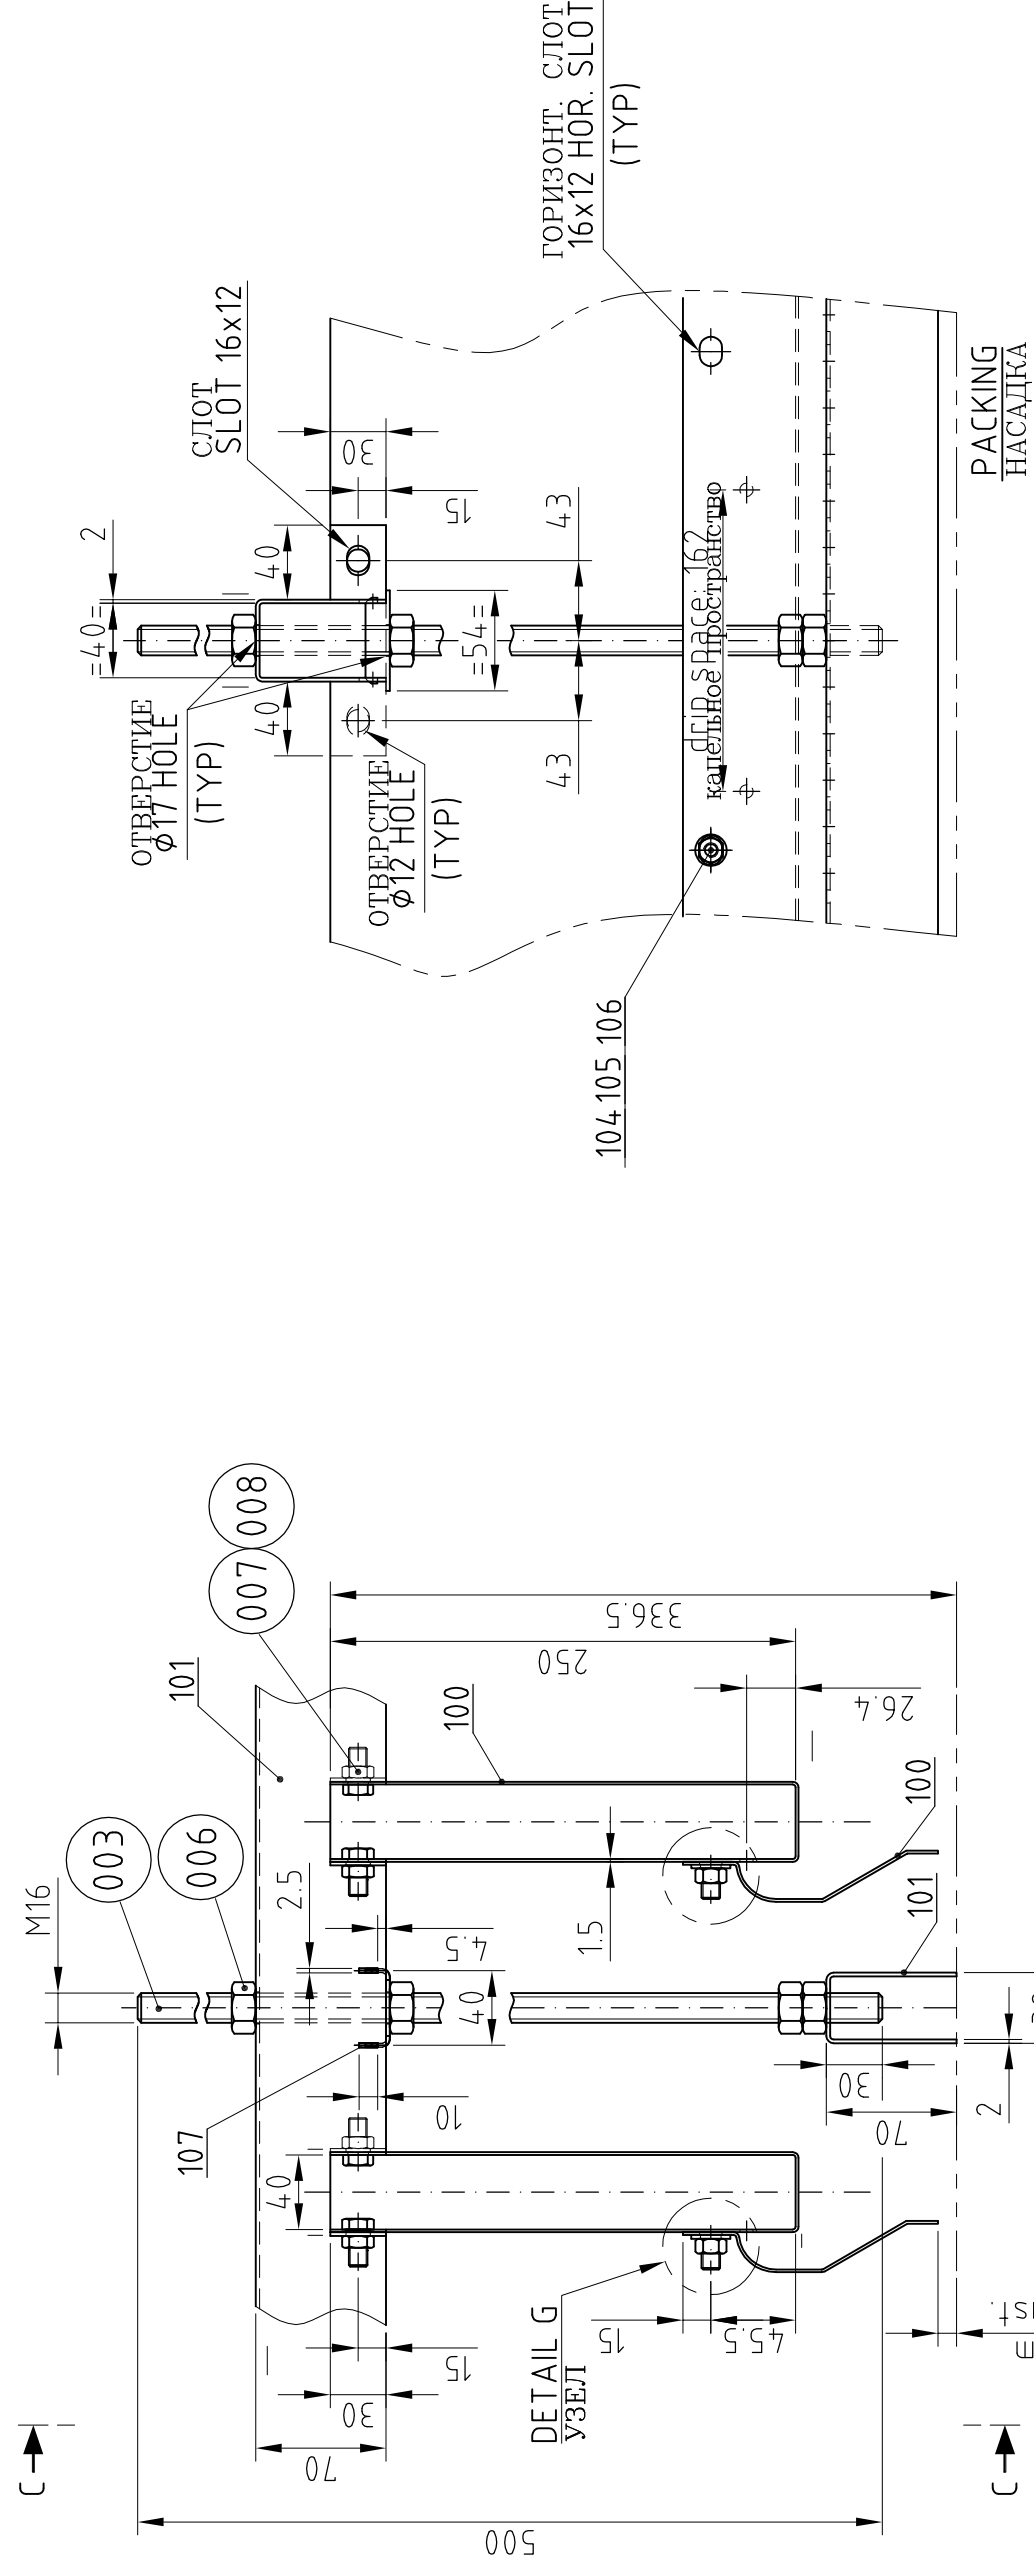


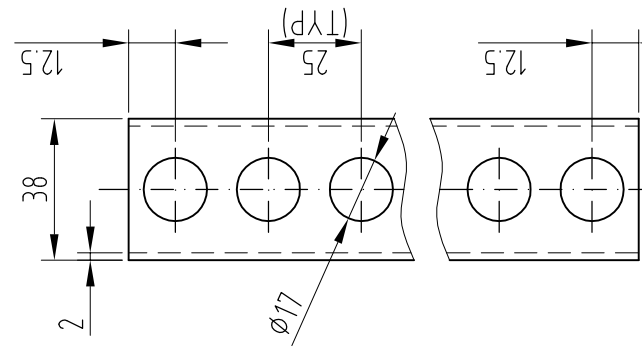

SECTION B-B  
СЕЧЕНИЕ

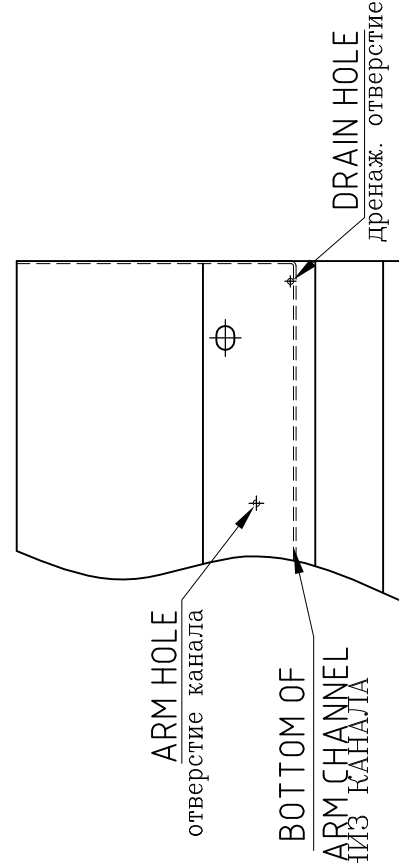


НИЖНЯЯ РЕШЕТКА  
BOTTOM GRID (005)  
FOR LOCATING GRID SYSTEM  
BEGINNING AND END OF PROFILE  
НАЧАЛО И КОНЕЦ ПРОФИЛЯ  
ДЛЯ СИСТЕМЫ РЕШЕТКИ

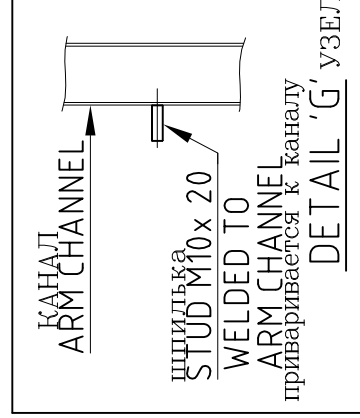


### DRAIN HOLE DETAIL


### УЗЕЛ ДРЕНАЖНОГО ОТВЕРСТИЯ

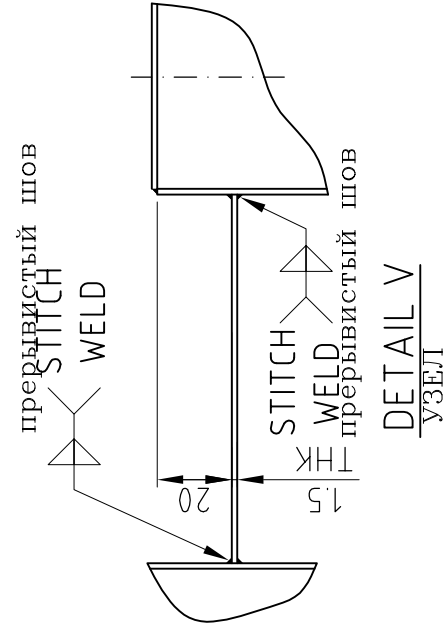


DETAIL V

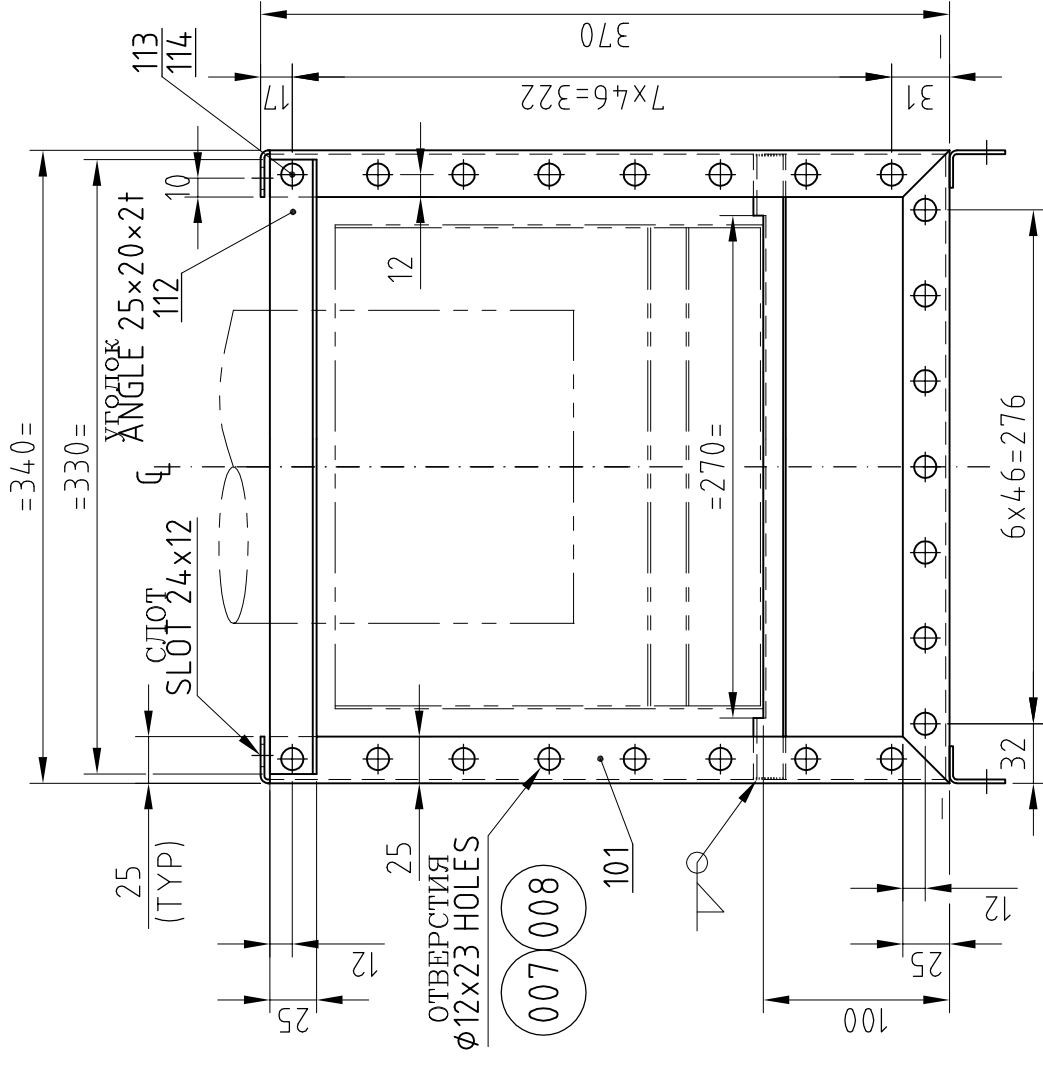

## SECTION E-E

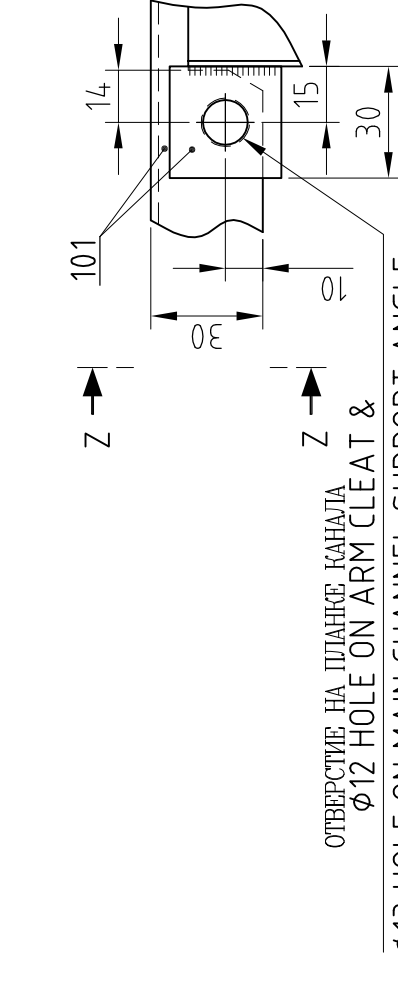

DETAIL Y

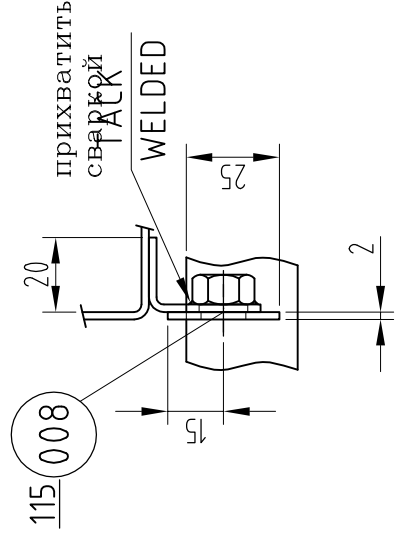

SECTION Z-Z  
СЧЕТИЕ

| Изм.                           | Описание              | Выполнен                            | Дата       | Проверен | Дата          | Утвержден          |
|--------------------------------|-----------------------|-------------------------------------|------------|----------|---------------|--------------------|
| 00                             | ORIGINAL ISSUE        | HENDOCHE                            | 75.01.2011 | PIRAMKA  | 25.01.2011    | PIRAMKA 25.01.2011 |
|                                | rev. revision remarks | issued by                           | date       | checked  | date approved | date               |
| SAP# 2193334.06                | 00104.001 C           | Project - 2193334.06                | CACNET     | PIRAMKA  | 25.01.2011    | PIRAMKA 25.01.2011 |
| Sec-ID: 64.00                  | document              | Customer: SALAVINFEEDINGSINHELZ JSC |            |          |               |                    |
| Coling Tag: 001 K-300 VACUUM T | Service/Unit:         | customer-P.O.: Z193334.06           |            |          |               |                    |
| Ref: AA                        | Plant/Area:           | customer-dwg:                       |            |          |               |                    |
| Ref: B                         |                       | End user:                           |            |          |               |                    |

|               |                                               |                                                   |
|---------------|-----------------------------------------------|---------------------------------------------------|
| <b>SULZER</b> | VEP Distributor -ID 64.00mm<br>РАСПРЕДЕЛИТЕЛЬ | drawing-no. номер чертежа<br>2139334-001-019 -2/2 |
|---------------|-----------------------------------------------|---------------------------------------------------|

This document is entrusted to the recipient personally. The copyright remains with SULZER CHEMTECH. Recipients must obtain written

Drawing-state: стадия