
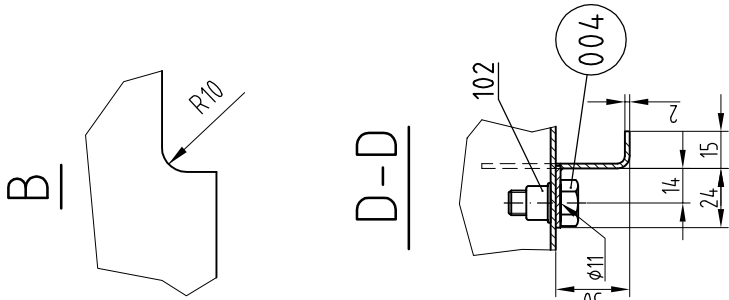


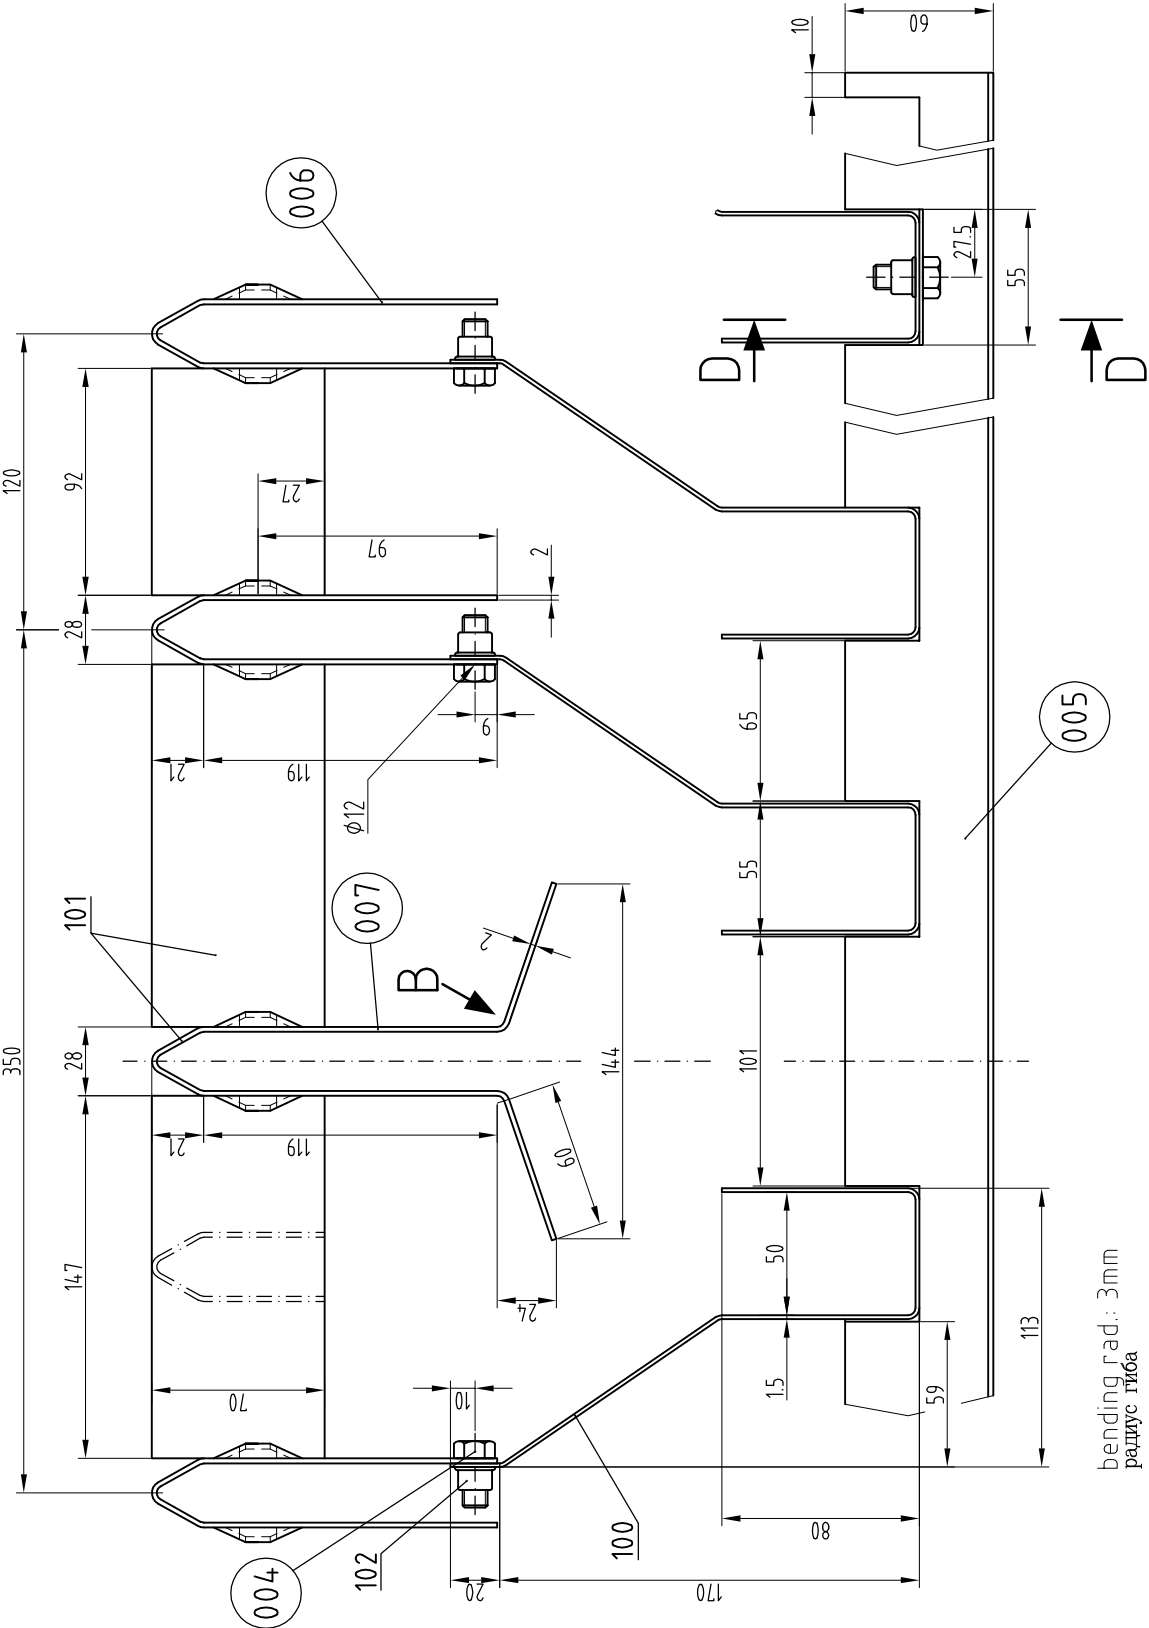

Изм.	Описание	Выполнил	Дата	Проверил	Дата	Утвердил	Дата
00	ORIGINAL ISSUE	PATLSH	25.01.2011	PURANKMA	25.01.2011	THAKAREAM	25.01.2011
rev.	revision remarks	issued by	date	checked	date	approved	date
SAP# 2139334.06.00104.003		Project: 2139334.06		CACNEFT		scale: NTS	
Sec-ID: 64.00		Customer: SALAVATNEFTORGINSINTEZ JSC		customer-P.O.: 2139334.06			
Customer: SALAVATNEFTORGINSINTEZ JSC		Service/Unit:		customer-dwg.:			
Col-No/Tag-001 K-300 VACUUM T		AA		End user:			
Ver: 2							
				drawing no.: номер чертежа			
				2139334-001-023-2/2			
SULZER		SLMT Collector / Support -ID 64.00mm		коллектор / опора			
This document is entrusted to the recipient personally. The copyright remains with SULZER CHEMTECH. Recipient's must obtain written authority of the said company before wholly or partly use or duplicating the contents or disclosing same to others. All rights reserved.							