item	qty.	spare	unit	drawing- or part-no.	description	remarks	material	wght.[kg]
000	1	-	PC	2139334-001-025	BET10 Beam for TS -ID 6400mm	балка каплеотбойника	14000/4105	496
001	2	-	PC	300000278	Beam	балка		
002	17	2	PC	10005025	Hex bolt DIN933 M16x60	болт	A2	0.117
003	21	2	PC	10006673	Hex nut DIN934 M16	гайка	A-194Gr.6	0.033
004	28	2	PC	10002716	Washer 17/32x3	шайба	14000/4105	0.014
105	493	-	KG	10004525	Sheet 10x1500x3000	лист	14000/4105	-

1

001 - 099: parts / 100 - 199: materials 001–009: части / 100–199: материалы

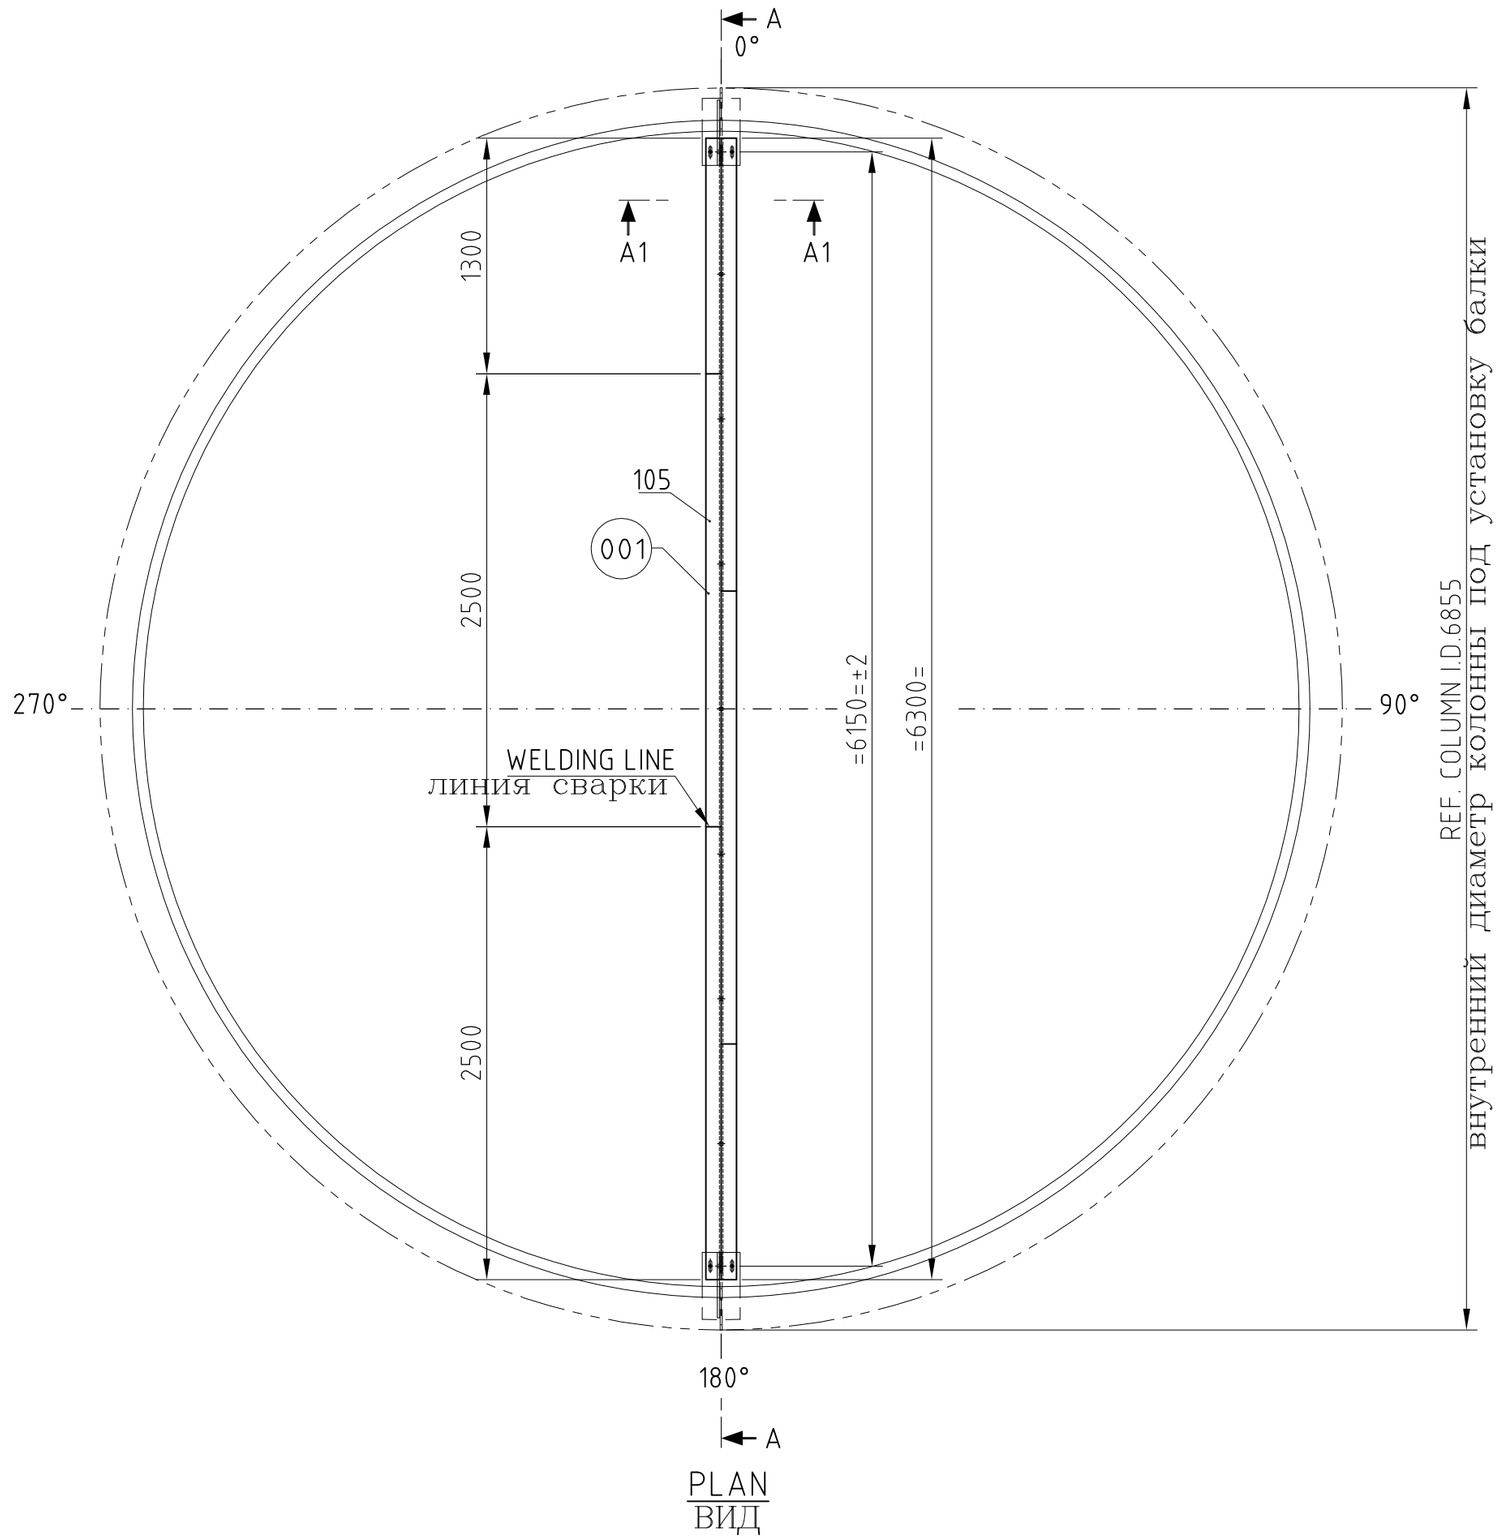

PLAN
ВИД

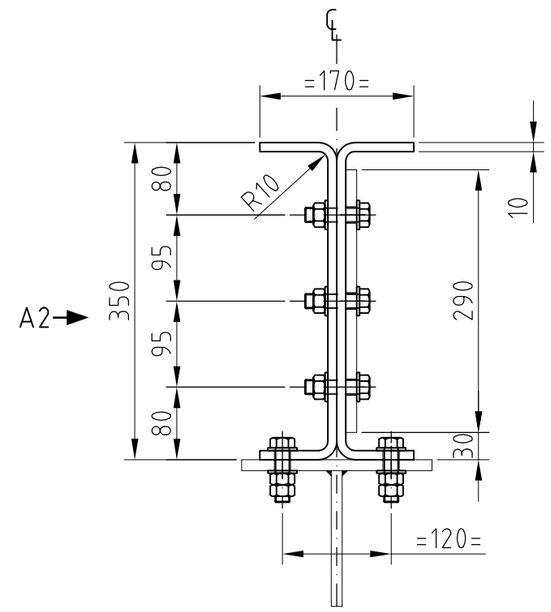

SECTION A1-A1
сечение

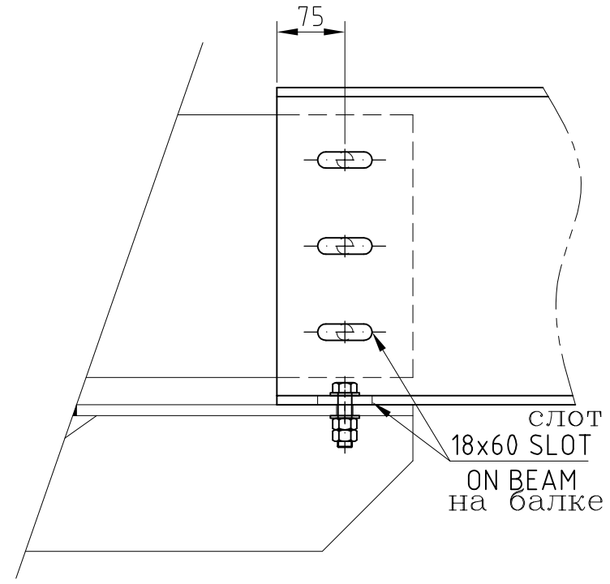

VIEW A2
вид

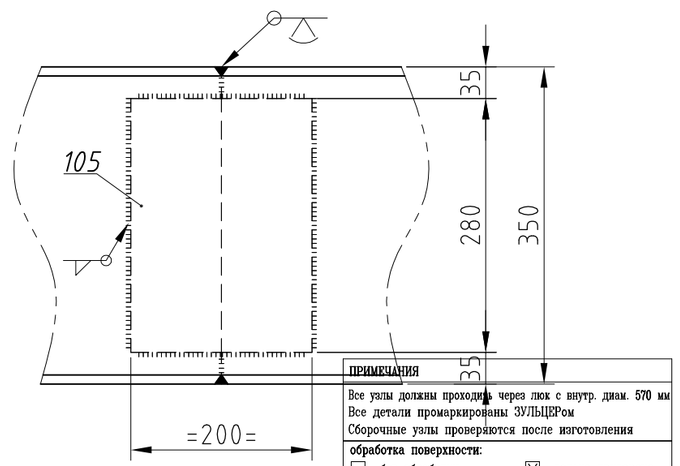

ПРИМЕЧАНИЯ	
Все узлы должны проходить через люк с внутр. диам. 570 мм Все детали промаркированы ЗУЛЬЦЕРом Сборочные узлы проверяются после изготовления	
обработка поверхности:	
☐ без обработки	☒ только приварено
☐ протравлено	☐ нейтрализовано

DETAIL A3
УЗЕЛ

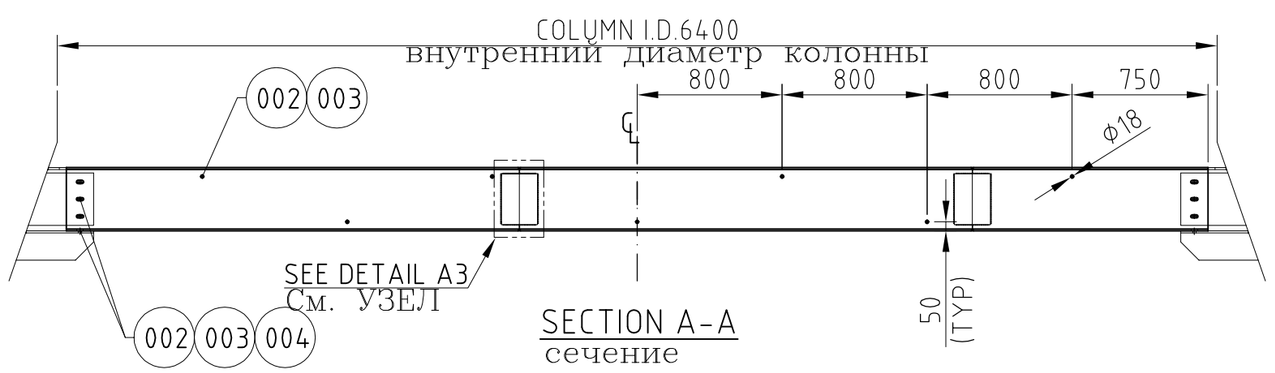

SECTION A-A
сечение

ПРИМЕЧАНИЯ	
Все узлы должны проходить через люк с внутр. диам. 570 мм Все детали промаркированы ЗУЛЬЦЕРом Сборочные узлы проверяются после изготовления	
обработка поверхности:	
☐ без обработки	☒ только приварено
☐ протравлено	☐ нейтрализовано

GENERAL NOTES	
All parts shall pass thr. a man way:	570 I.D.
All components are marked by SULZER The assembled part is checked after manufact.	
surface treatment:	
☐ without	☒ welding joints only
☐ pickled	☐ degreased
shop data files: 1000089791	

NOTE:Примечание:

1) MARK THUS ⚑ TO BE WELDED AT SITE.
1)Помеченное флажком приваривается при монтаже

rev.	revision remarks описание изменений	issued by выпустил	date дата	checked проверил	date дата	approved утвердил	date дата
01	Design revision	PATILDA	01.06.2011	PURANIKMA	03.06.2011	HANDESH	03.06.2011
00	original issue исходные данные	PATILSH	25.01.2011	PURANIKMA	25.01.2011	THAKAREAM	25.01.2011

SAP# 213933406.00104004 C | Project: 213933406 CACNEFT | A2 | scale: NTS

Sec-ID:6400 | Customer: SALAVATNEFTEORGSINTHEZ JSC | Customer-P.O.: 2139334.06

Loi-No./Tag.001 K-300 VACUUM T | Service/Unit: | End user:

Bed:2 | AC | Plant/Area:

SULZER

BET10 Beam for TS -ID 6400mm
балка

drawing-no.: 2139334-001-025-1/1

Drawing-state: стадия
CERTIFIED FINAL

This document is entrusted to the recipient personally. The copyright remains with SULZER CHEMTECH. Recipients must obtain written authority of the said company before wholly or partly use or duplicating the contents or disclosing same to others. All rights reserved.

1000089790-DRW