item	qty	запас	ед.изм	позиц. чертежа/деталь	Наименование / description	примечание / remarks	материал / material	масса (кг) / wght. (kg)
000	1	-	PC	2139334-001-027	Downpipes -ID 6400mm сливные трубы		14008/4M5	294
001-002	6	-	PC	300000210	Pipe with flange труба с фланцем			
003	6	-	PC	300000209	Pipe труба			
004	96	10	PC	10006646	Hex bolt DIN933 M16x60 болт		A-193Gr.B8	0.114
005	120	12	PC	10006683	Hex nut DIN934 M16 гайка		A-194Gr.8	0.033
006	6	-	PC	10005638	U-Bolt DIN3570 DN150 у-образный болт		1.4301/304	0.9
007	24	2	PC	10002714	Washer 17/32x3 шайба		1.4307/304L	0.014
008	12	2	PC	10006954	Hex bolt DIN933 M10x20 болт		A-193Gr.B8	0.021
009	12	2	PC	10006674	Hex nut DIN934 M10 гайка		A-194Gr.8	0.012
010	6	-	PC	300000327	Angle уголок			
011	6	-	PC	10002901	Flange DN150x10 фланец		1.4307/304L	2.4
100	3	-	KG	10004451	Sheet 2x1500x3000 лист		1.4301/304L	-
107	18	-	PC	10002901	Flange DN150x10 фланец		1.4307/304L	2.4
170	15	-	M	10005222	Pipe welded 6"x10S приварная труба		1.4307/304L	14

001 - 099: parts / 100 - 199: materials 001-099: части / 100-199: материалы

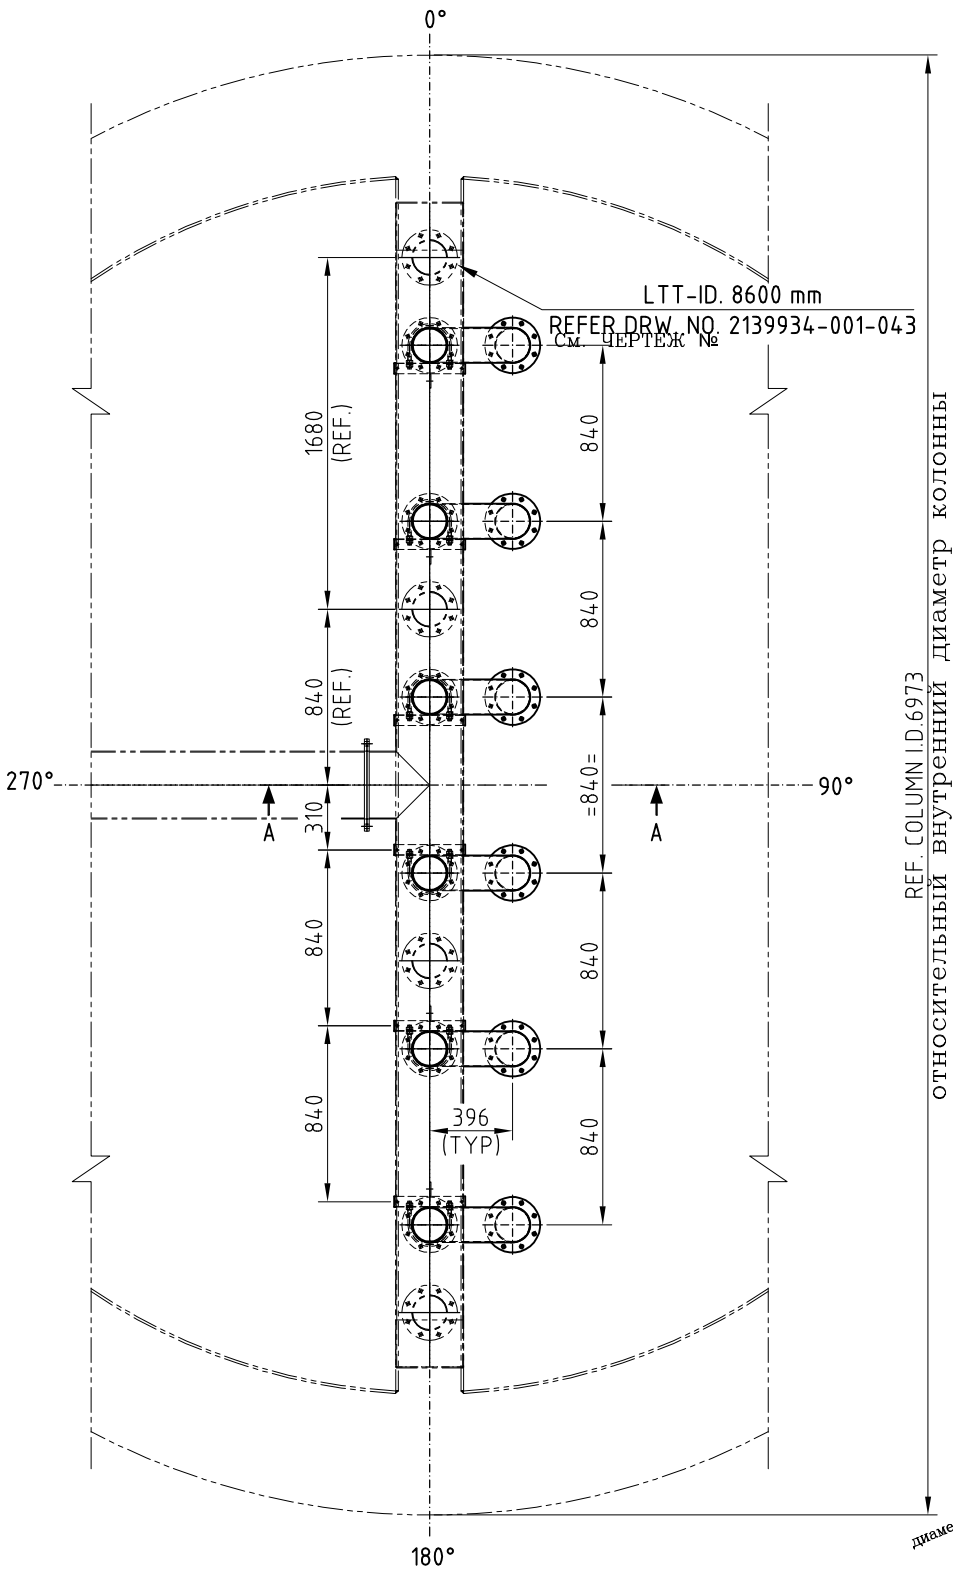

PLANвид

(MAIN CHANNEL & PRE'D OMITTED FOR CLARITY)
(ГЛАВНЫЙ КАНАЛ И ПРЕДРАСПРЕДЕЛИТЕЛЬ ОПУСХЕНЫ ДЛЯ ЯСНОСТИ)

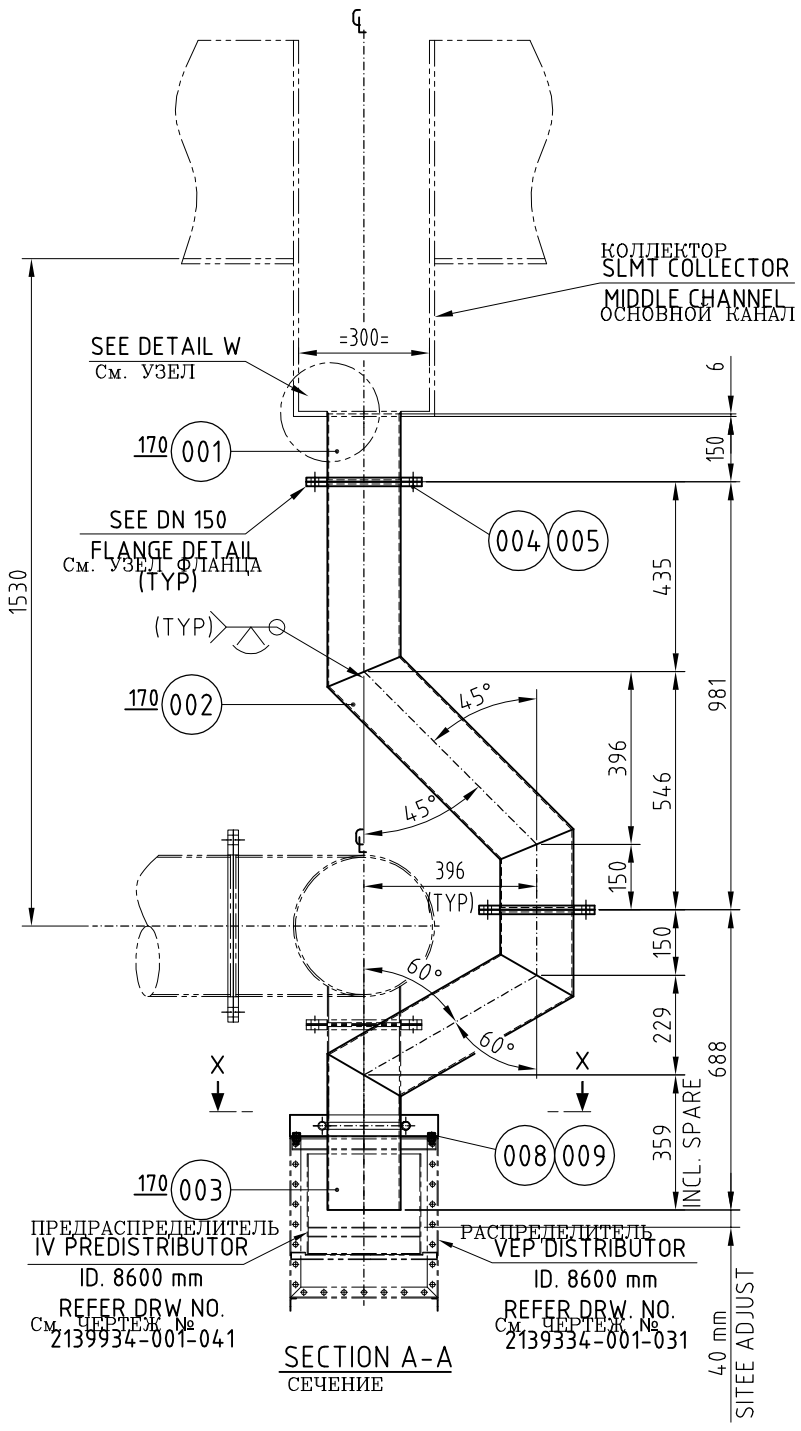

SECTION A-A
СЕЧЕНИЕ

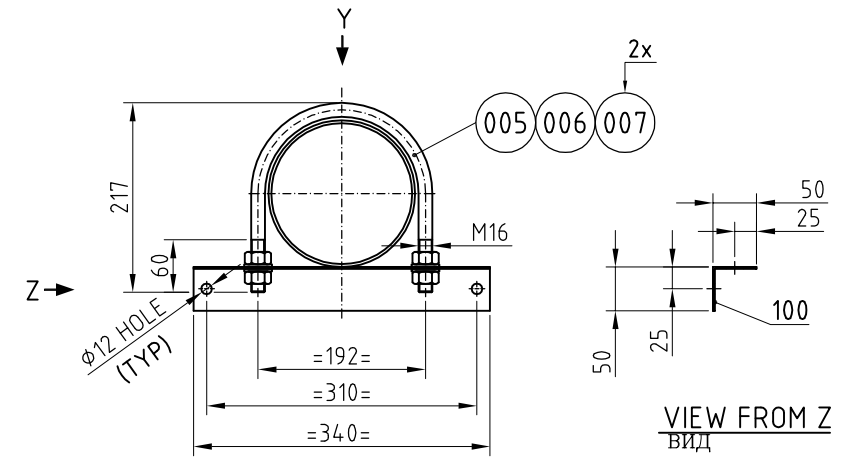

SECTION X-X
СЕЧЕНИЕ
(M16 U-BOLT FOR 6" PIPE)
У-ОБРАЗНЫЙ БОЛТ

VIEW FROM Z
ВИД

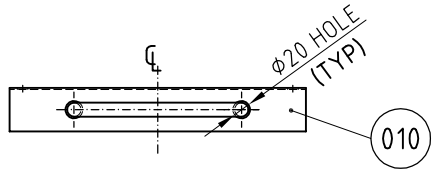

VIEW FROM Y
ВИД

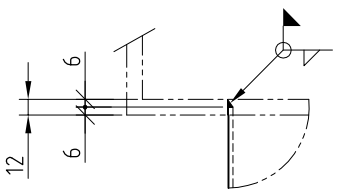

DETAIL W
УЗЕЛ

ПРИМЕЧАНИЯ

Все узлы должны проходить через люк с внутр. диам. 570 мм
Все детали промаркированы ЗУЛЬЦЕРом
Сборочные узлы проверяются после изготовления

обработка поверхности:

- [ ] без обработки
- [X] только приварено
- [ ] протравлено
- [ ] нейтрализовано

GENERAL NOTES

All parts shall pass through man holes: 570 I.D.
All components are marked by SULZER.
The assembled part is checked after manufact.

surface treatment:

- [ ] without
- [X] welding joints only
- [ ] pickled
- [ ] degreased

shop data files:
1000089793

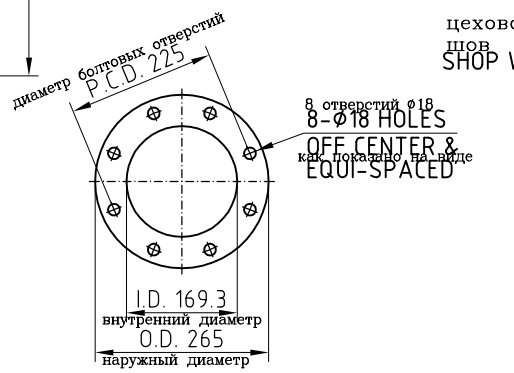

DN 150 FLANGE DETAIL
УЗЕЛ ФЛАНЦА

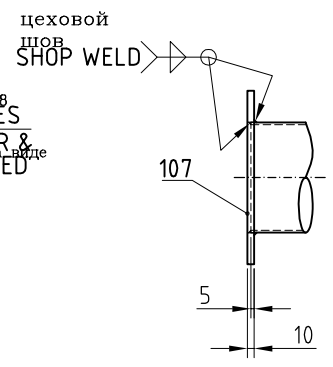

УЗЕЛ СВАРКИ ТРУБЫ С ФЛАНЦЕМ
PIPE TO FLANGE WELDING DETAIL
(FOR ITEM NO. 001 & 002 ONLY)
(ТОЛЬКО ПОЗ. № 001 И 002)

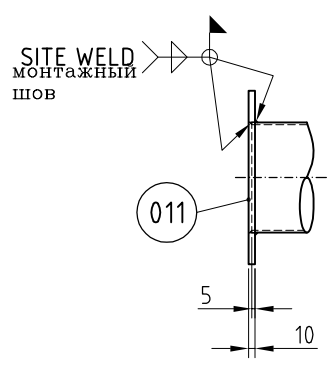

УЗЕЛ СВАРКИ ТРУБЫ С ФЛАНЦЕМ
PIPE TO FLANGE WELDING DETAIL
(FOR ITEM NO. 003 ONLY)
(ТОЛЬКО ПОЗ. № 001 И 002)

NOTE: Примечание:

1) MARK THUS ⚑ TO BE WELDED AT SITE.
1) Помеченное флажком приваривается при монтаже

Изм.	Описание	Выполнил	Дата	Проверил	Дата	Утвердил	Дата
00	Original Issue	HENDGEDE	25.01.2011	INAMDARJA	25.01.2011	PURANKMA	25.01.2011
rev.	revision remarks	issued by	date	checked	date	approved	date

SAP# 213933406.00104005 C | Project: 213933406 CACNEFT | Формат A2 | Масштаб scale: NTS
Sec-ID: 6400 диаметр колонны | Customer: SALAVATNEFTEORGSINTHEZ JSC | customer-P.O.: 2139334.06
Col-No./Tag: 001 K-300 VACUUM T | Service/Unit: | customer-dwg.:
Bed: 3 AA | Plant/Area: | End user:

SULZER

Downpipes -ID 6400mm
СЛИВНЫЕ ТРУБЫ

drawing-no.: номер чертежа
2139334-001-027 -1/1

Drawing-state: стадия
CERTIFIED FINAL

This document is entrusted to the recipient personally. The copyright remains with SULZER CHEMTECH. Recipients must obtain written authority of the said company before wholly or partly use or duplicating the contents or disclosing same to others. All rights reserved.

1000089792-DRW