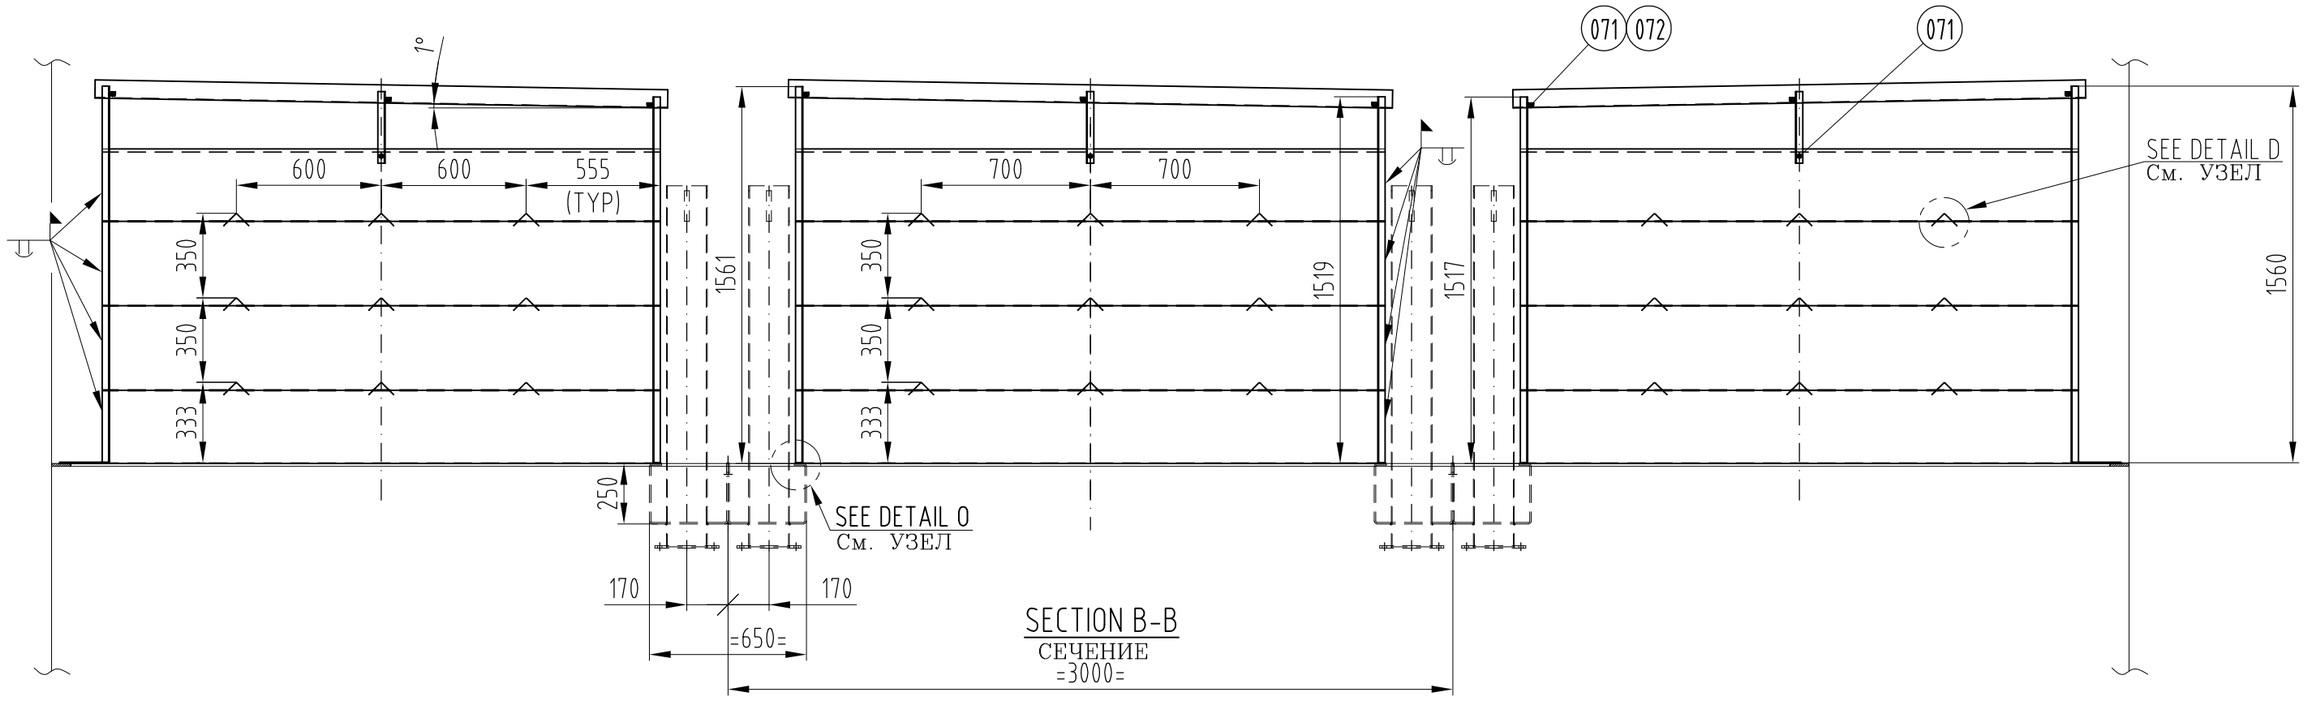

SECTION B-B
СЕЧЕНИЕ

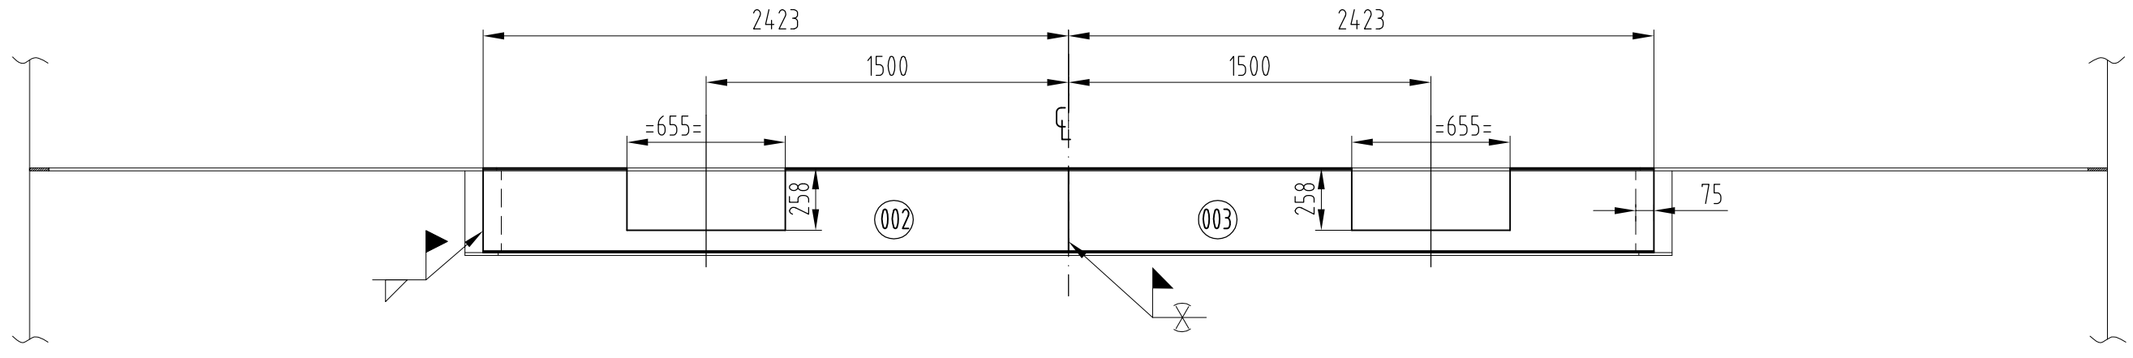

SECTION G-G
СЕЧЕНИЕ

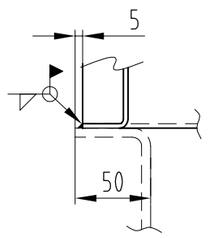

DETAIL O
УЗЕЛ

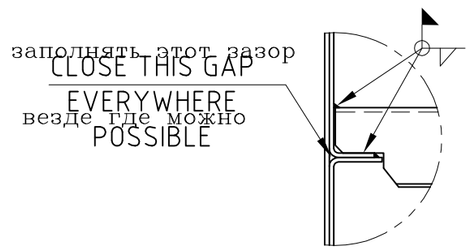

DETAIL P
УЗЕЛ

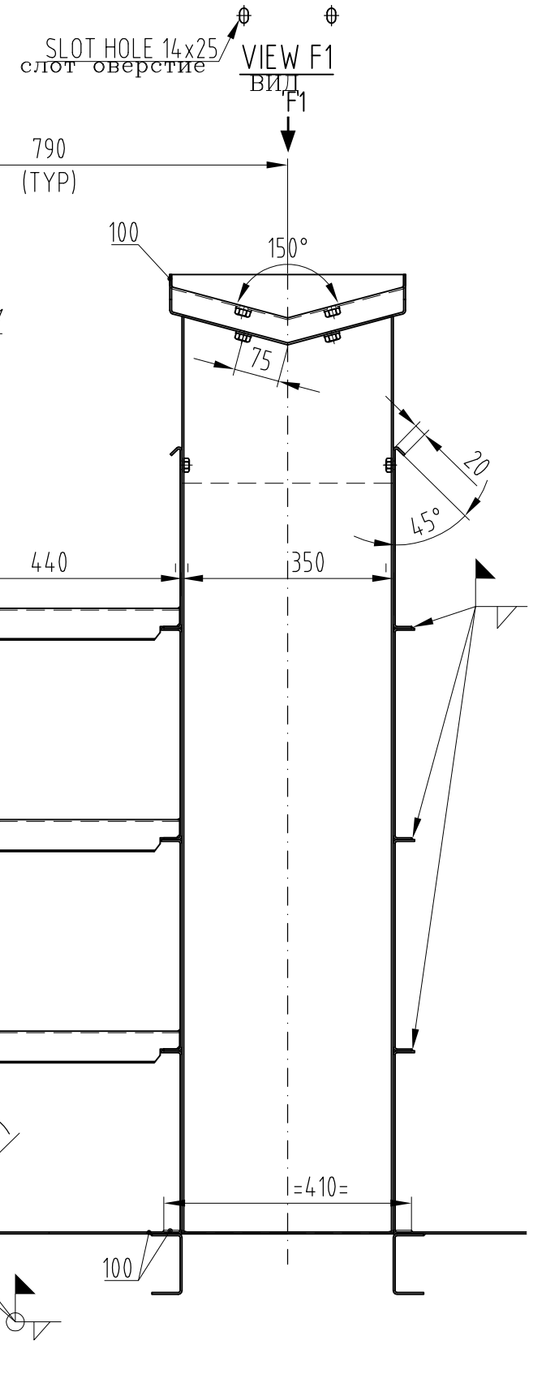

SECTION C-C
СЕЧЕНИЕ

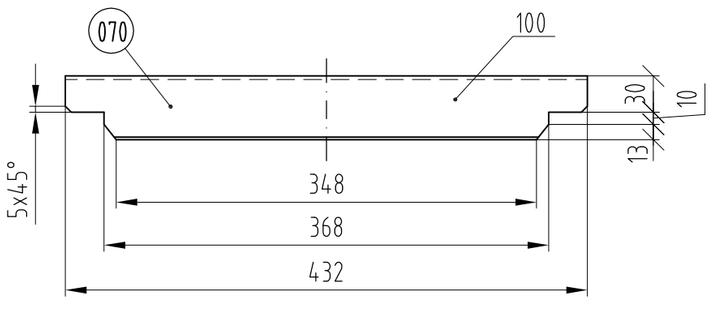

VIEW D1
ВИД

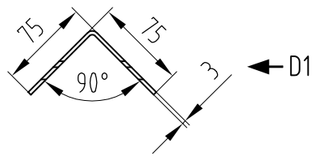

DETAIL D
УЗЕЛ

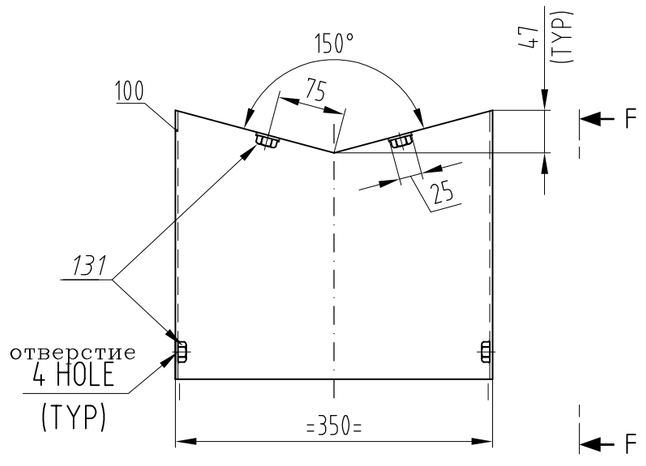

SECTION E-E
СЕЧЕНИЕ

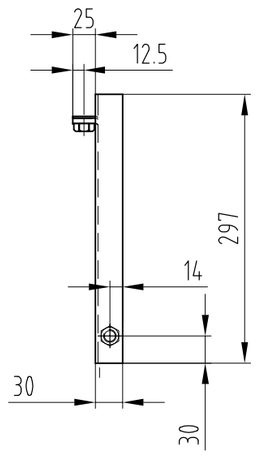

SECTION F-F
СЕЧЕНИЕ

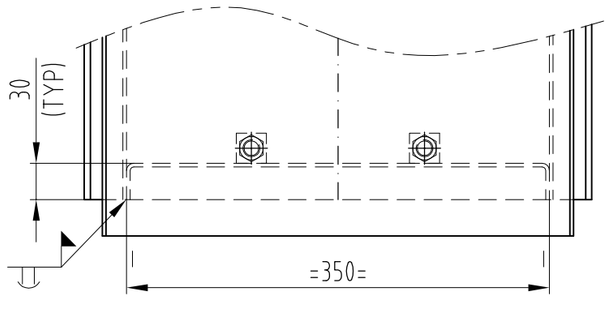

DETAIL R
УЗЕЛ

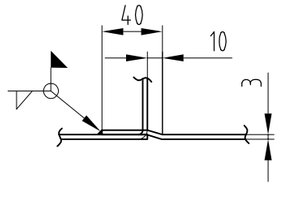

DETAIL L
УЗЕЛ

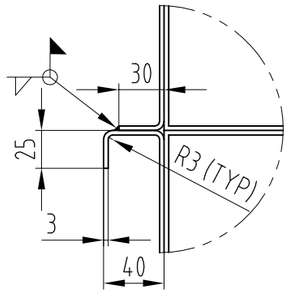

DETAIL N
УЗЕЛ

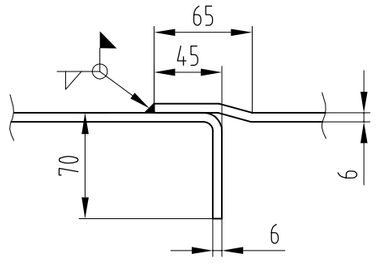

DETAIL Q
УЗЕЛ

Изм.	Описание	Выполнил	Дата	Проверил	Дата	Утвердил	Дата
01	Design revision	PATILDA	01.06.2011	PURANIKMA	03.06.2011	HANDESH	03.06.2011
00	Original Issue	PATILDA	03.02.2011	PURANIKMA	03.02.2011	HANDESH	03.02.2011
rev.	revision remarks	issued by	date	checked	date	approved	date

SAP# 2139334.06.00105002 C | Проект: Project: 213933406 CACNEFT | формат: A2 | масштаб: scale: NTS

Sec-ID: 8600 диаметр колонны | заказчик: Customer: SALAVATNEFTEORGSINTHEZ JSC | customer-P.O.: 2139334.06

Col-No./Tag: 001 K-300 VACUUM T | установка: Service/Unit: | customer-dwg.:

Bed: 3 | AB | площ.: Plant/Area: | End user:

SULZER

SKIW Chimney Tray -ID 8600mm
ГЛУХАЯ ТАРЕЛКА

drawing-no.: номер чертежа
2139334-001-033-2/2

Drawing-state: стадия
CERTIFIED FINAL

This document is entrusted to the recipient personally. The copyright remains with SULZER CHEMTECH. Recipients must obtain written authority of the said company before wholly or partly use or duplicating the contents or disclosing same to others. All rights reserved.

1000089798-DRW