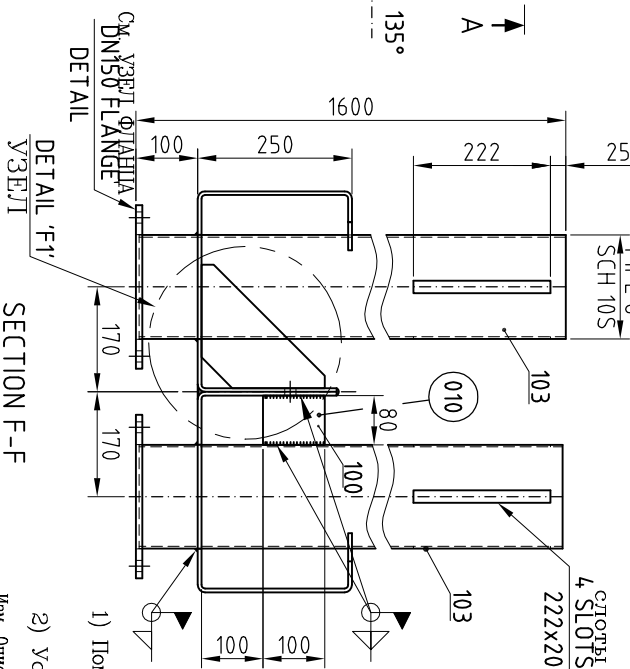
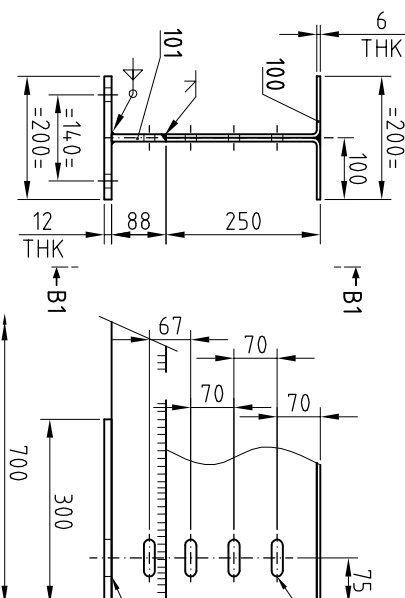
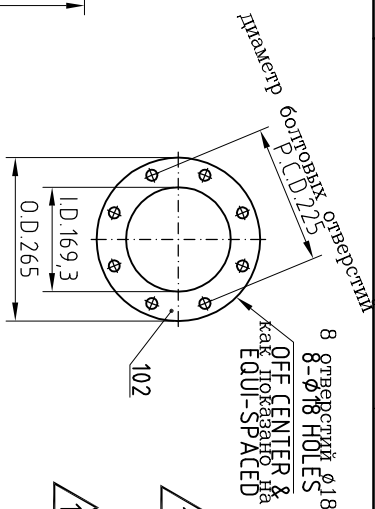
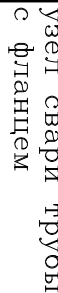
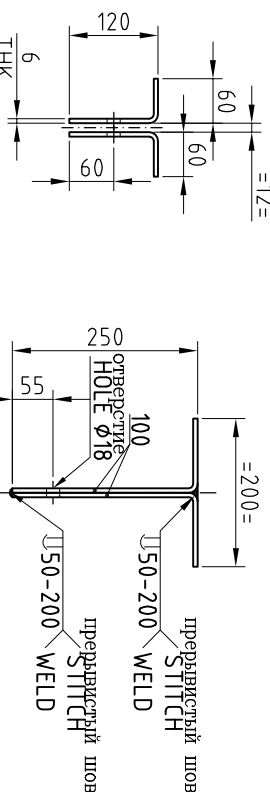
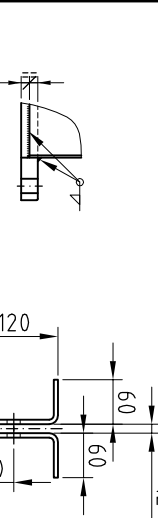
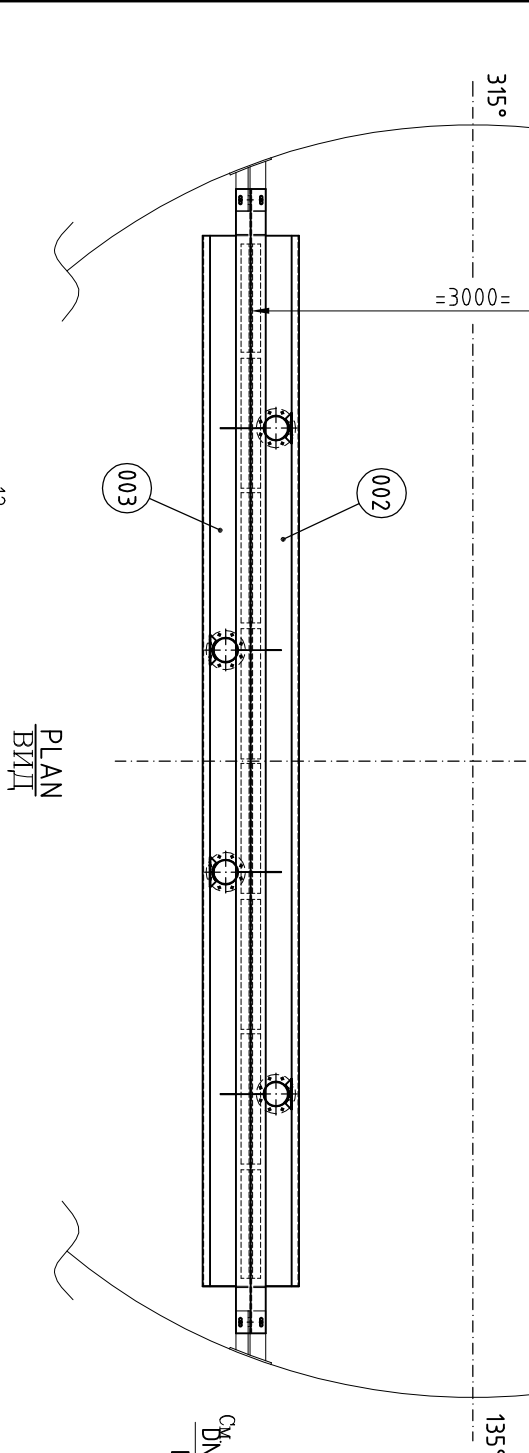
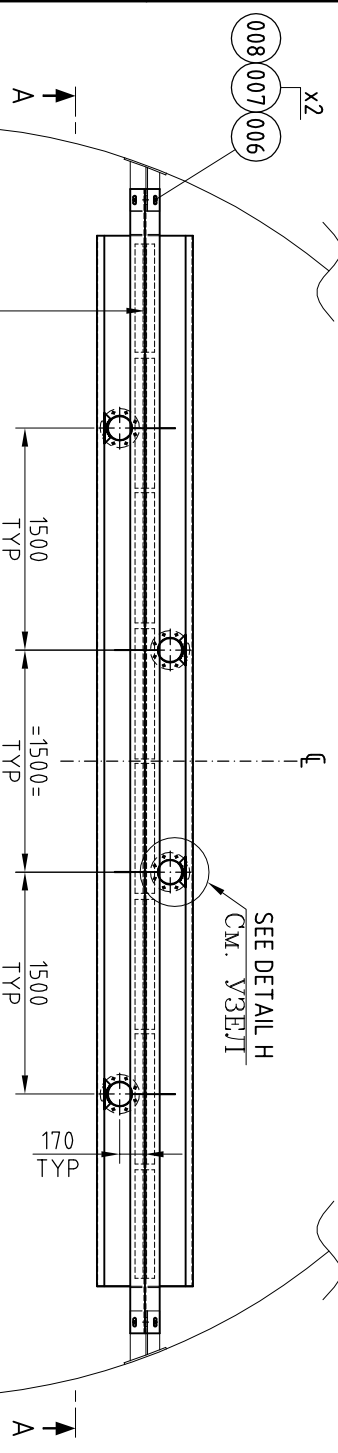
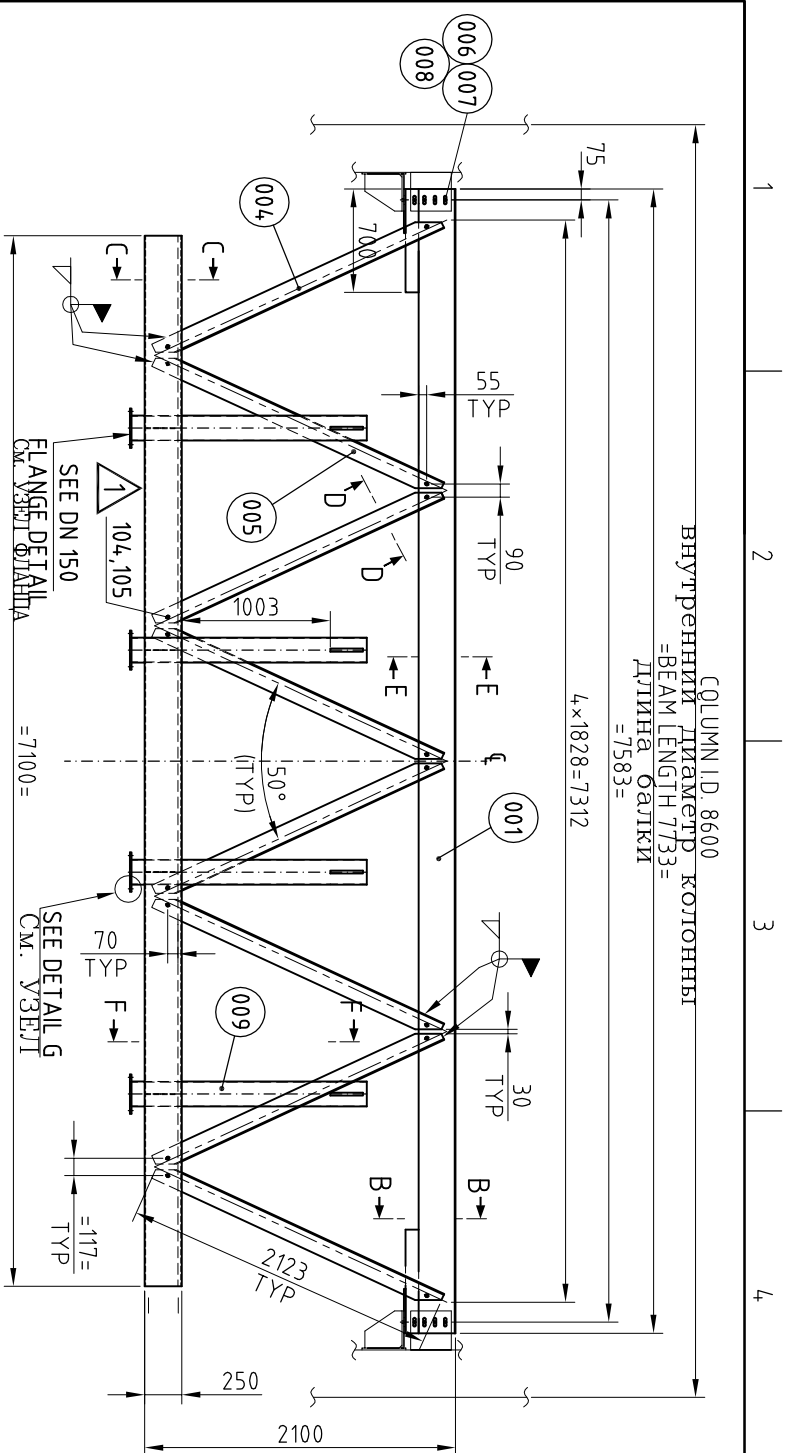
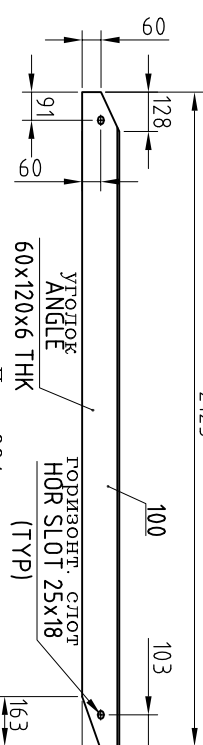
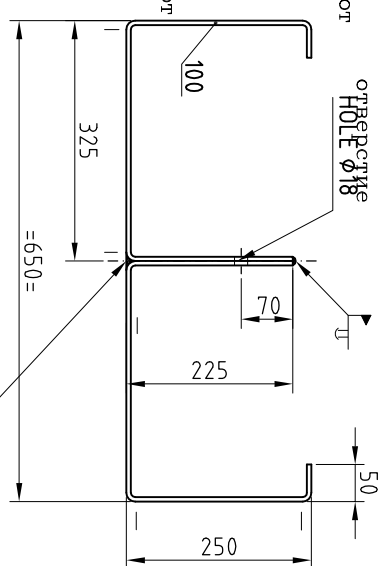
[illegible]

ITEM NO.005 (MIRROR OF ITEM NO.004)
Поз. 005 (отражение Поз. 004)

ITEM NO. 004

ПРИМЕЧАНИЕ
NOTES:

1) Помеченные флажком привариваются при монтаже
MARKED TO BE WELDED AT SITE

2) THE INSTALLATION OF PIPES SHOULD BE DONE AFTER
2) Установка труб должна быть сделана после установки решетки фермы.
THE INSTALLATION OF LATTICE GIRDER.

Код	Имя	Действие	Дата	Статус	Дата
01	Design revision	PATLDA	02.06.2011	PIRANKKA	03.06.2011
00	Original issue	TJANBYO	03.02.2011	PIRANKKA	03.02.2011
rev	revision remarks	issued by	date	checked	approved date
SAP# 219334,06	00705004,	C	Project: 219334,06	CACNET	
Sec-ID: 8600	Customer: SALAVANTIEFONGSINTHEZ JSC				
Col-No./Tag-001 K-300 YACUMT	Customer Service/Unit:				
Ref. 3	End user:				

Doc. J	PC PLASTICATED	CIN. DATE:	drawing - no.: номер чертежа
SULZER	BL Lattice beams -ID 8600mm PELLETQTATAY BAVKA		2139334-001-037-1/1