

item	qty.	spare	unit	drawing- or part-no.	description	remarks	material	weight [kg]
000	1	-	PC	2139334-001-039	Downpipes -ID 8600mm сливные трубы		1.4307	331
001–004	2	-	PC	300000209	Pipe труба			
005	8	-	PC	300000327	Angle уголок			
006–009	2	-	PC	300000029	Suspension подвеска			
010	16	-	PC	300001067	Lug проушина			
011	80	8	PC	10006646	Hex bolt DIN933 M16x60 болт		A-1936r.88	0.114
012	112	11	PC	10006683	Hex nut DIN934 M16 гайка		A-1946r.8	0.033
013	8	-	PC	10005638	U-Bolt DIN3570 DN150 У-образный болт		1.4301/304	0.9
014	48	5	PC	10002714	Washer 17/32x3 шайба		1.4307/304L	0.014
015	16	2	PC	10006954	Hex bolt DIN933 M10x20 болт		A-1936r.88	0.021
016	16	2	PC	10006674	Hex nut DIN934 M10 гайка		A-1946r.8	0.012
017	8	-	PC	10002901	Flange DN150x10 фланец		1.4307/304L	2.4
100	20	-	KG	10004451	Sheet 2x1500x3000 лист		1.4307/304L	-
101	6	-	KG	10004455	Sheet 6x1500x3000 лист		1.4307/304L	-
102	18.7	-	M	10005222	Pipe welded 6"x10S приварная труба		1.4307/304L	14

001 - 099: parts / 100 - 199: materials 001–099: части / 100–199: материалы

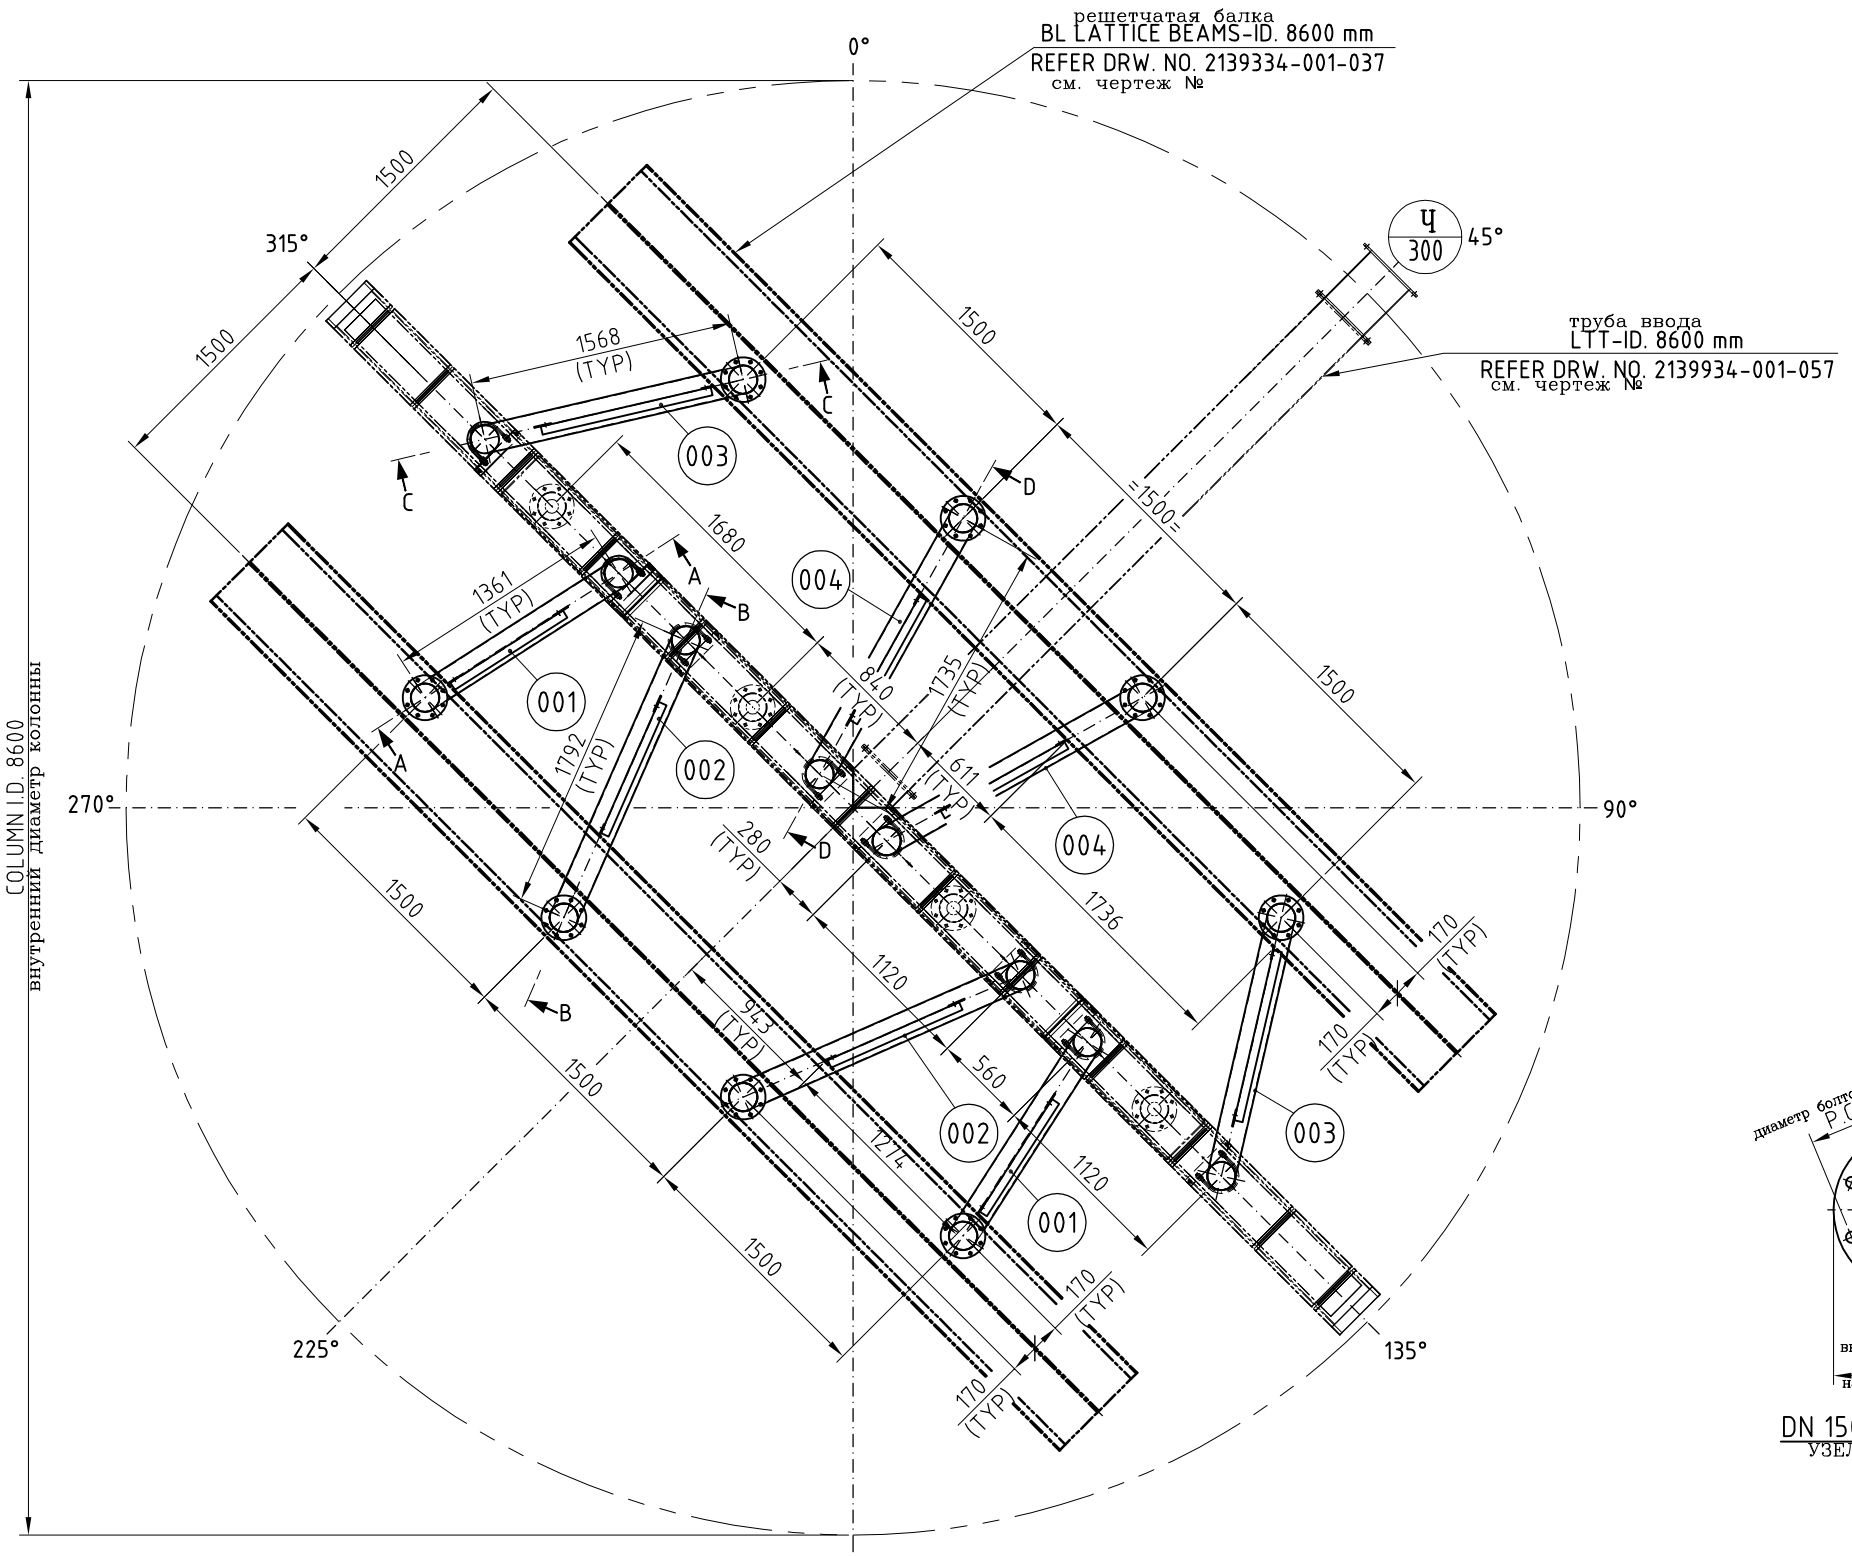


PLAN вид

(CALMING PLATE OMMITED FOR CLARITY)
(успокаивающая пластина опущена для ясности)

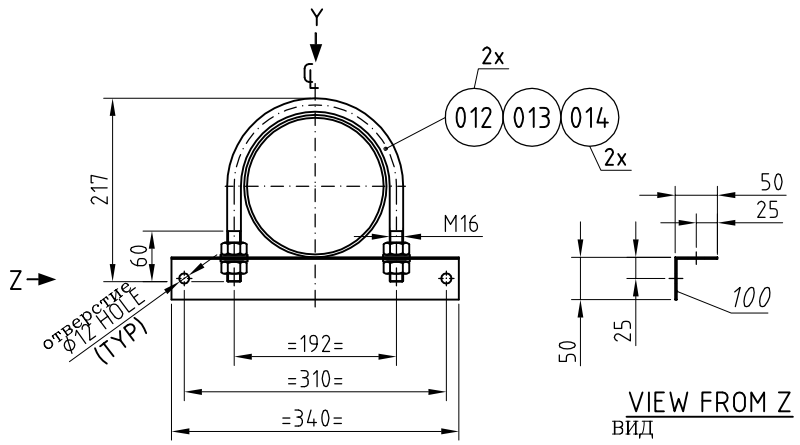


SECTION X-X
сечение
(M16 U-BOLT FOR 6" PIPE)
(У-образный болт для трубы)


VIEW FROM Z
вид

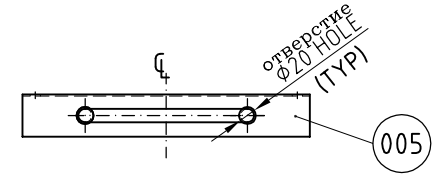

VIEW FROM Y
вид

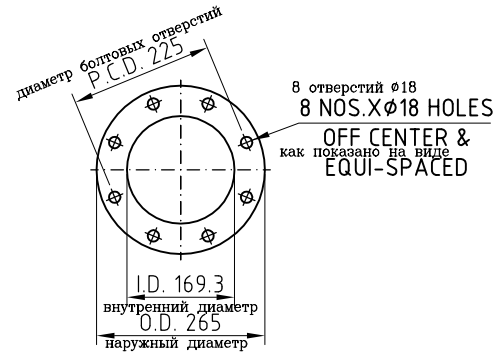

DN 150 FLANGE DETAIL
УЗЕЛ ФЛАНЦА

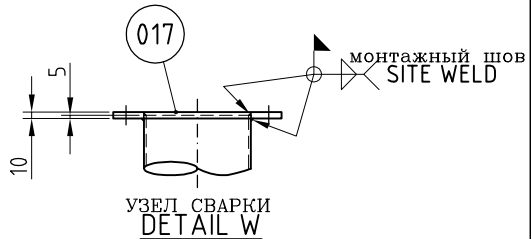

УЗЕЛ СВАРКИ
DETAIL W

PIPE TO FLANGE WELDING DETAIL
ТРУБЫ К ФЛАНЦУ (TYP)

NOTE:ПРИМЕЧАНИЕ:
1) Помеченные флажком привариваются при монтаже.
1) MARK THUS ⚑ TO BE WELDED AT SITE.

TYP - обычно используемый размер

ПРИМЕЧАНИЯ
Все узлы должны проходить через люк с внутр. диам. 570 мм
Все детали проверяются ультразвуком
Сборочные узлы проверяются после изготовления
обработка поверхности:
☐ без обработки ☒ только травлено
☐ протравлено ☐ нейтрализовано

GENERAL NOTES

All parts shall pass through man holes: 570 I.D.
All components are marked by SULZER.
The assembled part is checked after manufact.

surface treatment:
☐ without ☒ welding joints only
☐ pickled ☐ degreased

shop data files:
1000089805

Drawing-state: стадия
CERTIFIED FINAL

Изм.	Описание	Выполнил	Дата	Проверил	Дата	Утвердил	Дата
00	Original Issue	PATILDA	08.02.2011	PURANKMA	08.02.2011	GORECH	08.02.2011
rev.	revision remarks	issued by	date	checked	date	approved	date

SAP# 2139334.06.00105005 C | проект Project: 2139334.06 CACNEFT | формат A2 | масштаб scale: NTS
Sec-ID: 8600 диаметр колонны | заказчик Customer: SALAVATNEFTEORGSINTHEZ JSC | customer-P.O.: 2139334.06
Col-No./Tag: 001 K-300 VACUUM T | установка Service/Unit: | customer-dwg.:
Bed: 4 | AA | фирма Plant/Area: | End user:

SULZER

Downpipes -ID 8600mm
СЛИВНЫЕ ТРУБЫ

drawing-no.: номер чертежа
2139334-001-039 -1/3

This document is entrusted to the recipient personally. The copyright remains with SULZER CHEMTECH. Recipients must obtain written authority of the said company before wholly or partly use or duplicating the contents or disclosing same to others. All rights reserved.

1000089804-DRW