


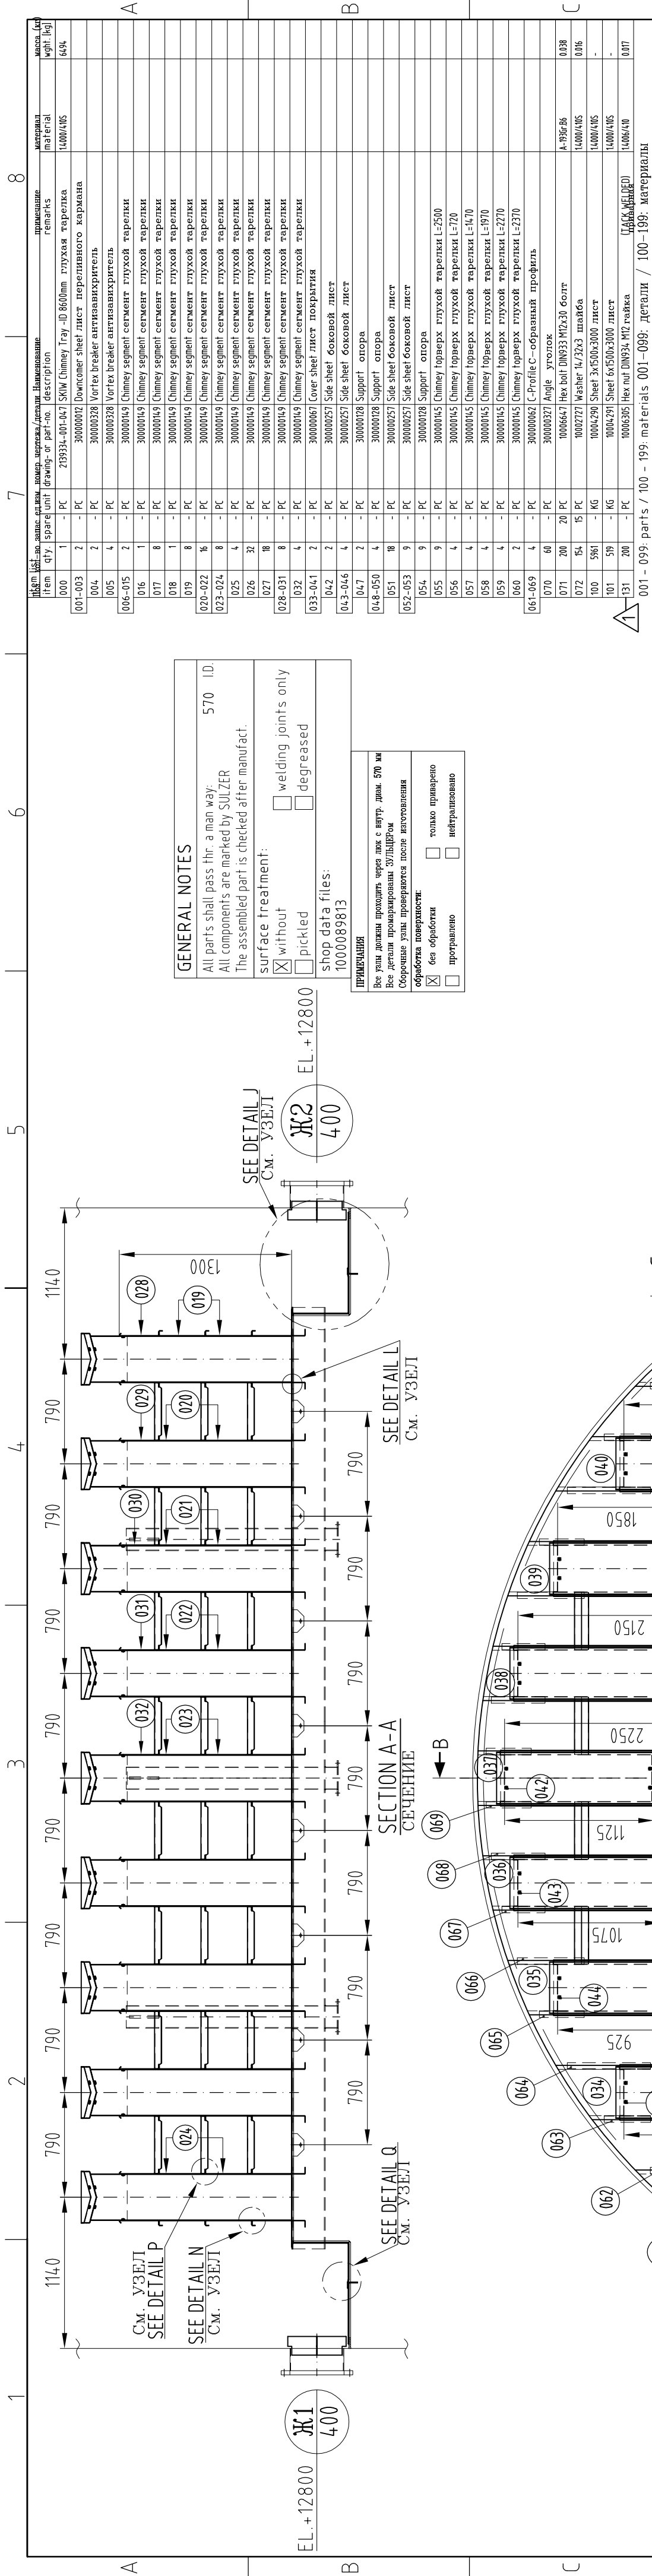

NOTES: Примечание:

1) NO. 8P SET REQUIRED: 1

2) NO. 8P SET REQUIRED: 1

3) * MARKED DIMENSIONS HAVE TO BE ADAPTED ON SITE. TO SUIT EXISTING NOZZLE.

4) * OPEN AREA=30.0%

5) CHIMNEY TRAY SHALL BE WELDED AFTER WELDING WORK.

