




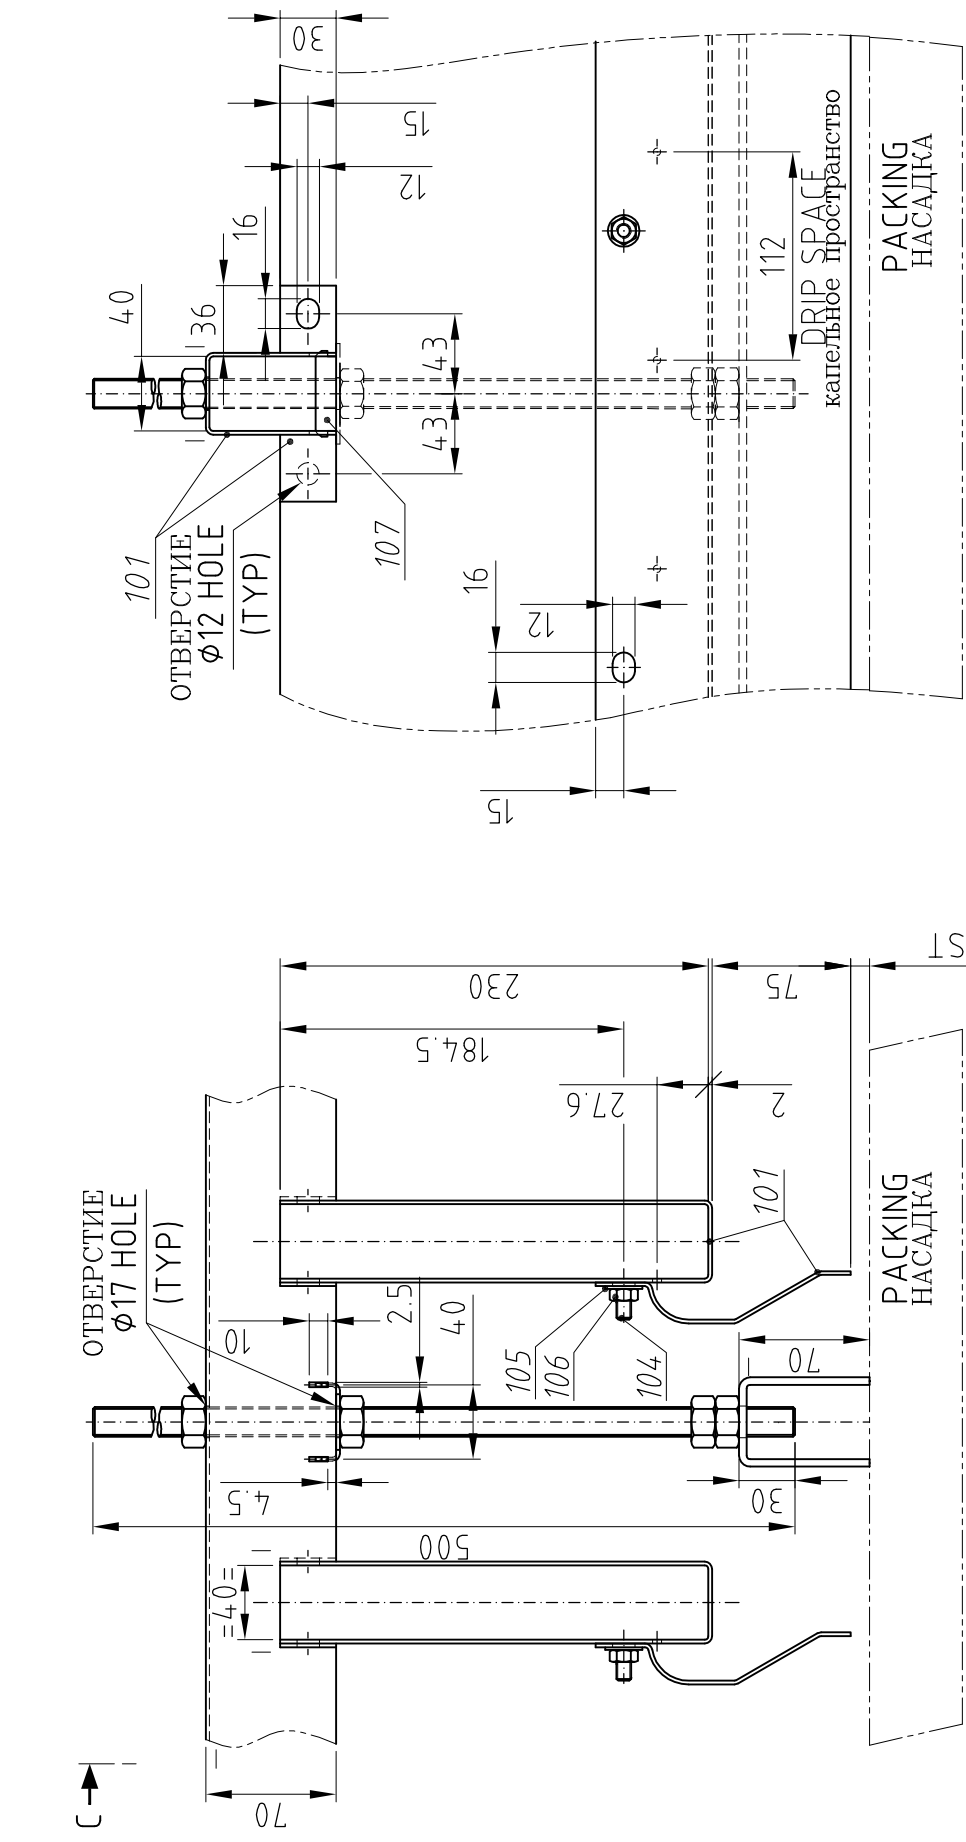

SECTION B-B
СЕЧЕНИЕ

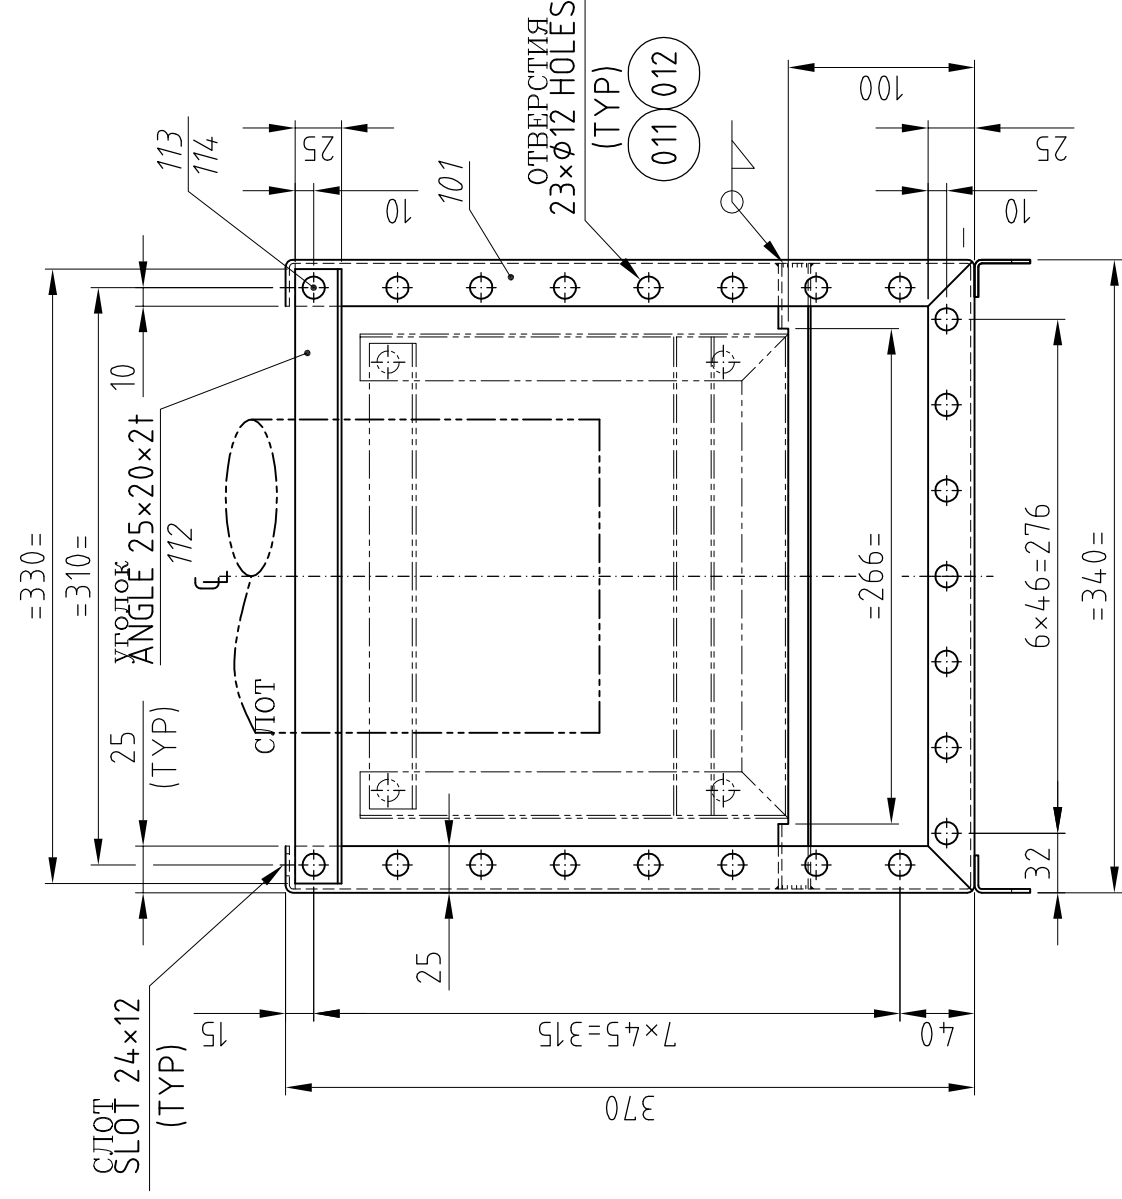


SECTION D-D
СЕЧЕНИЕ

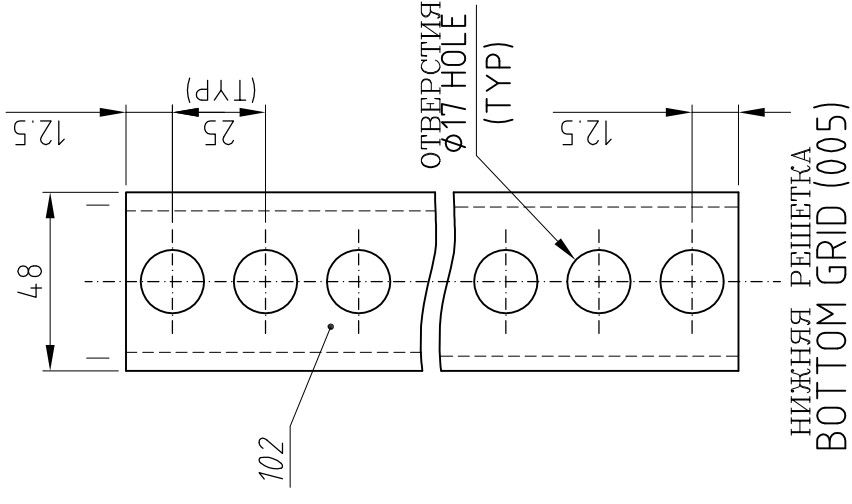


НИЖНЯЯ РЕШЕТКА
BOTTOM GRID (005)


BEGINNING AND END OF PROFILE FOR LOCATING GRID SYSTEM НАЧАЛО И КОНЕЦ ПРОФИЛЯ ДЛЯ СИСТЕМЫ РЕШЕТКИ

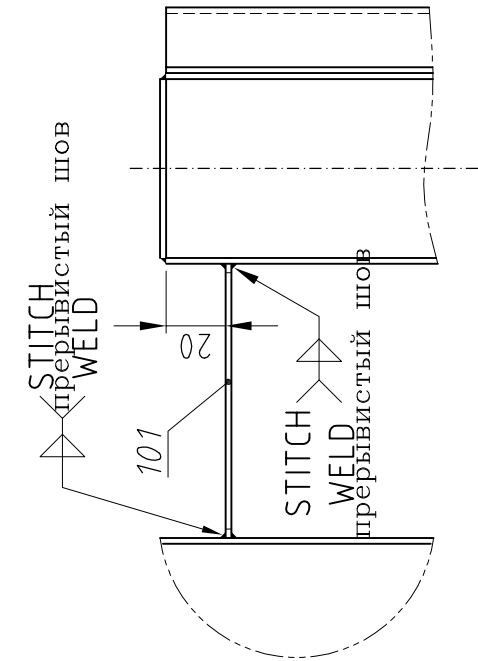


DETAIL G
УЗЕЛ

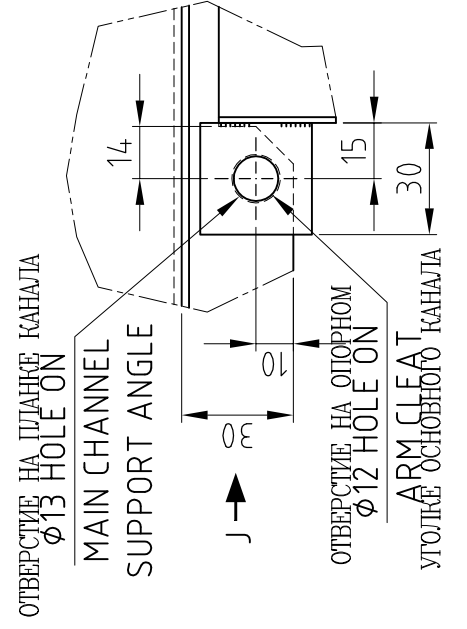


DETAIL H

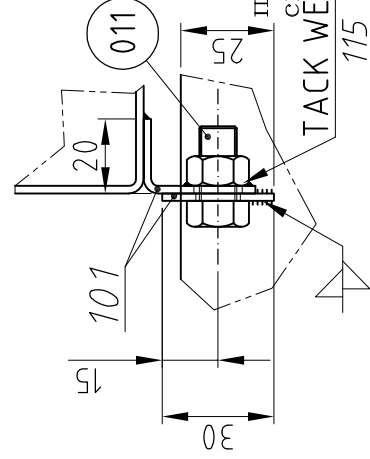


VIEW FROM J

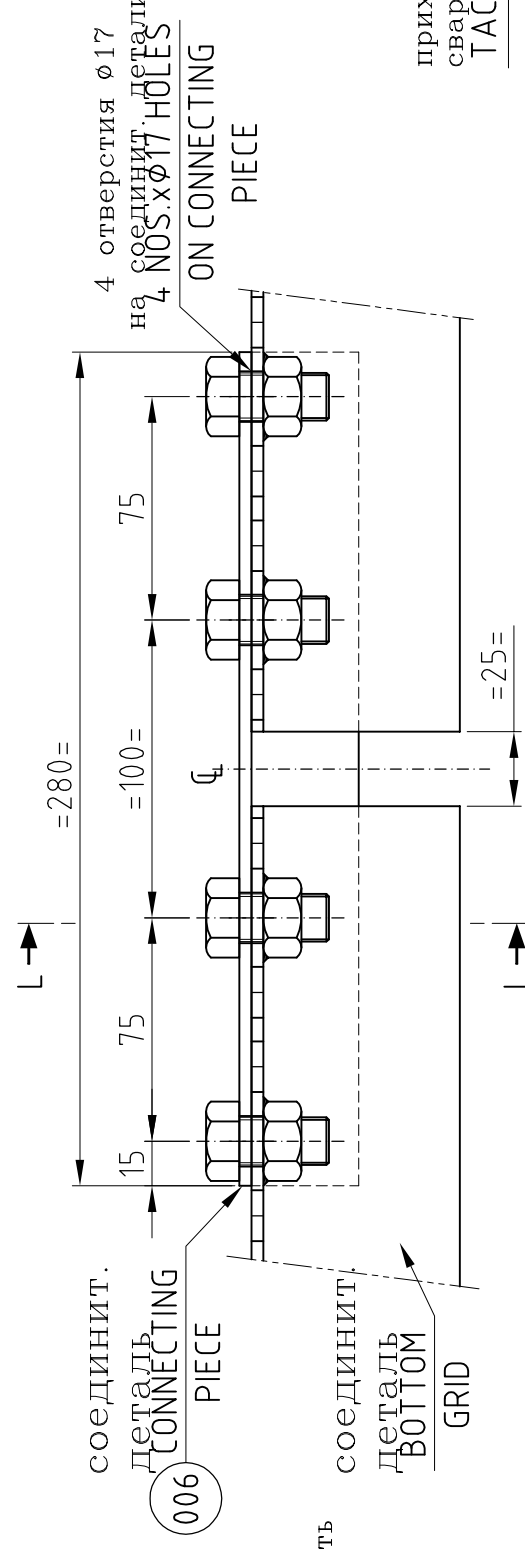


SECTION K-K
СЧЕТНИК

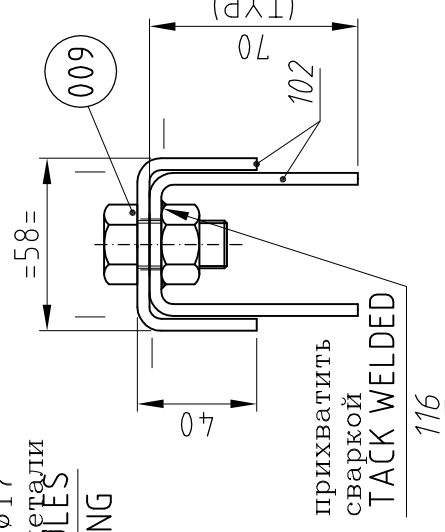

SECTION L-L
СЕЧЕНИЕ

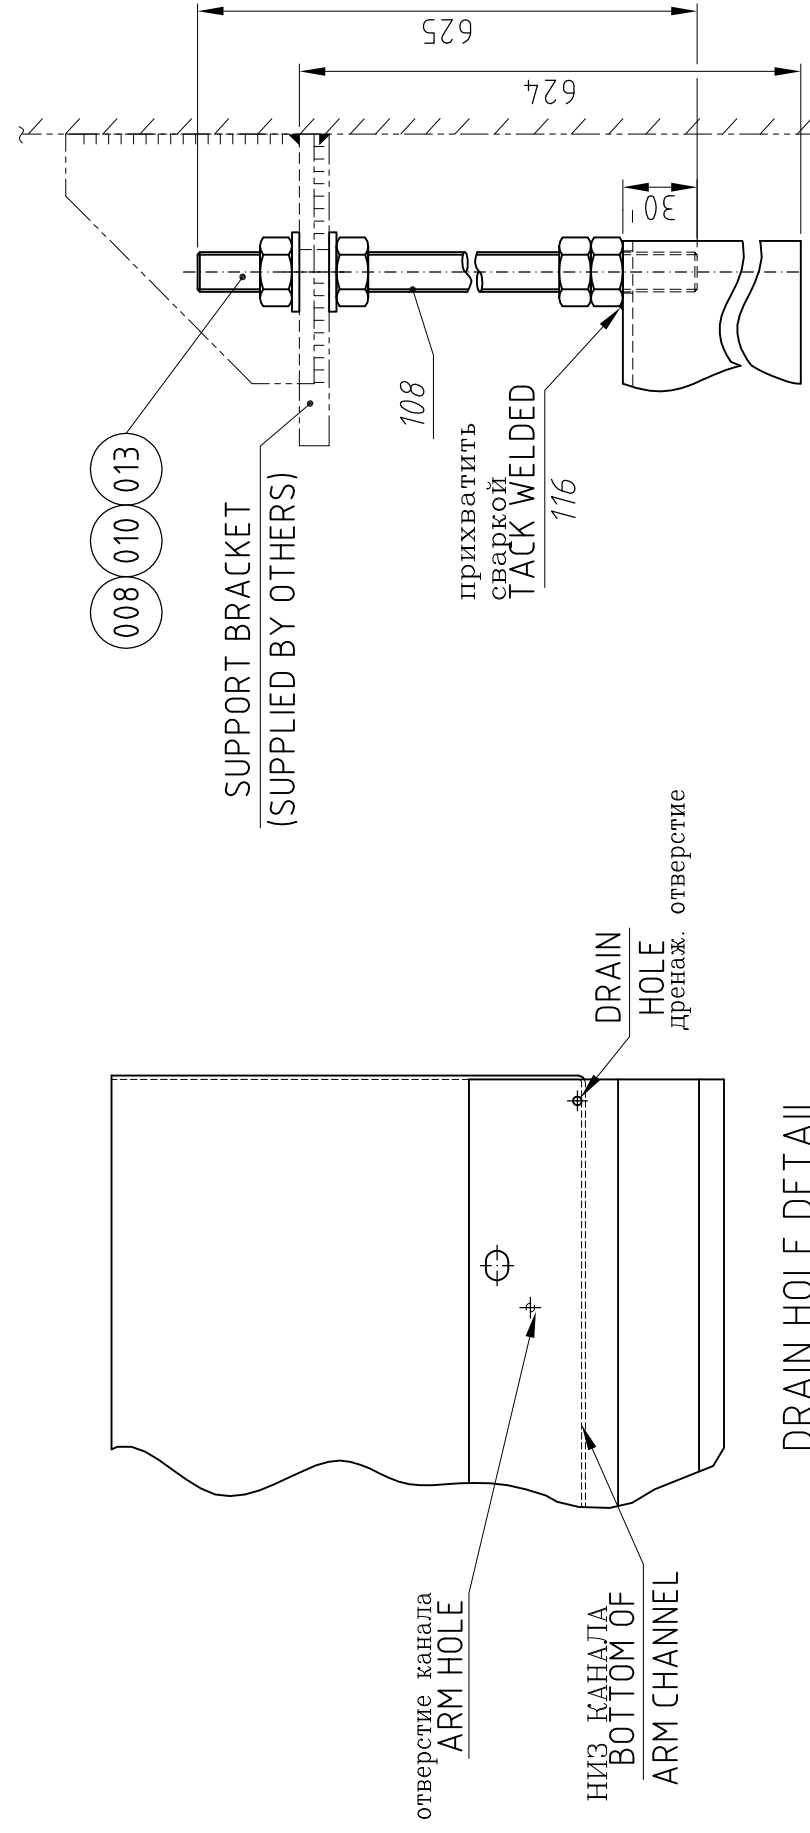

DRAIN HOLE DETAIL

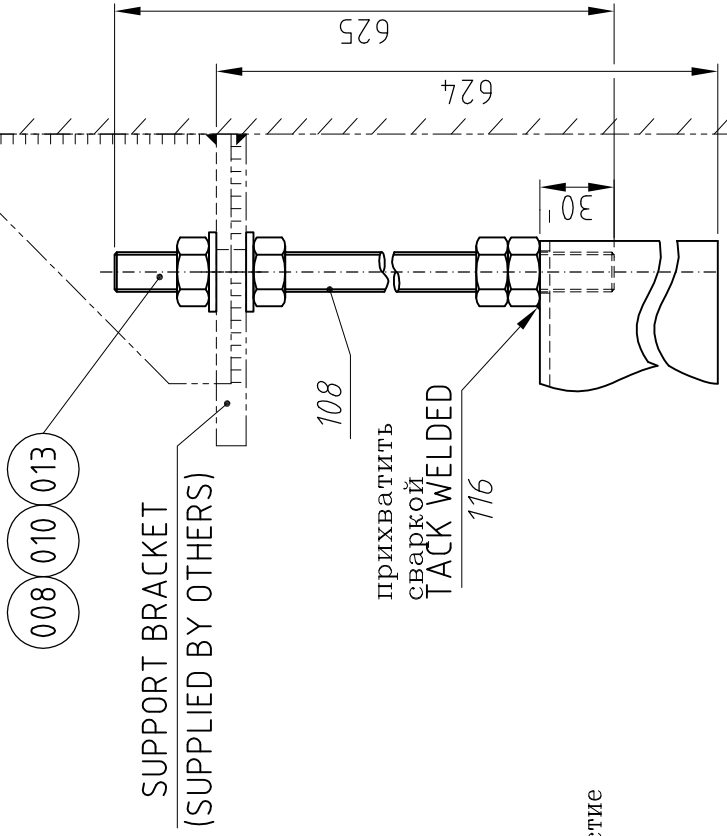

SECTION M-M

Изм.	Описание	Выполнен	Дата	Проверен	Дата	Утвержден
00	Original issue	PATLIDA	08.02.2011	PIRAMKA	08.02.2011	GORECH 08.02.2011
	rev. revision remarks	C	Project - 219337406	checked date approved date	date	status NTS
SAP#	2193334-06.00107001					
Sec-ID:	8600	document	Customer: SALAVINFEJGDSINHZEJ JSC		customer-P.O.: Z19334-06	
Contract Tag:	001 K-300 VACUUM T Service/Unit:				End user:	
Bef's	AA Plant/Area:					

VEP Distributor - ID 8600mm	
------------------------------------	--

SULZER	РАСПРЕДЕЛИТЕЛЬ	2139334-001-059-2/2
This document is entrusted to the recipient personally. The copyright remains with SULZER CHEMTECH. Recipients must obtain written		

Drawing-state: стадия
CERTIFIED FINAL