item list

item	qty.	spare	unit	drawing- or part-no.	description	remarks	material	wght. [kg]
000	1	-	PC	2139334-001-073	Downpipes -ID 8600mm	сливные трубы	304L	282
001-004	2	-	PC	300000210	Pipe with flange	труба с фланцем		
005	4	-	PC	300000029	Suspension	распорка		
006	76	-	PC	10006646	Hex bolt DIN933 M16x60	болт	A-193Gr.B8	0.114
007	76	-	PC	10006683	Hex nut DIN934 M16	гайка	A-194Gr.8	0.033
008	12	-	PC	10002714	Washer 17/32x3	шайба	1.4307/304L	0.014
100	10.5	-	KG	10004455	Sheet 6x1500x3000	лист	1.4307/304L	-
101	14	-	PC	10002901	Flange DN150x10	фланец	1.4307/304L	2.4
102	16.1	-	M	10005222	Pipe welded 6"x10S	приварная труба	1.4307/304L	14

001 - 099: parts / 100 - 199: materials 001–099: части / 100–199: материалы

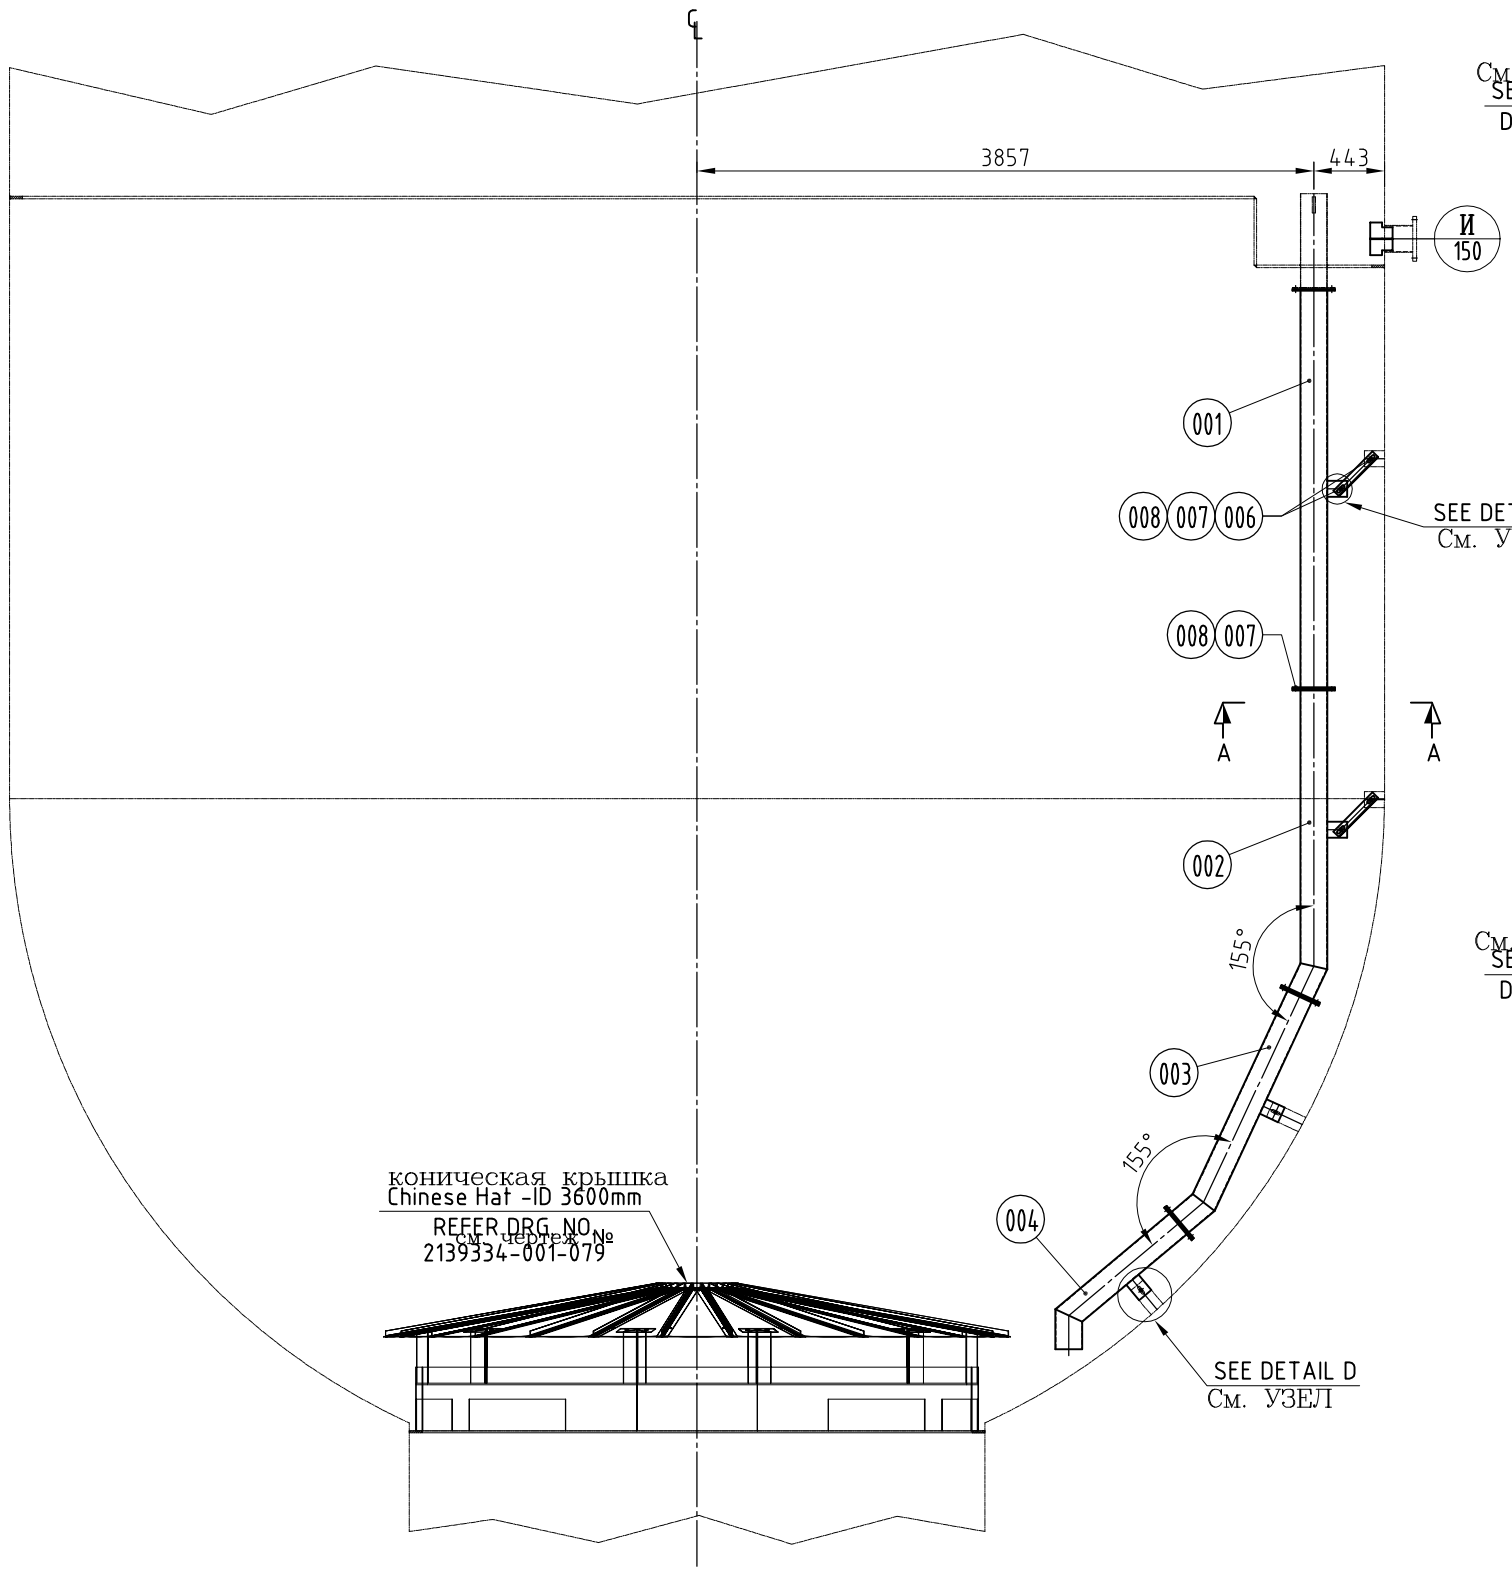

ELEVATION
общий вид

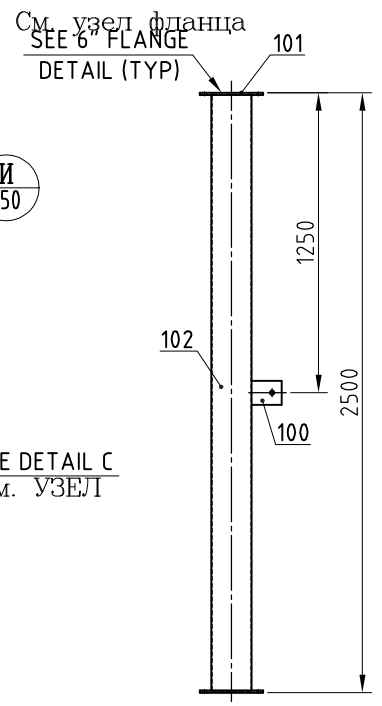

DETAIL OF ITEM 001
УЗЕЛ Поз.001

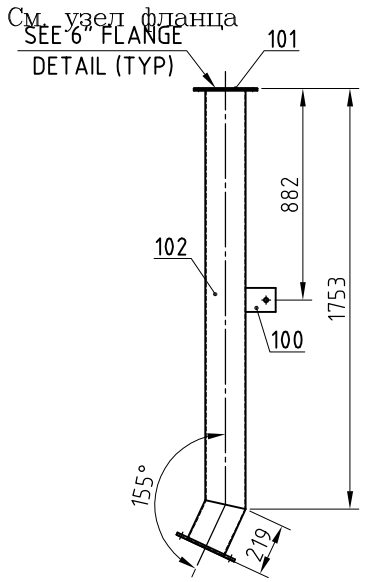

DETAIL OF ITEM 002
УЗЕЛ Поз.002

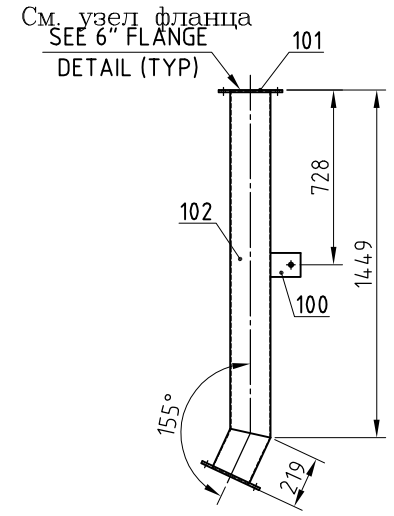

DETAIL OF ITEM 003
УЗЕЛ Поз.003

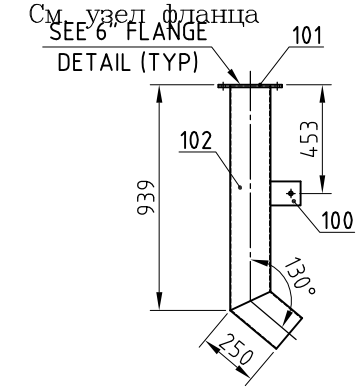

DETAIL OF ITEM 004
УЗЕЛ Поз.004

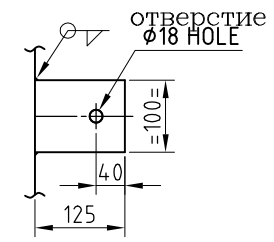

DETAIL C
УЗЕЛ

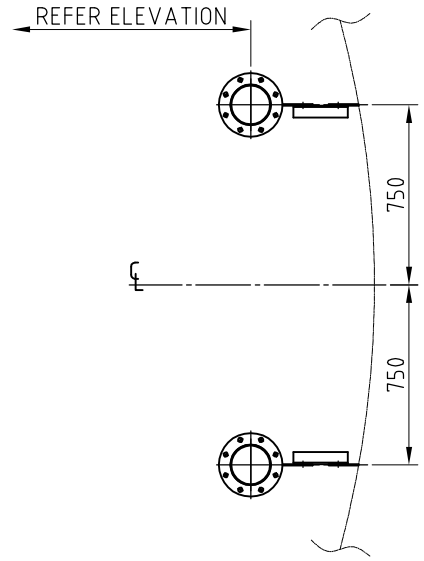

SECTION A-A
СЕЧЕНИЕ

DN 150 FLANGE DETAIL
УЗЕЛ ФЛАНЦА

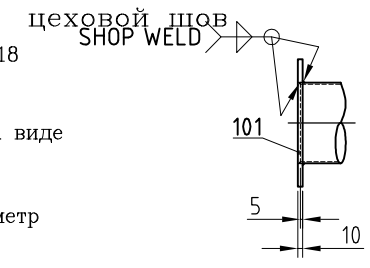

PIPE TO FLANGE WELDING DETAIL
УЗЕЛ СВАРКИ ТРУБЫ К ФЛАНЦУ

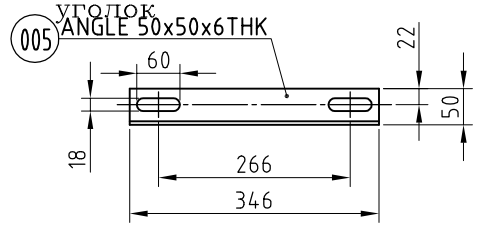

DETAIL OF SUSPENSION BAR
УЗЕЛ РАСПОРНОЙ БАЛКИ

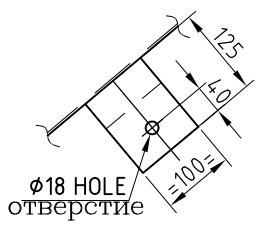

DETAIL D УЗЕЛ

Изм.	Описание	Выполнил	Дата	Проверил	Дата	Утвердил	Дата
00	Original issue	PATILDA	14.02.2011	PURANIKMA	14.02.2011	HANDESH	14.02.2011
rev.	revision remarks	issued by	date	checked	date	approved	date

SAP# 2139334.06.00108005 C | проект Project: 2139334 CACNEFT | формат A3 | масштаб scale: NTS

Sec-ID: 8600 диаметр колонны | заказчик Customer: SALAVATNEFTEORGSINTHEZ JSC | customer-P.O.: 2139334.06

Col-No./Tag: 001 K-300 VACUUM | установка Service/Unit: | customer-dwg.:

секция Bed: 5 | AB завод Plant/Area: | End user:

SULZER

Downpipes -ID 8600mm
СЛИВНЫЕ ТРУБЫ

drawing-no.: номер чертежа
2139334-001-073-1/1

Drawing-state: стадия
CERTIFIED FINAL

This document is entrusted to the recipient personally. The copyright remains with SULZER CHEMTECH. Recipients must obtain written authority of the said company before wholly or partly use or duplicating the contents or disclosing same to others. All rights reserved.

1000089838-DRW