
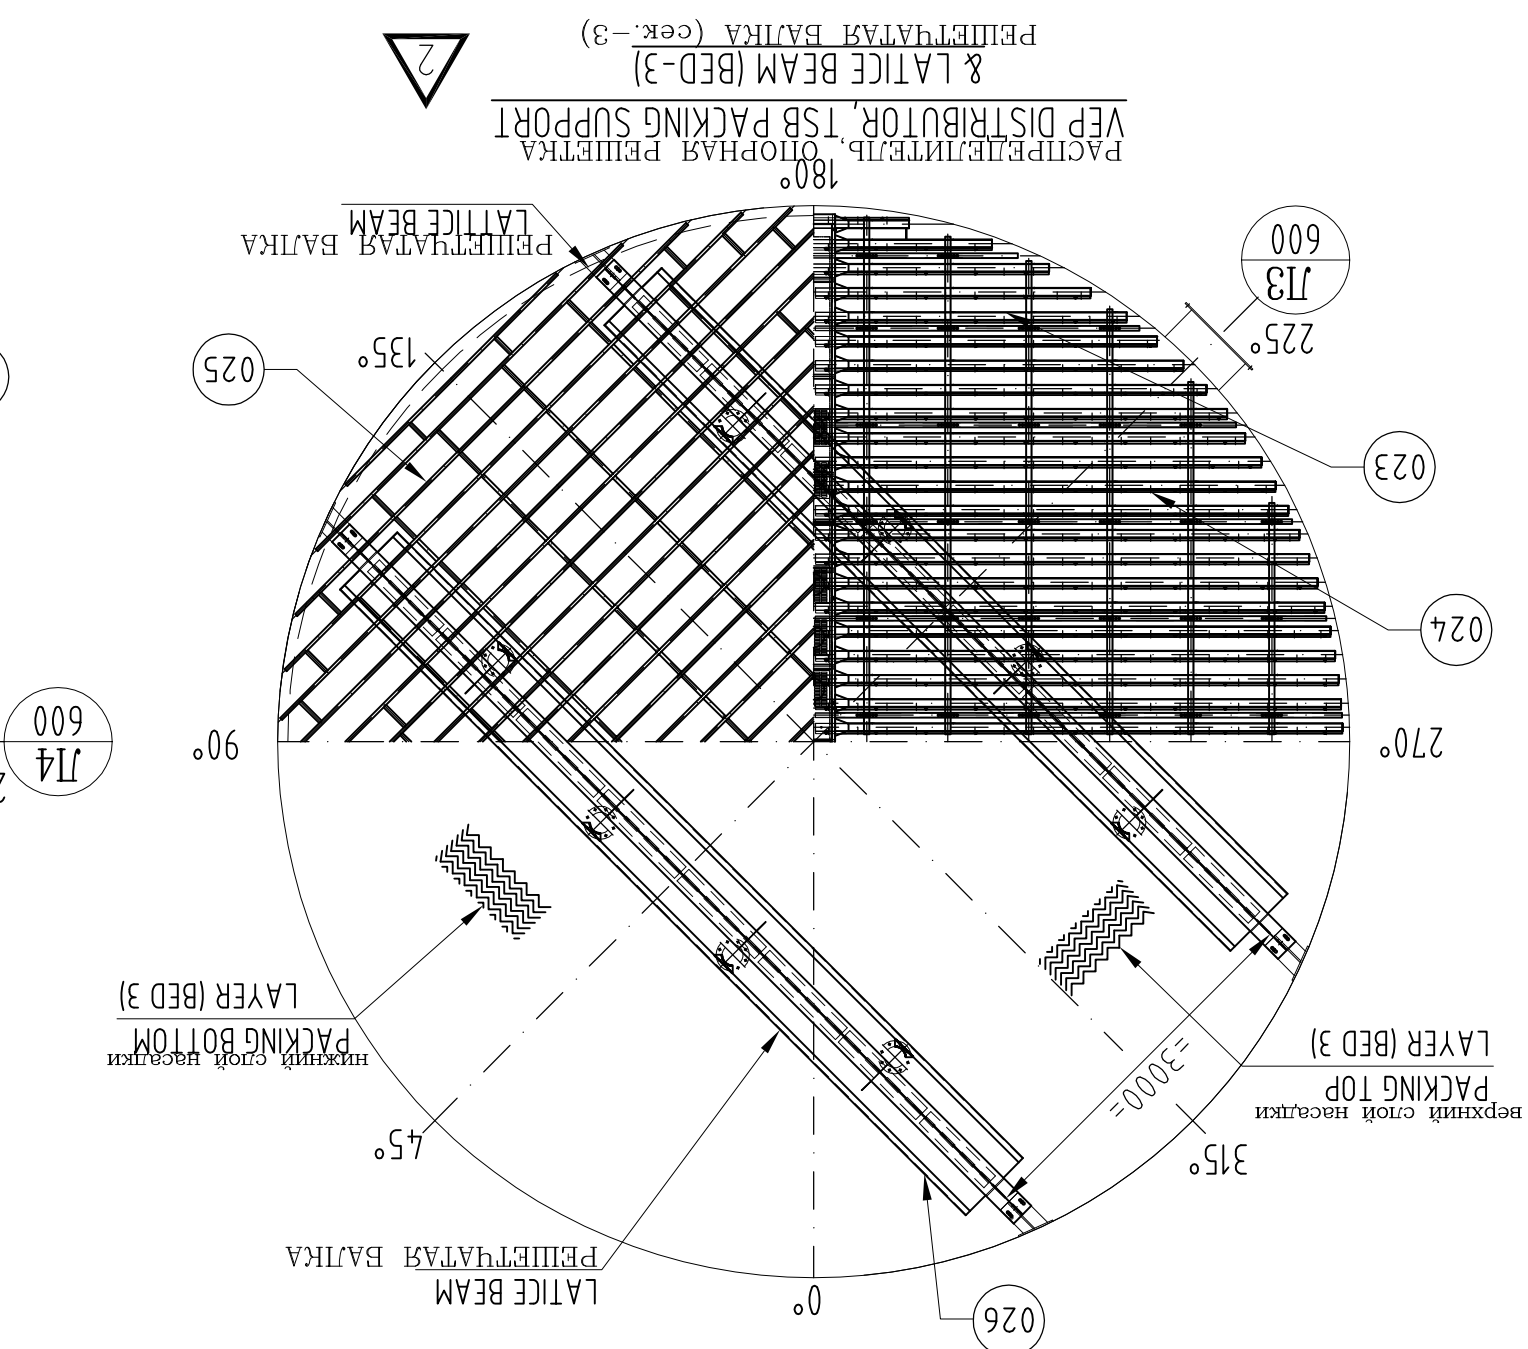
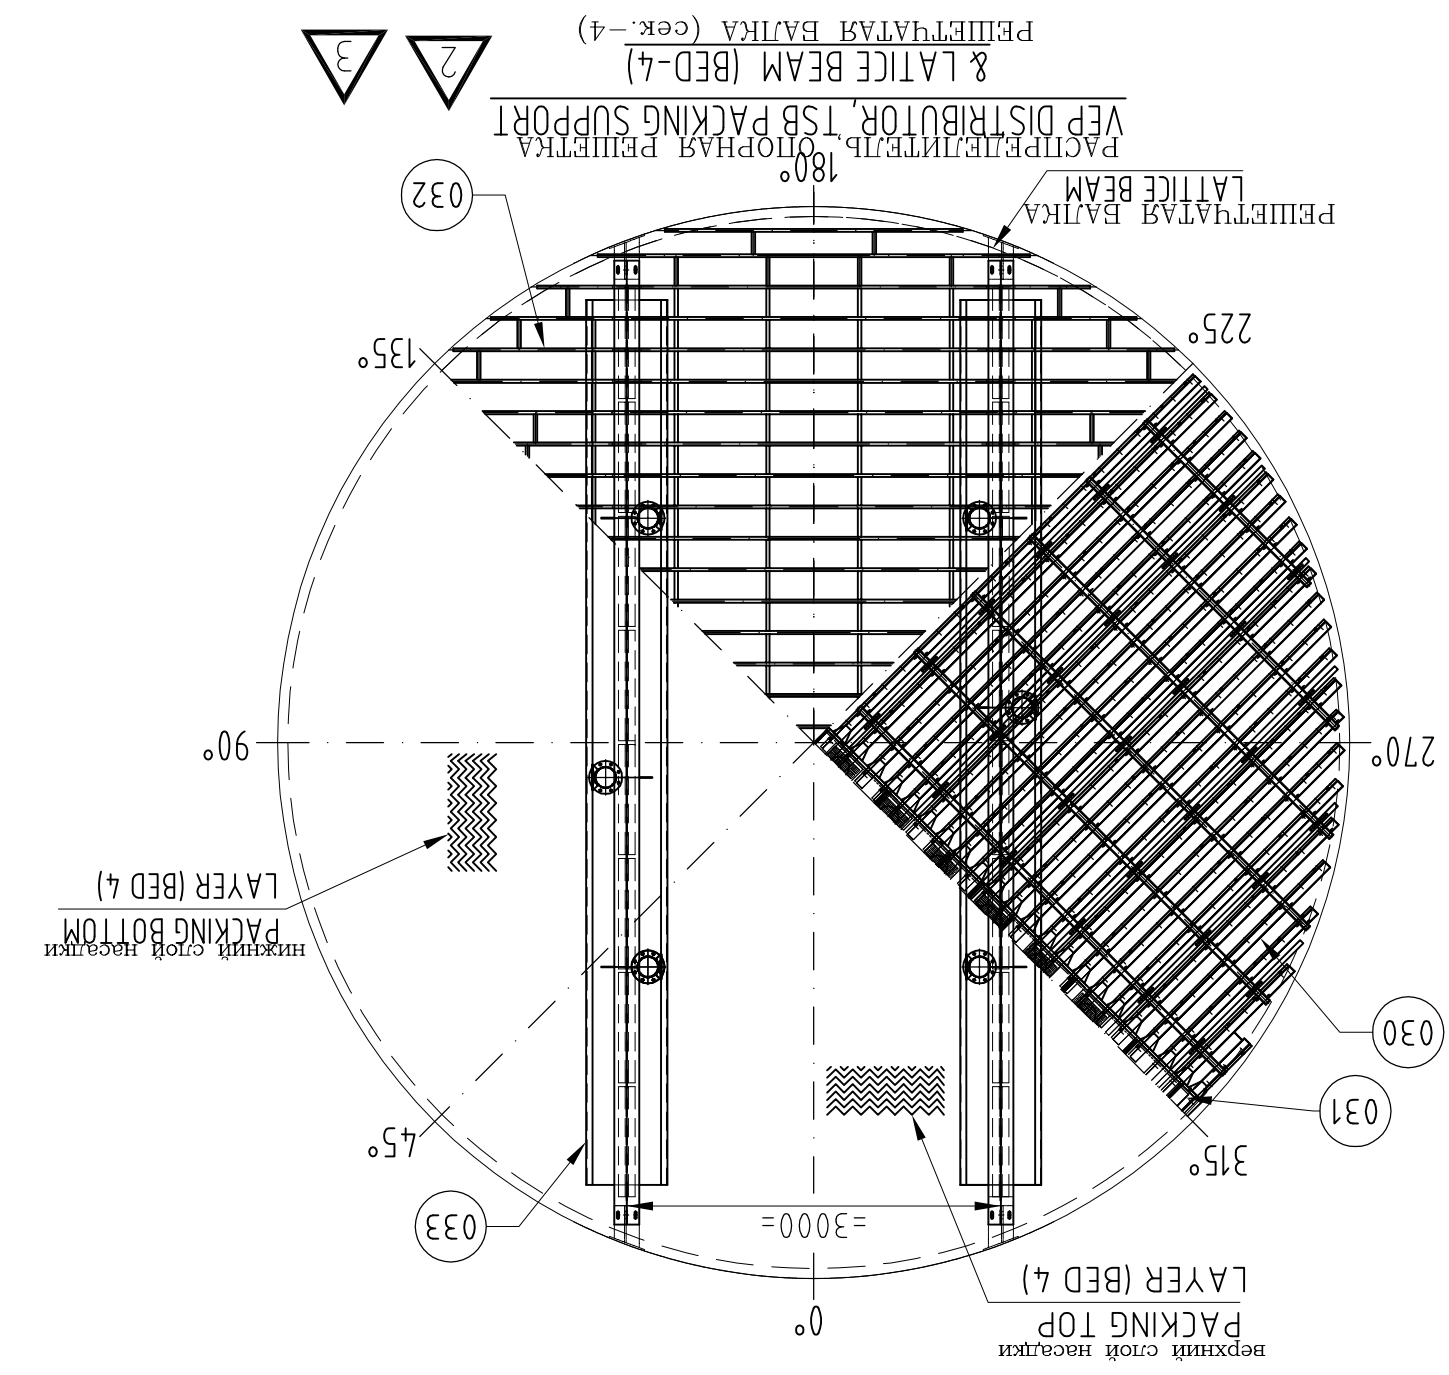
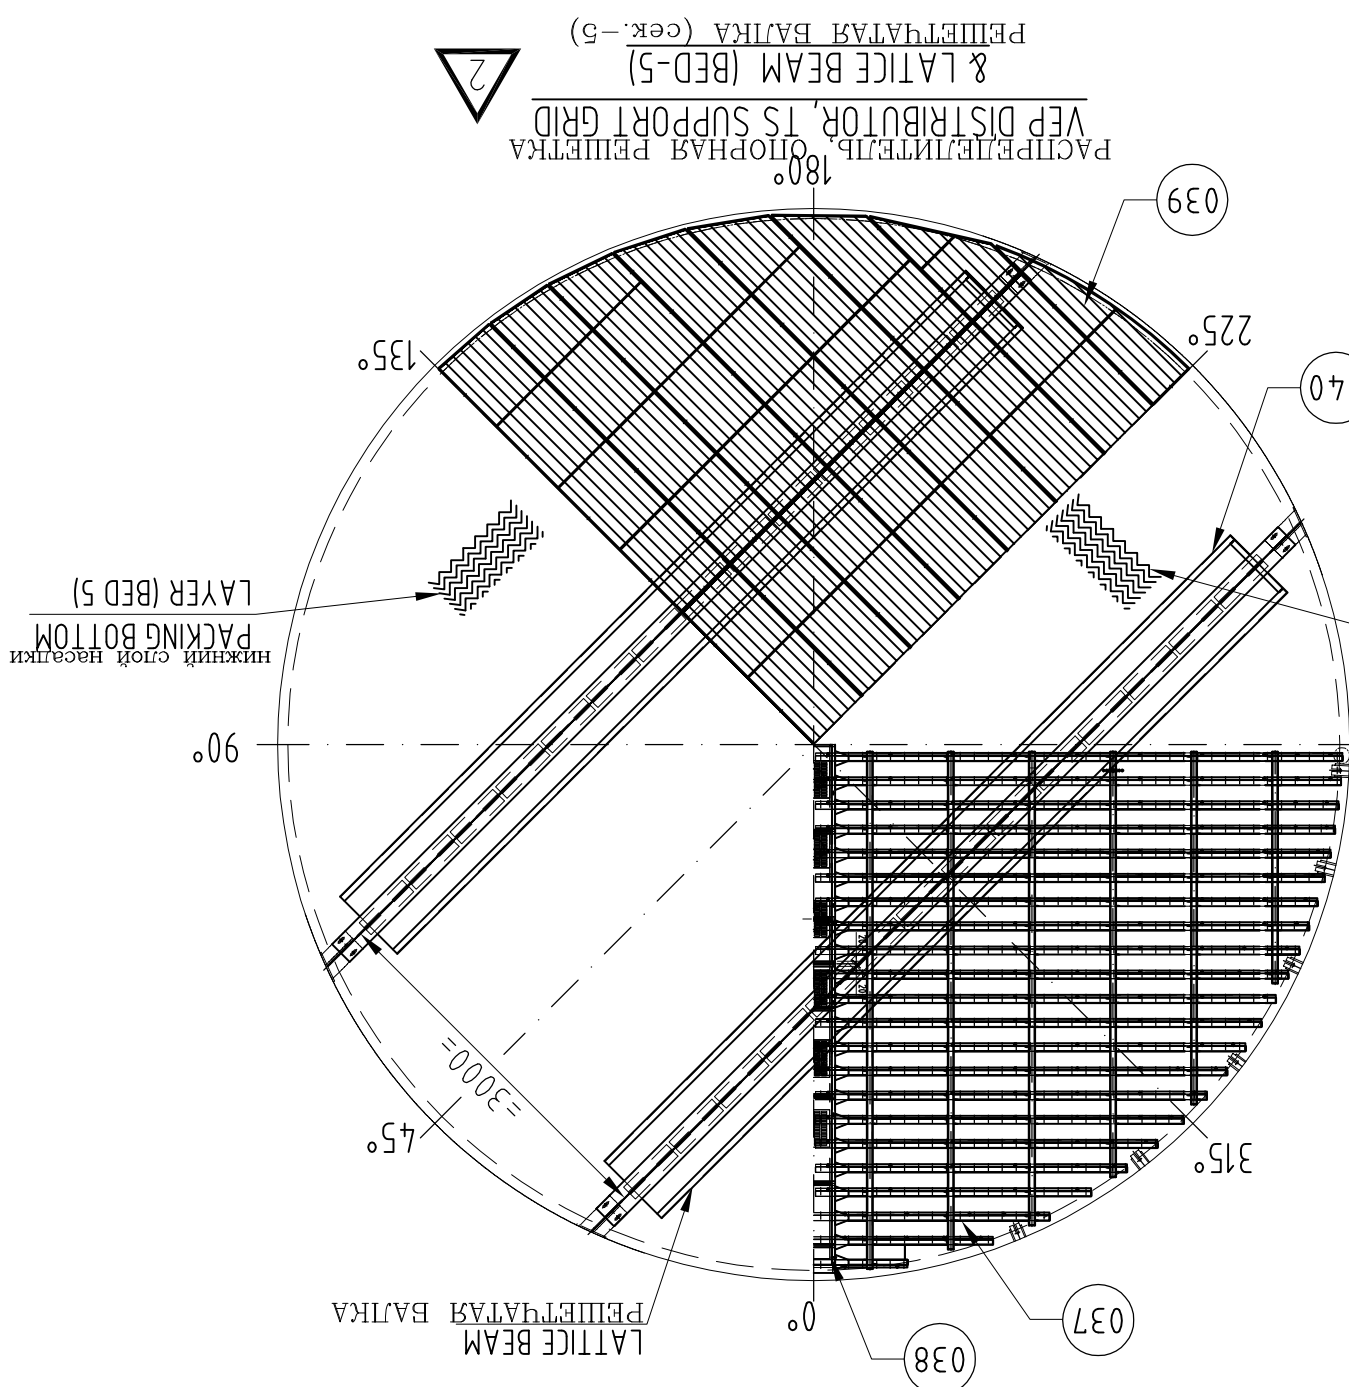
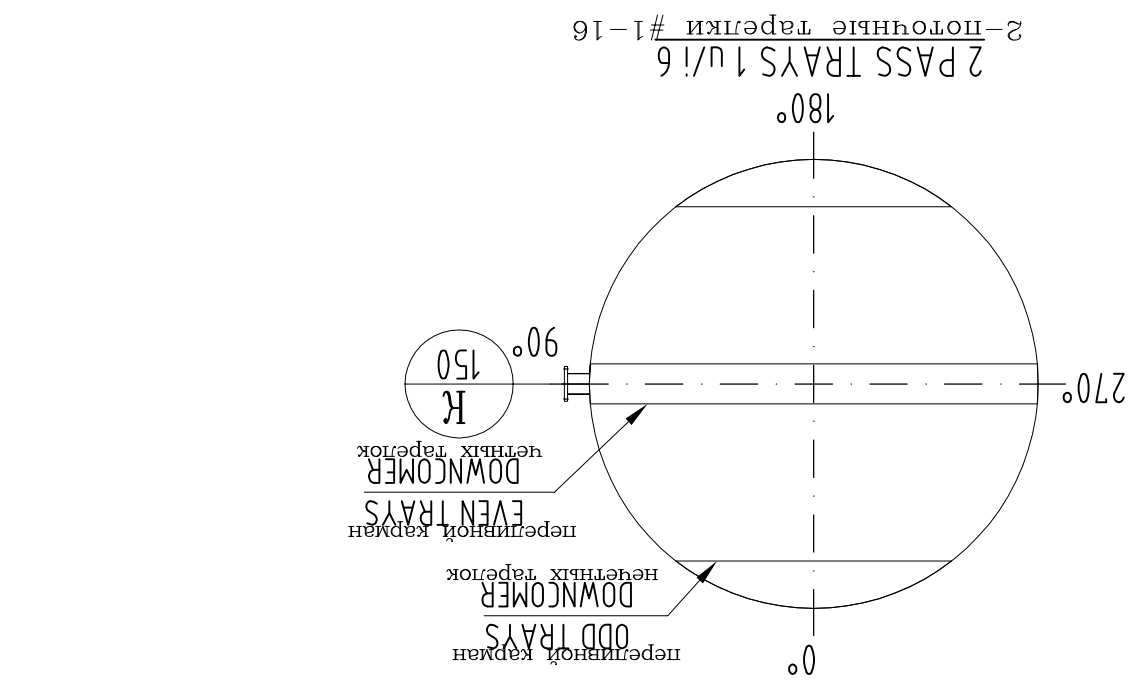
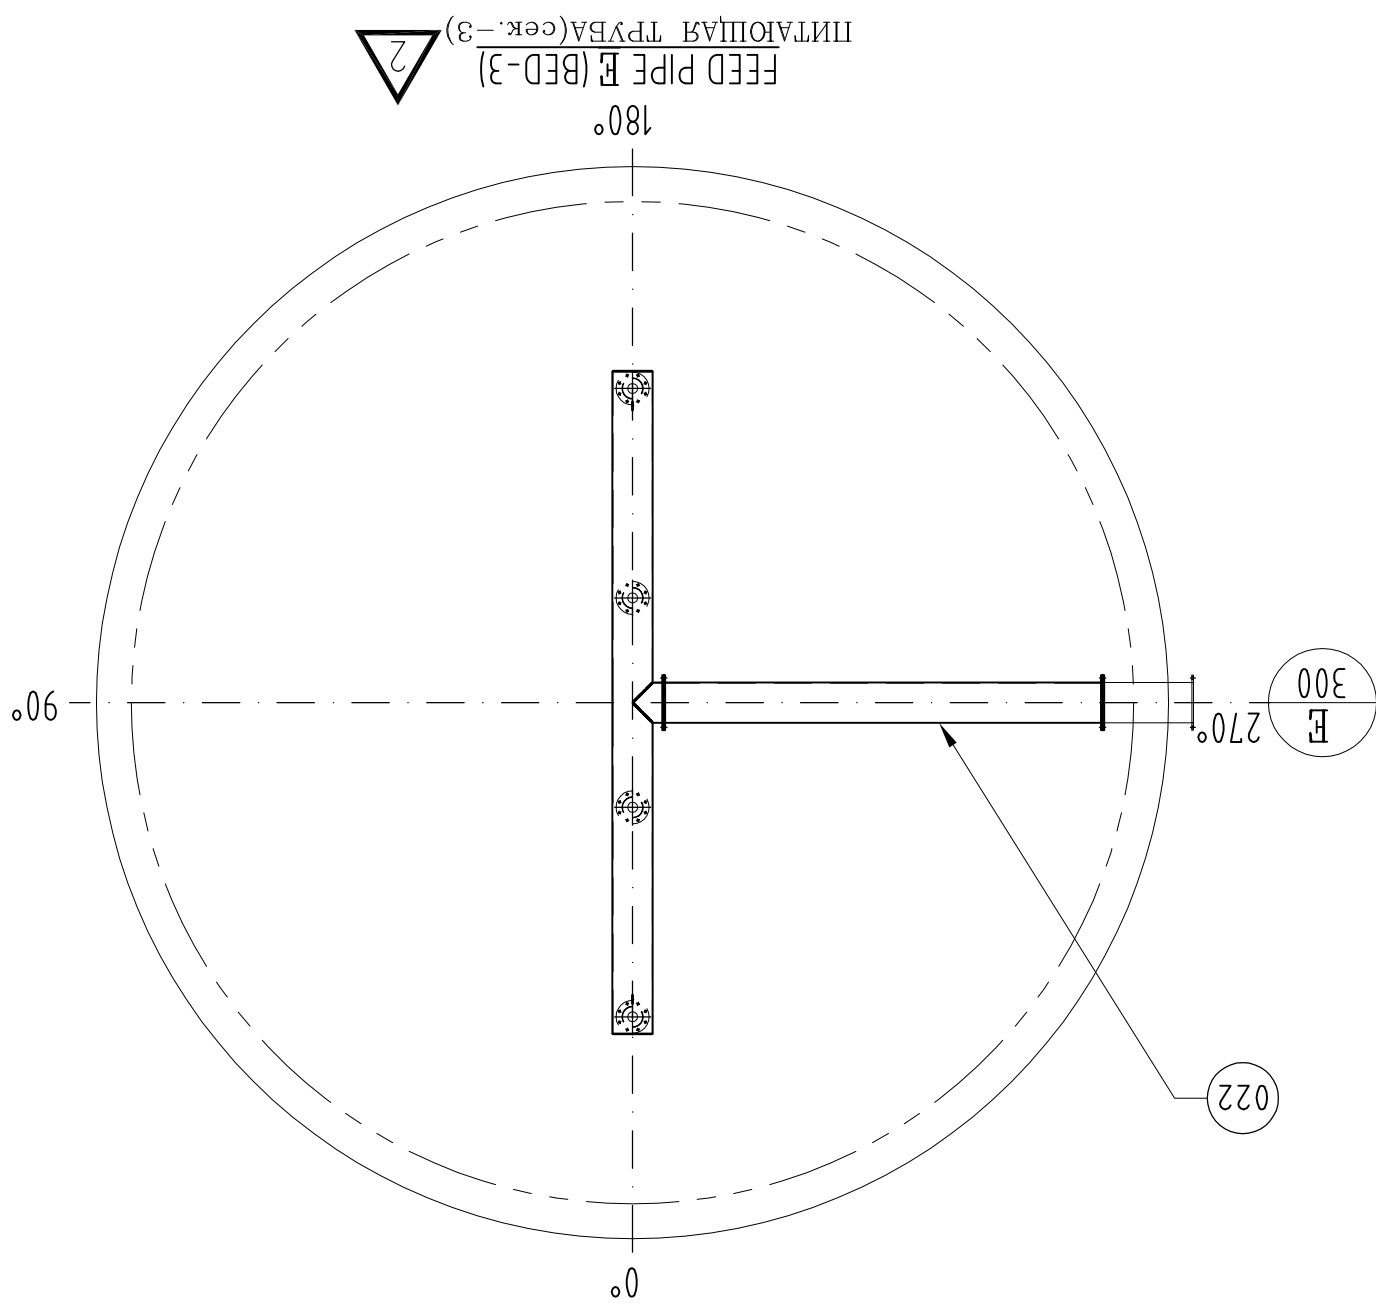
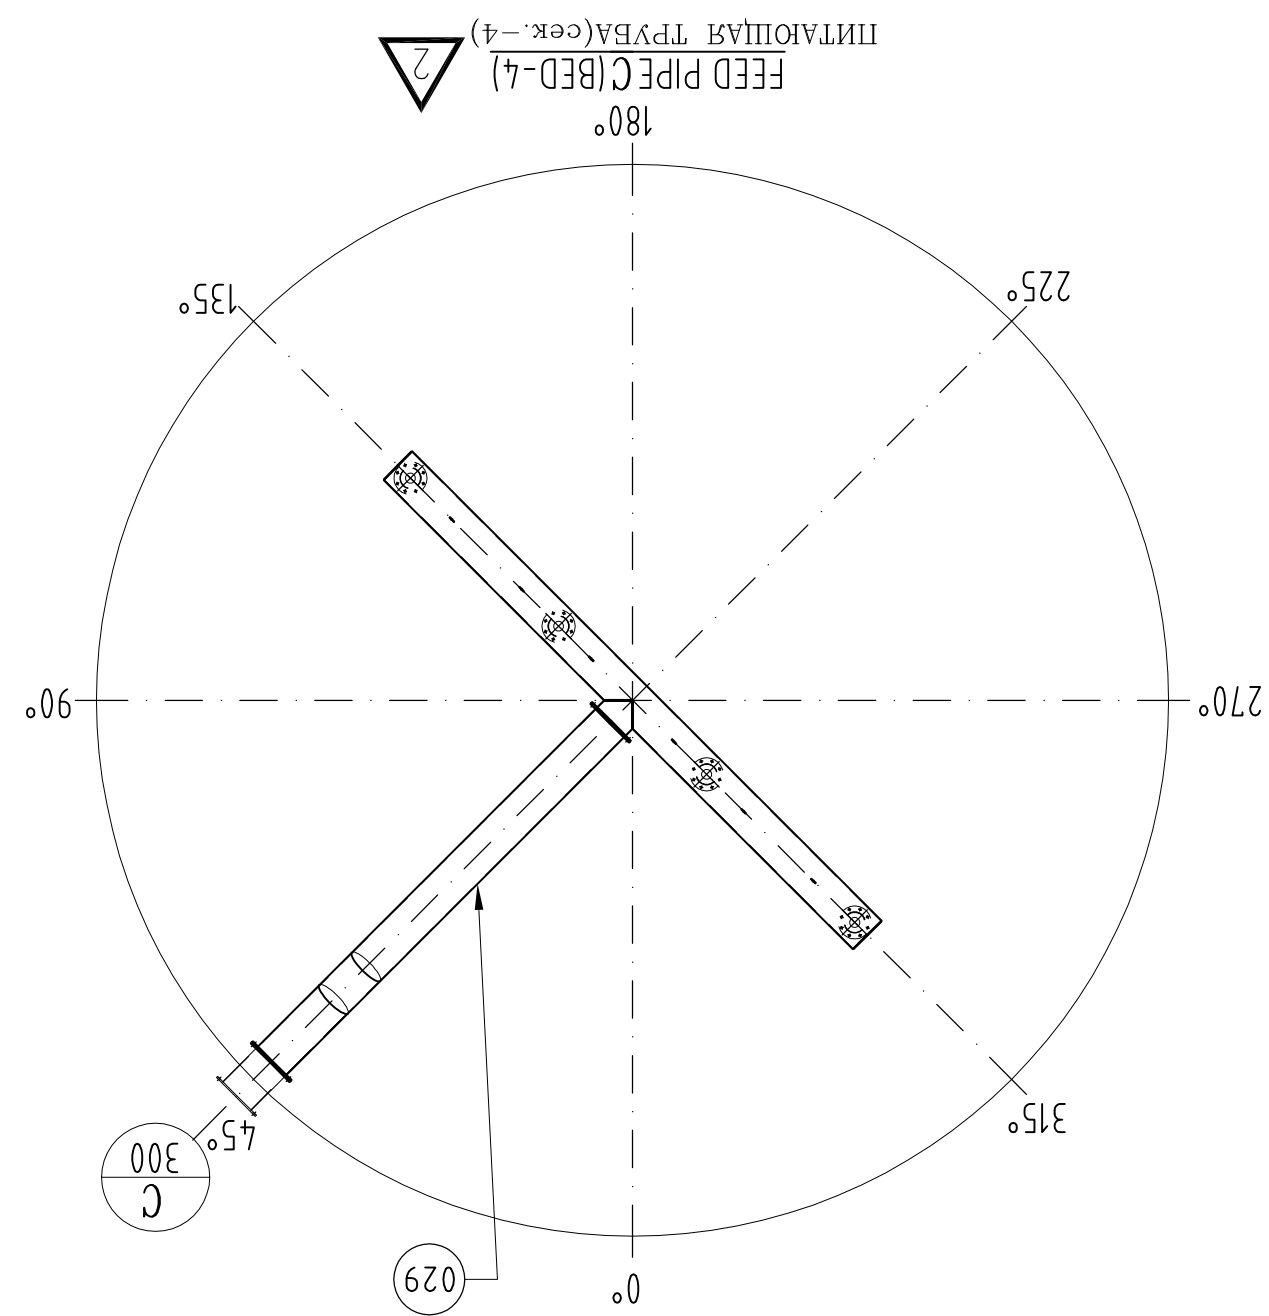
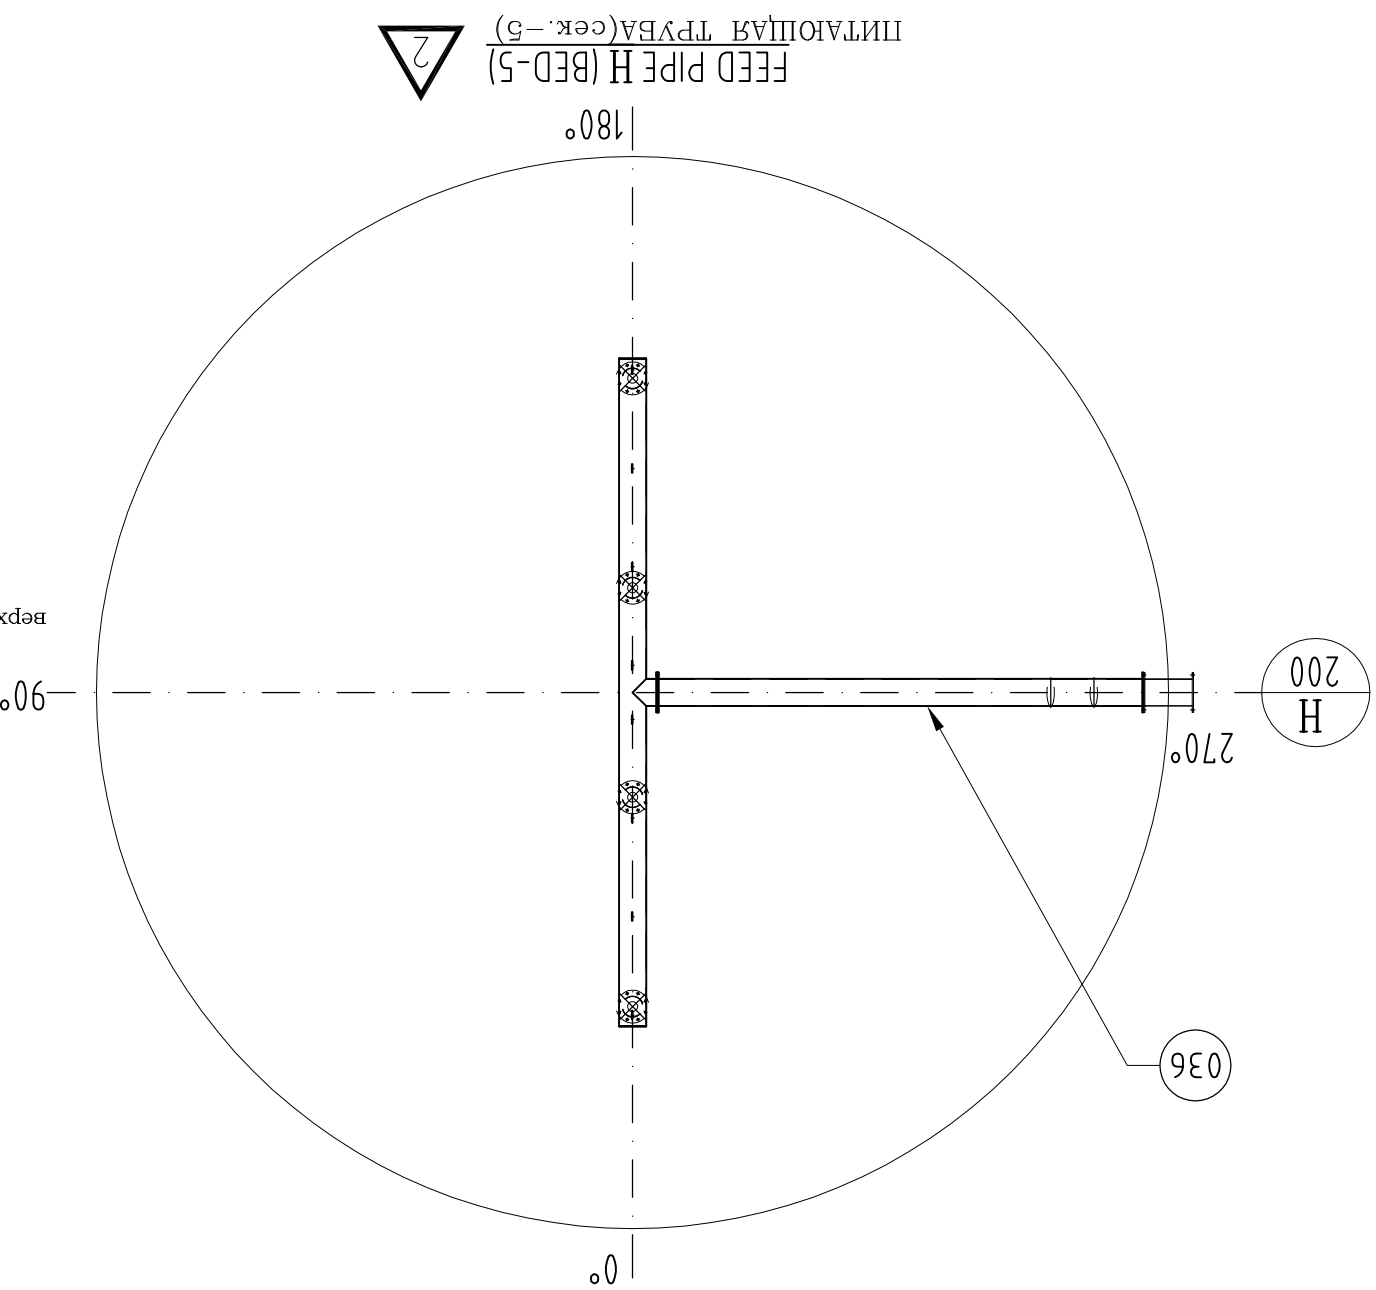


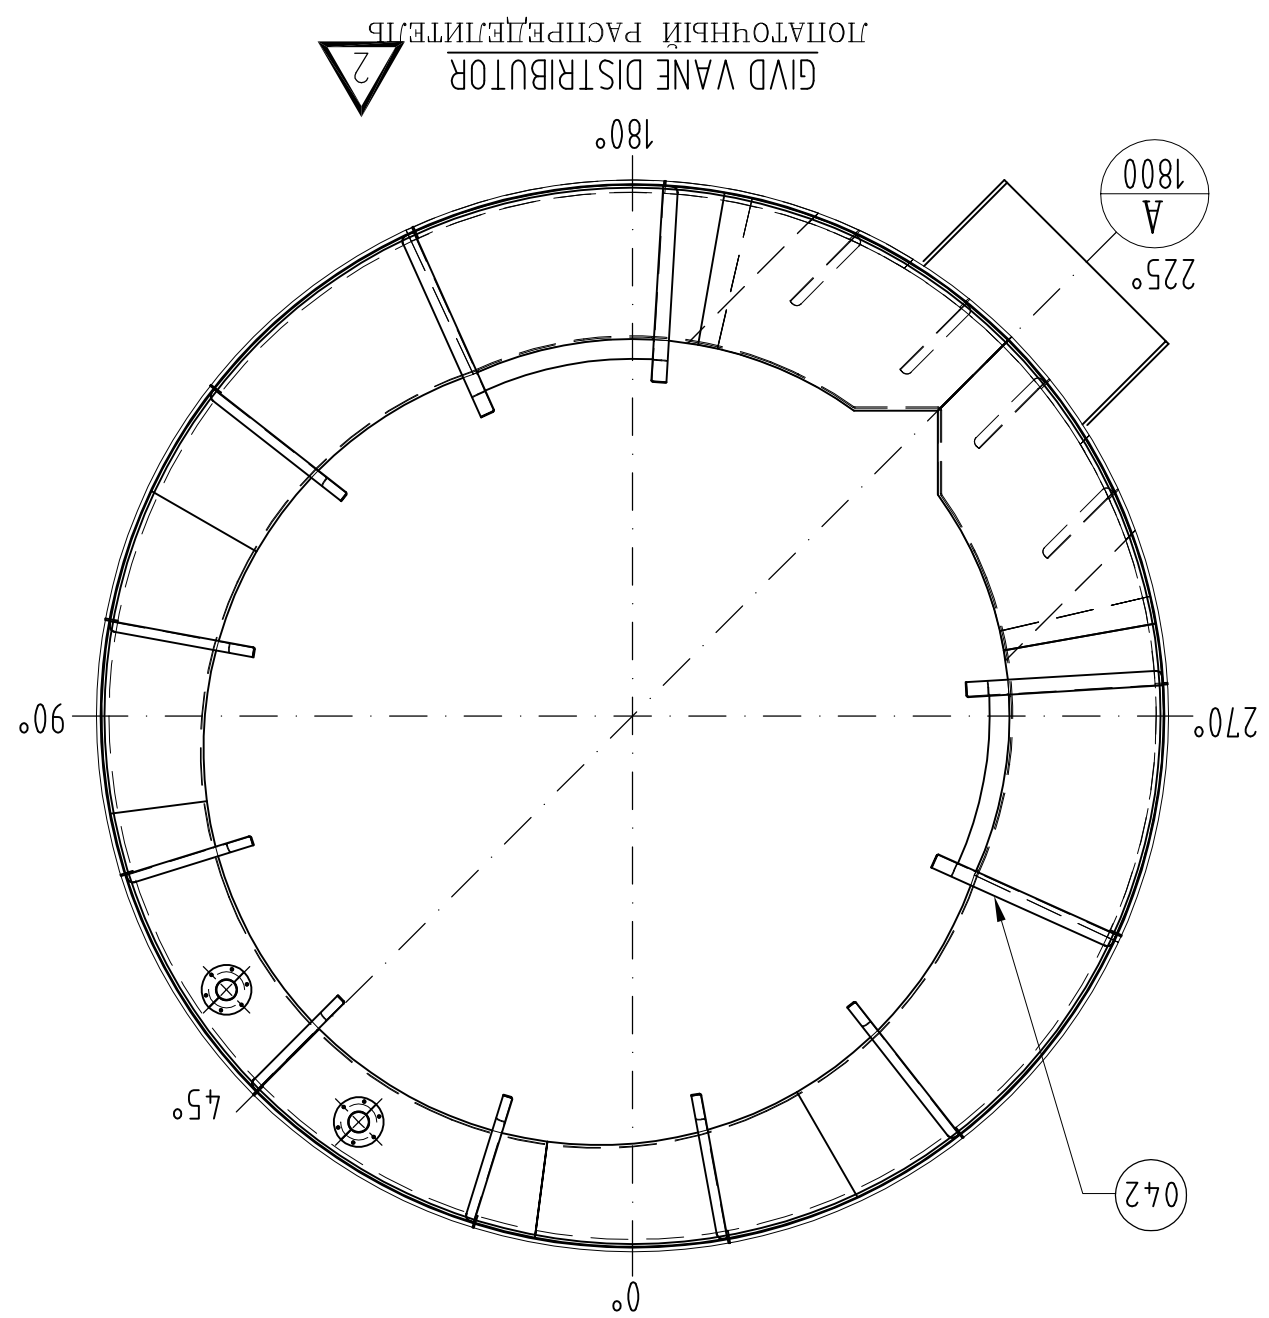

2-ПАСС ТРАЙС 1 u/1 6

РАСПРЕДЕЛИТЕЛЬ, 158 ПАККИНГ СУППОРТ
& ЛАТТИС БИМ (BED-5)

РАСПРЕДЕЛИТЕЛЬ, 158 ПАККИНГ СУППОРТ
& ЛАТТИС БИМ (BED-4)

РАСПРЕДЕЛИТЕЛЬ, 158 ПАККИНГ СУППОРТ
& ЛАТТИС БИМ (BED-3)

ГИД ВОДНОГО РАСПРЕДЕЛИТЕЛЯ

ПИТАЮЩАЯ ТРУБА (BED-5)

ПИТАЮЩАЯ ТРУБА (BED-4)

ПИТАЮЩАЯ ТРУБА (BED-3)

2-ПАСС ТРАЙС 1 u/1 6

РАСПРЕДЕЛИТЕЛЬ, 158 ПАККИНГ СУППОРТ
& ЛАТТИС БИМ (BED-5)

РАСПРЕДЕЛИТЕЛЬ, 158 ПАККИНГ СУППОРТ
& ЛАТТИС БИМ (BED-4)





РАСПРЕДЕЛИТЕЛЬ, 158 ПАККИНГ СУППОРТ
& ЛАТТИС БИМ (BED-3)

ГИД ВОДНОГО РАСПРЕДЕЛИТЕЛЯ

ПИТАЮЩАЯ ТРУБА (BED-5)

ПИТАЮЩАЯ ТРУБА (BED-4)

ПИТАЮЩАЯ ТРУБА (BED-3)

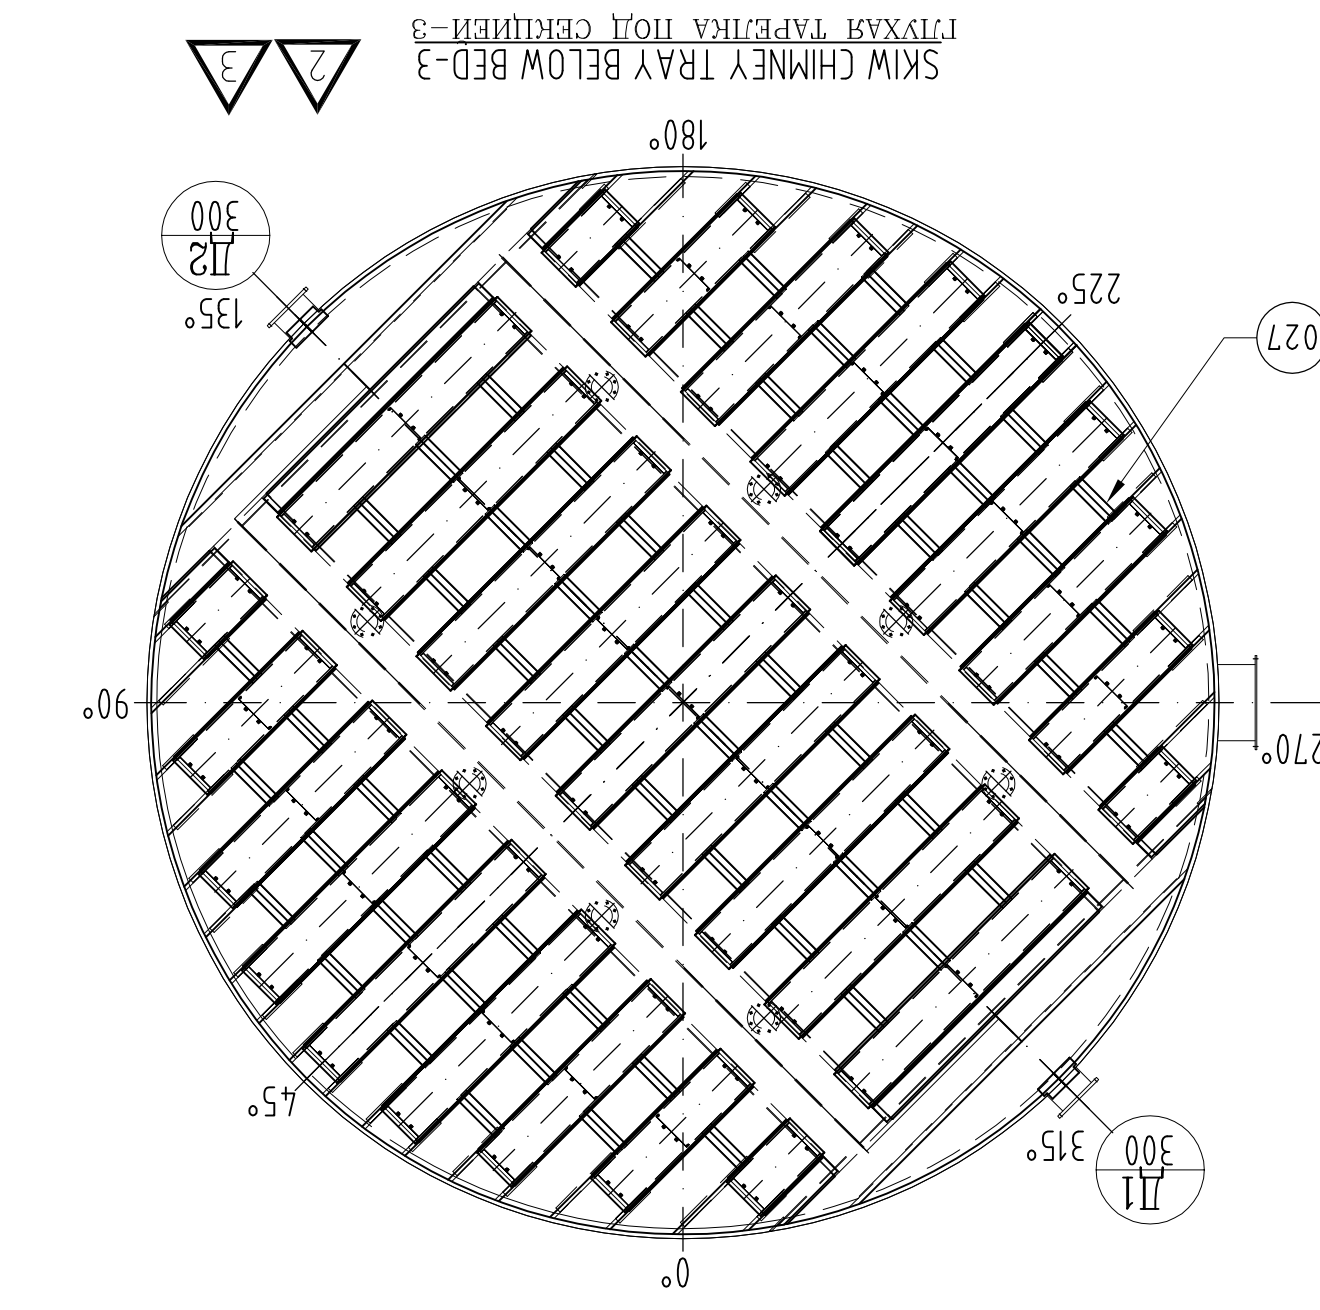
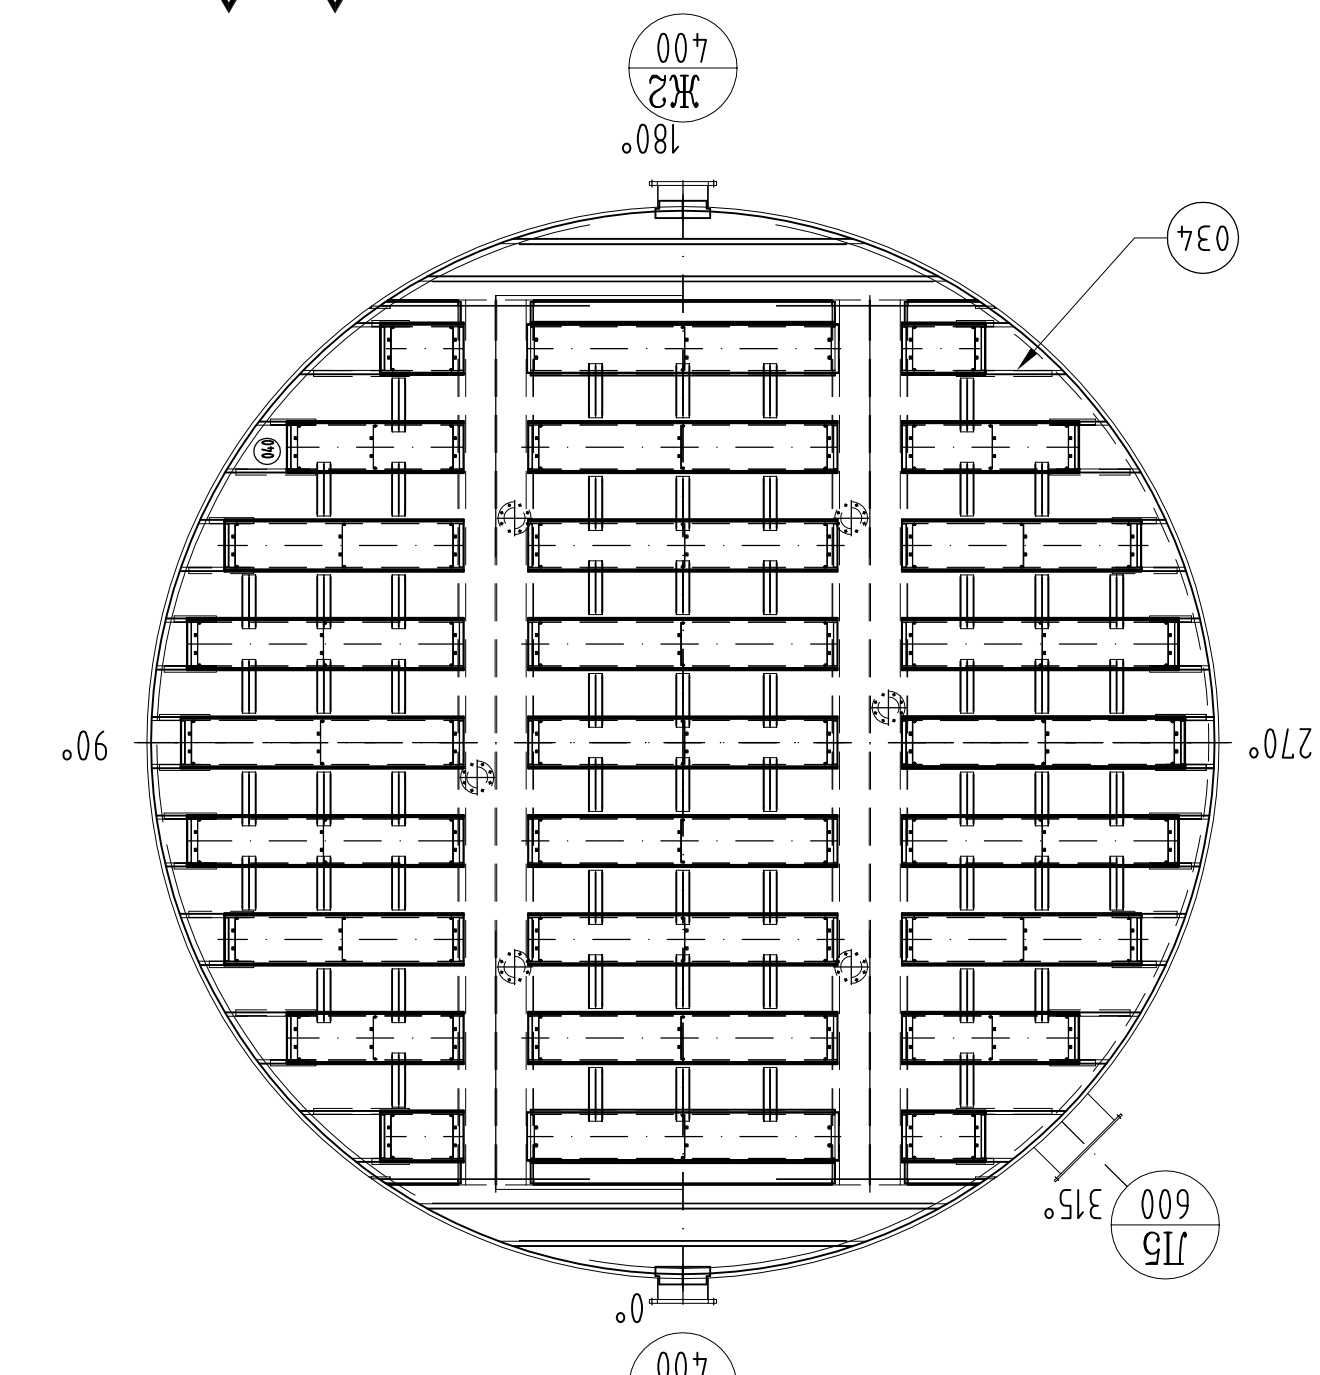
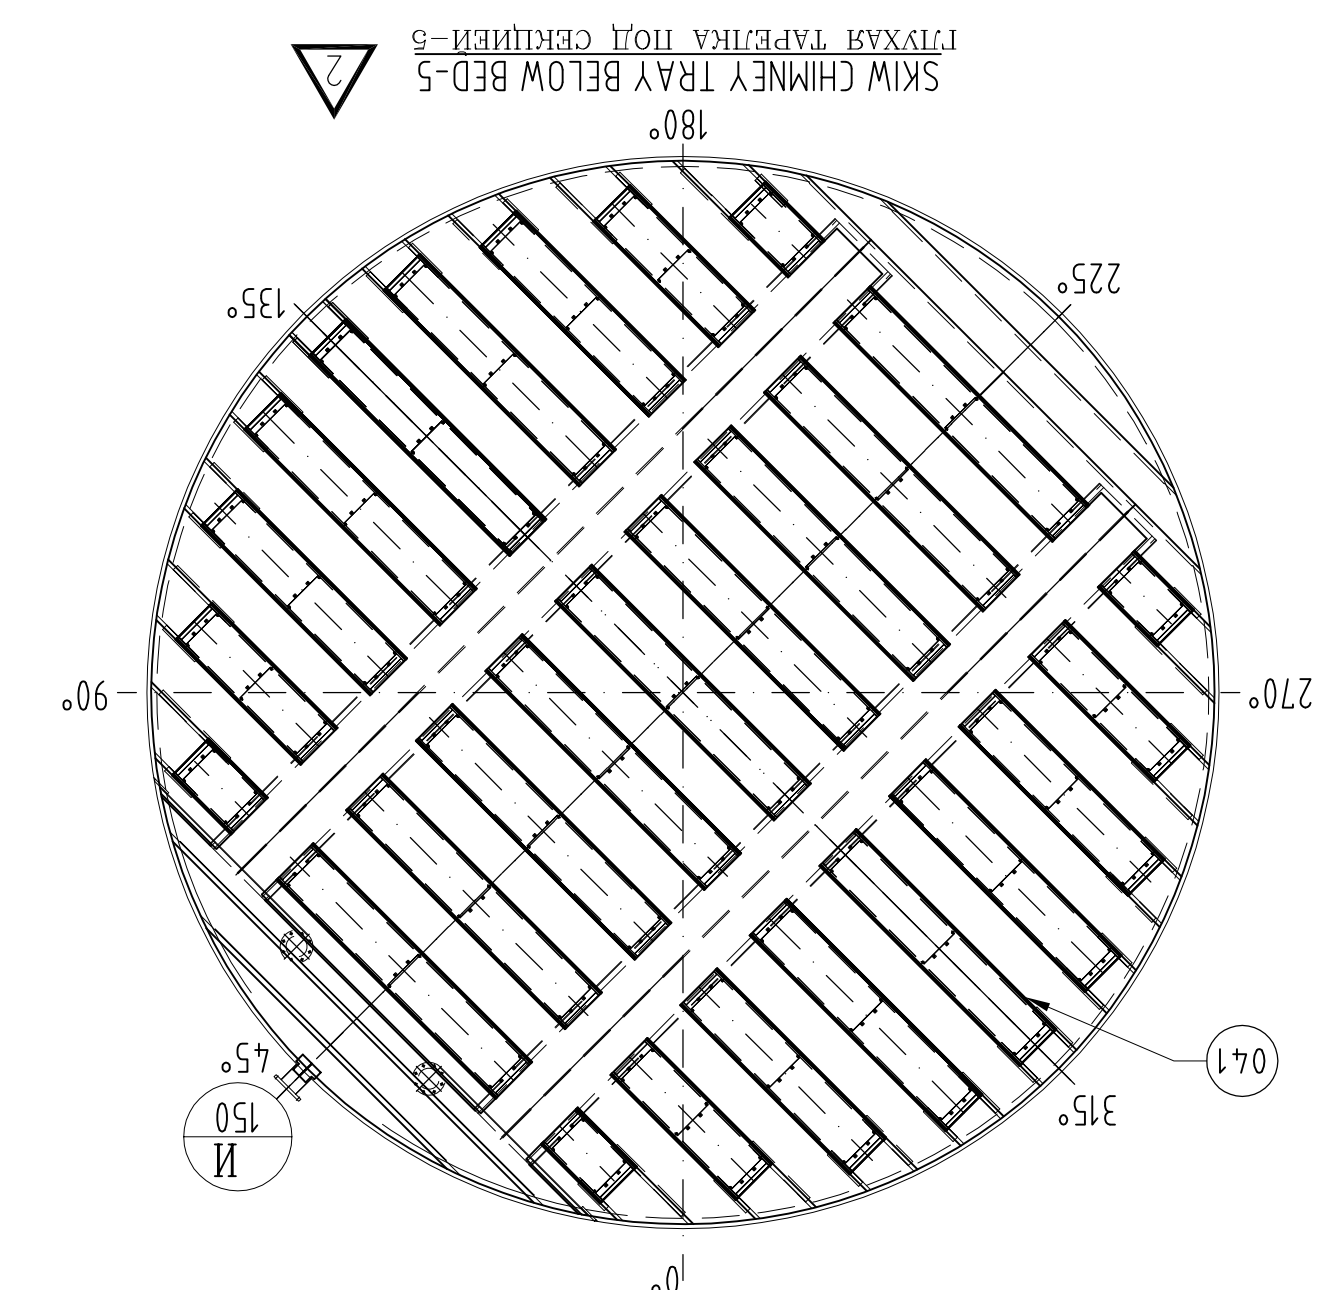
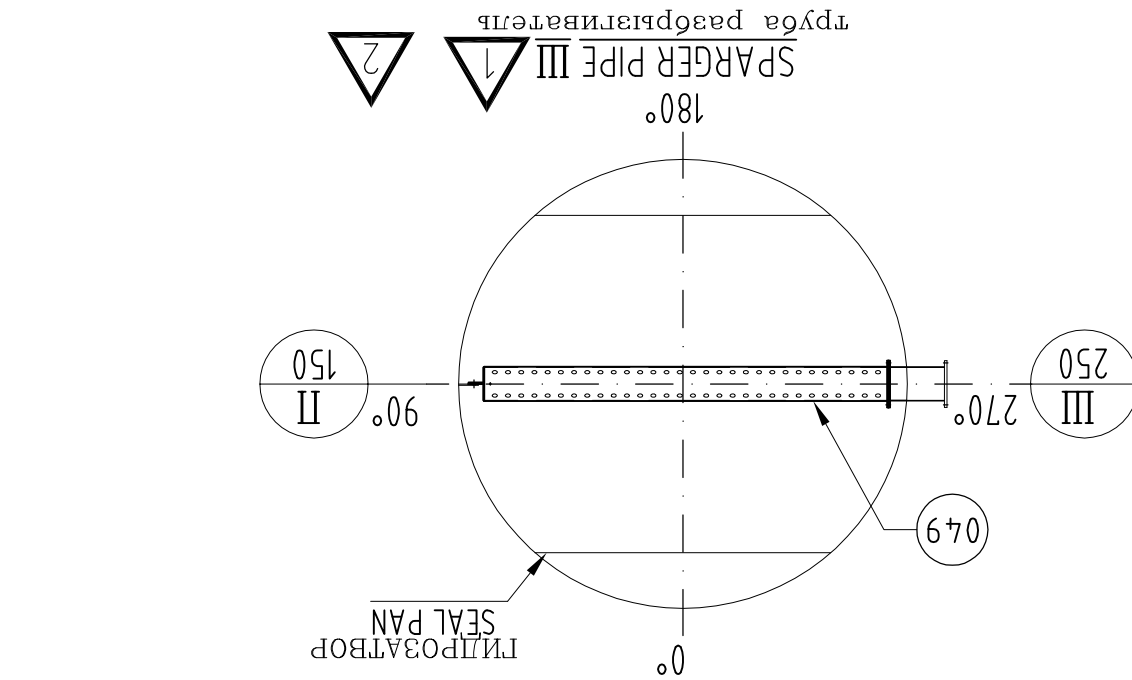


СПАРДЖЕР ПИП III

ЛИХАЯ ТРАПЛИКА ПОД СЕКЦИЕЙ-5

ЛИХАЯ ТРАПЛИКА ПОД СЕКЦИЕЙ-4

ЛИХАЯ ТРАПЛИКА ПОД СЕКЦИЕЙ-3

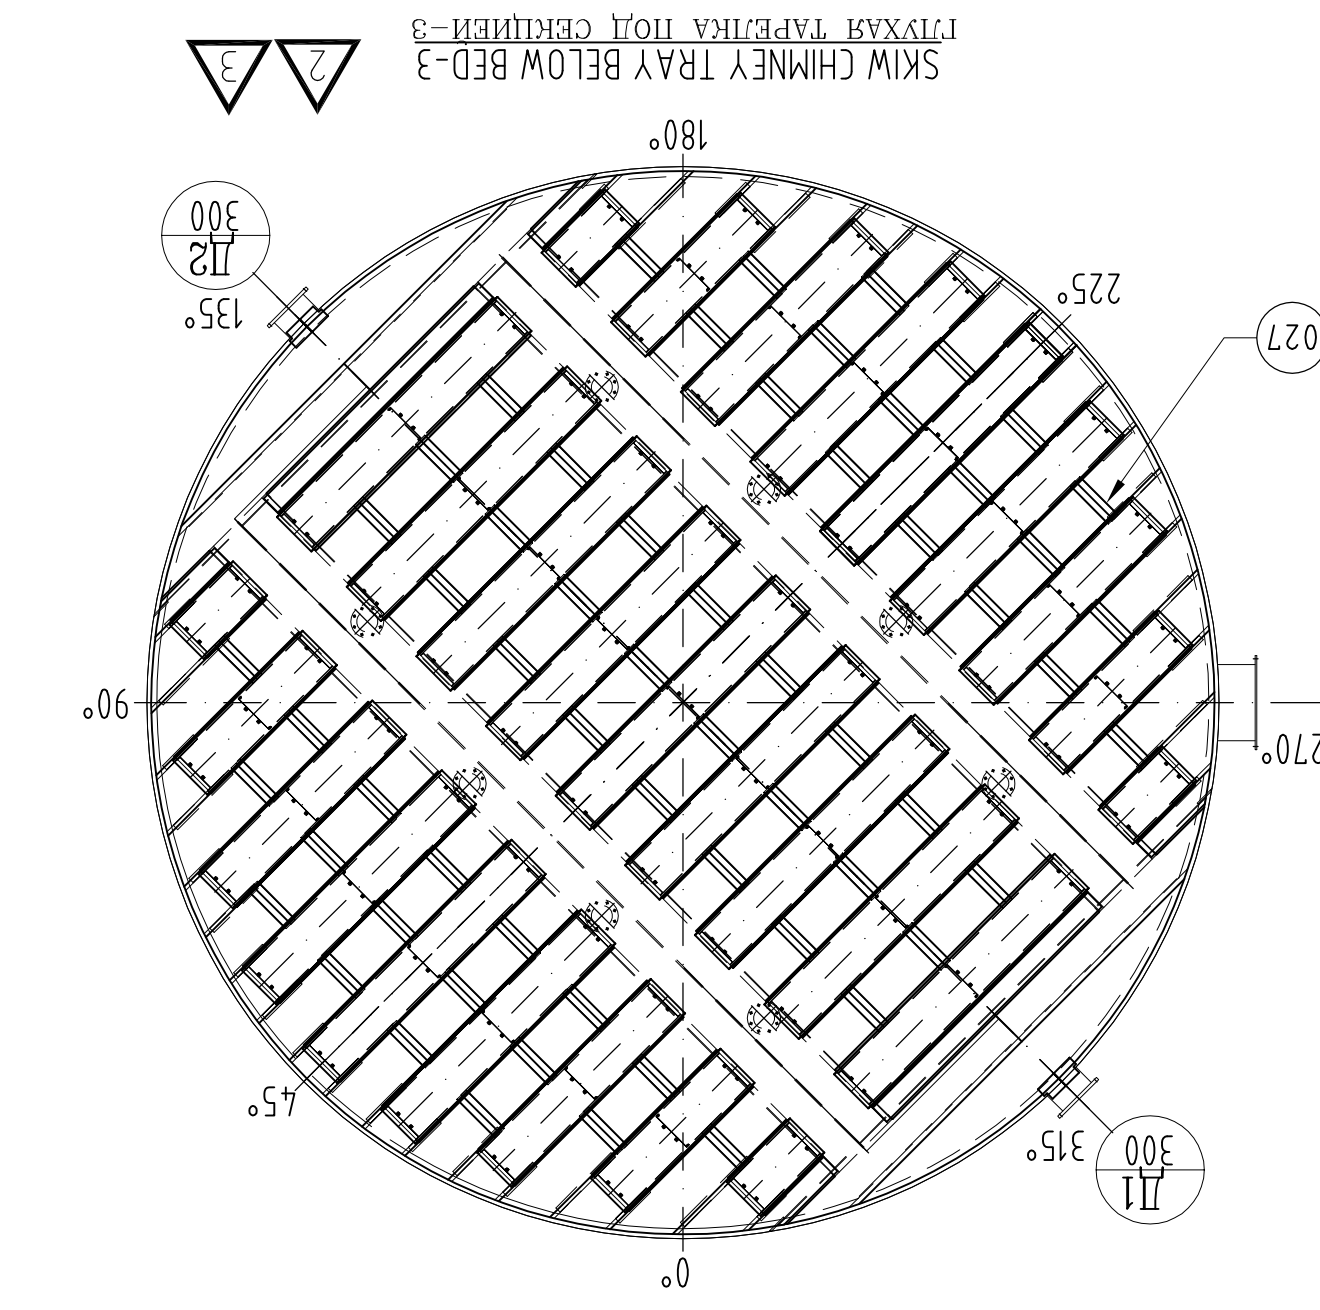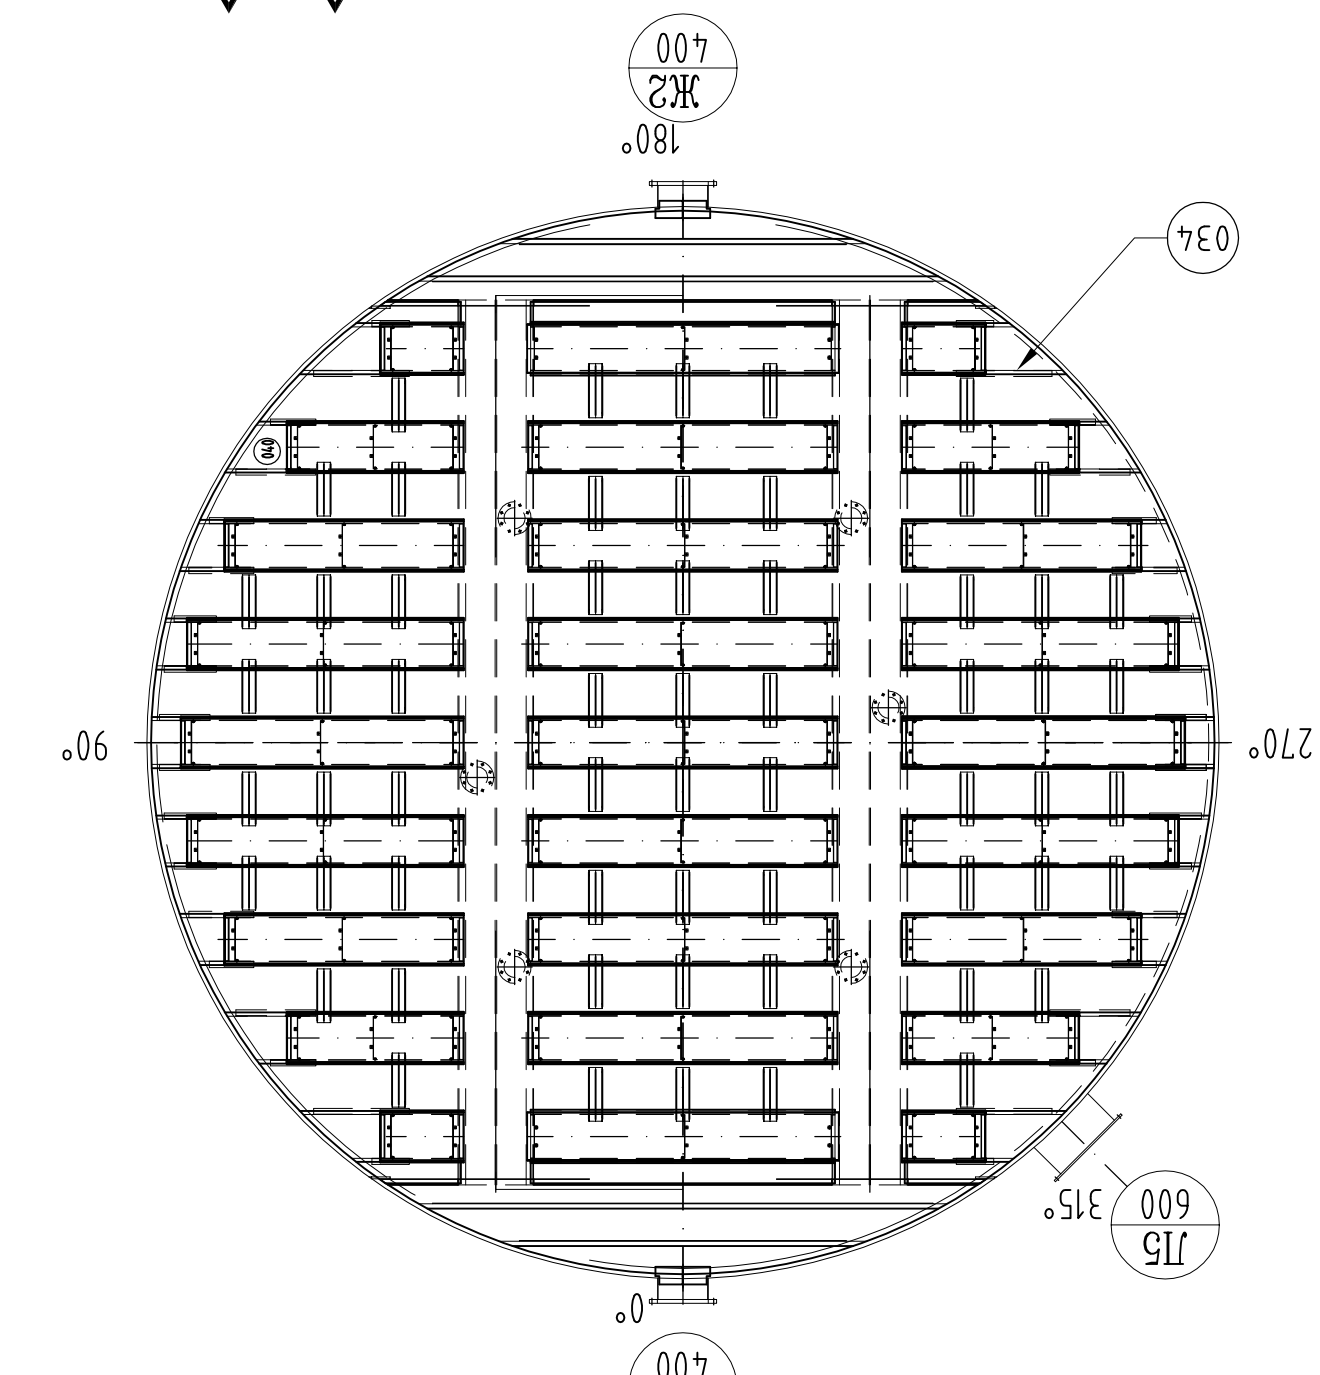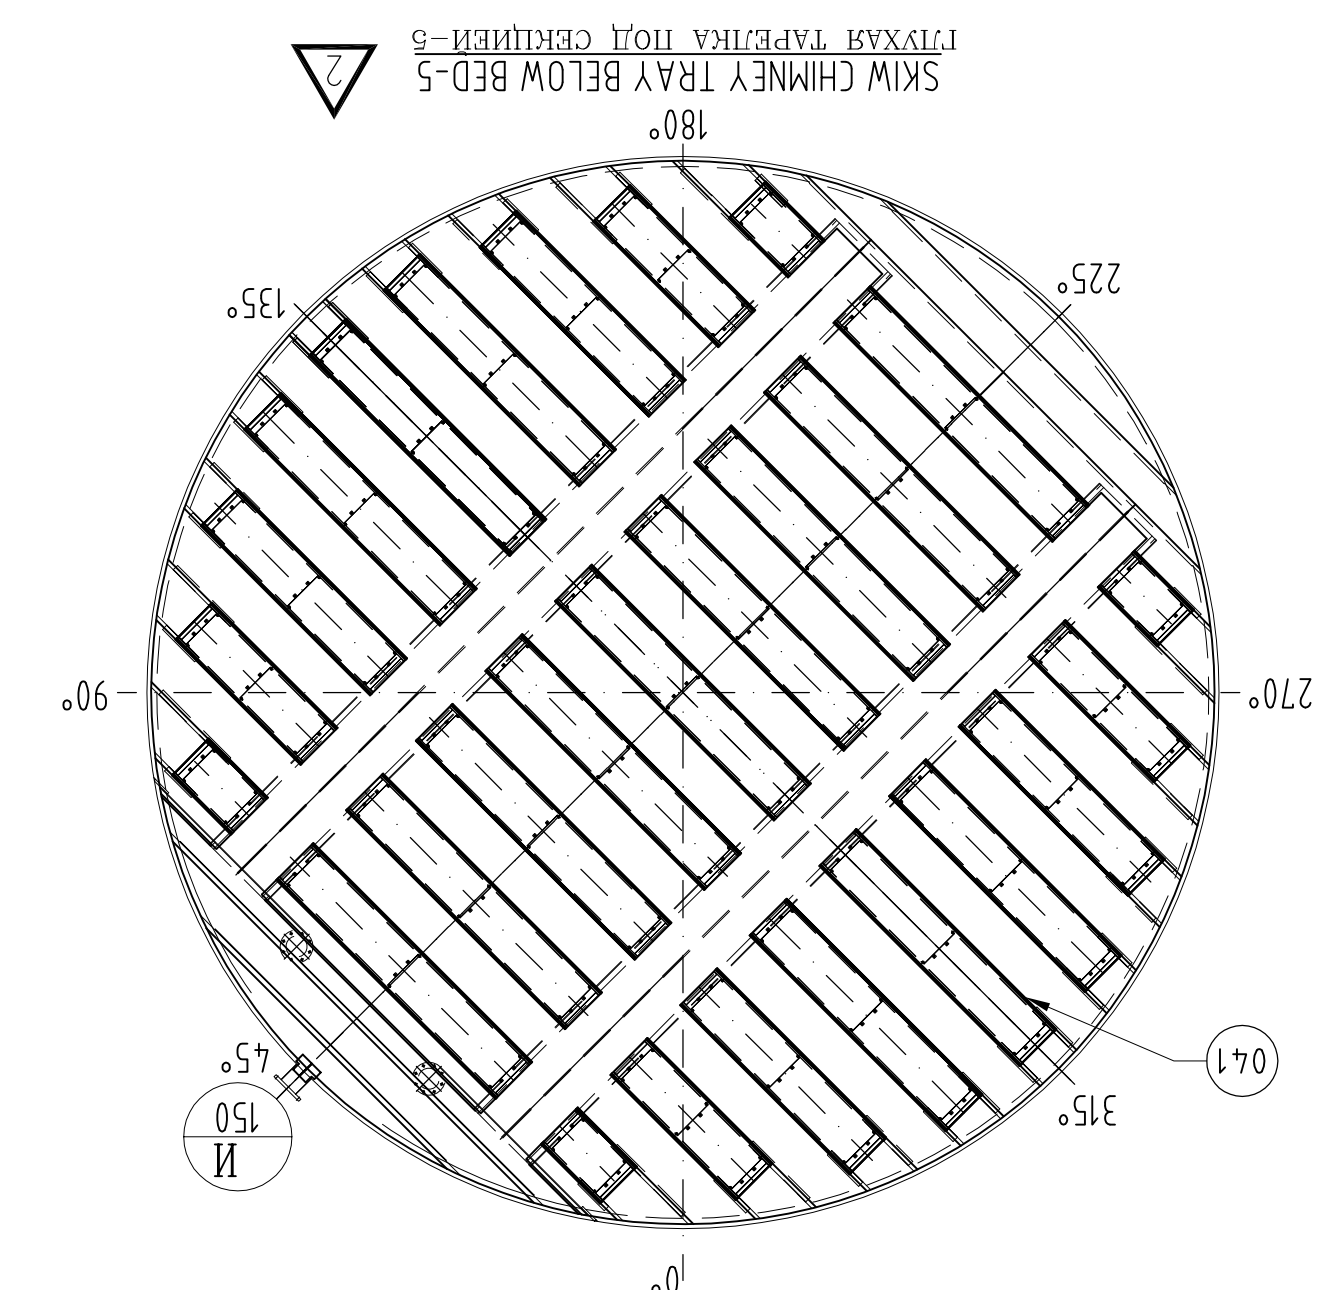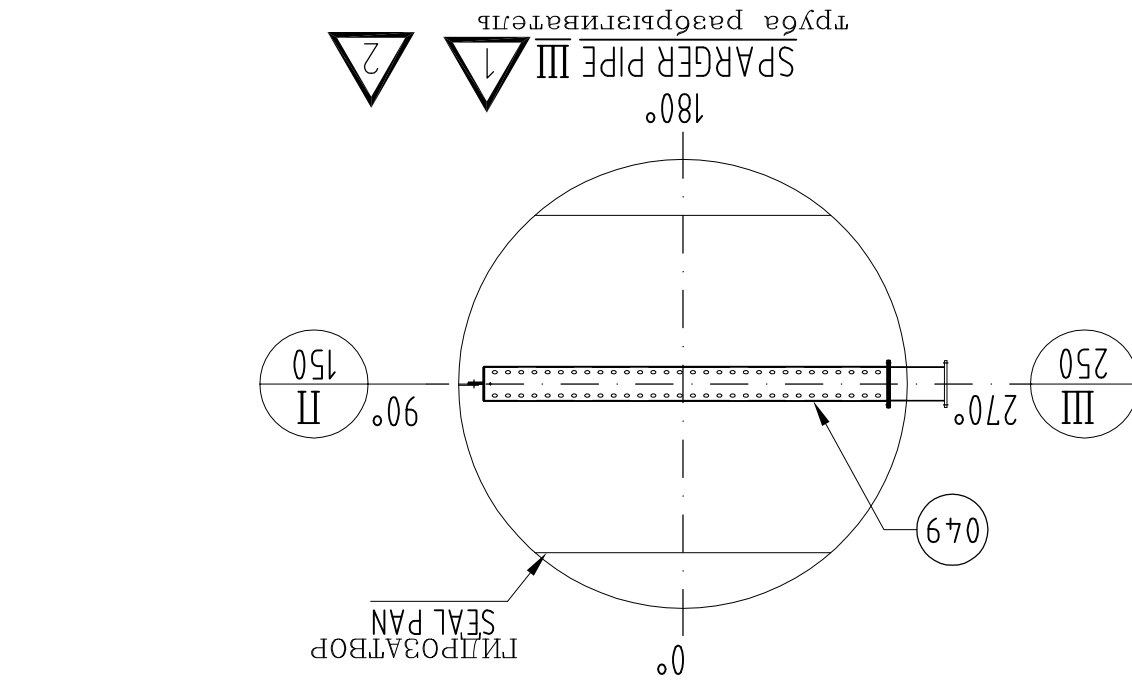

СПАРДЖЕР ПИП III

ЛИХАЯ ТРАПЛИКА ПОД СЕКЦИЕЙ-5

ЛИХАЯ ТРАПЛИКА ПОД СЕКЦИЕЙ-4

ЛИХАЯ ТРАПЛИКА ПОД СЕКЦИЕЙ-3