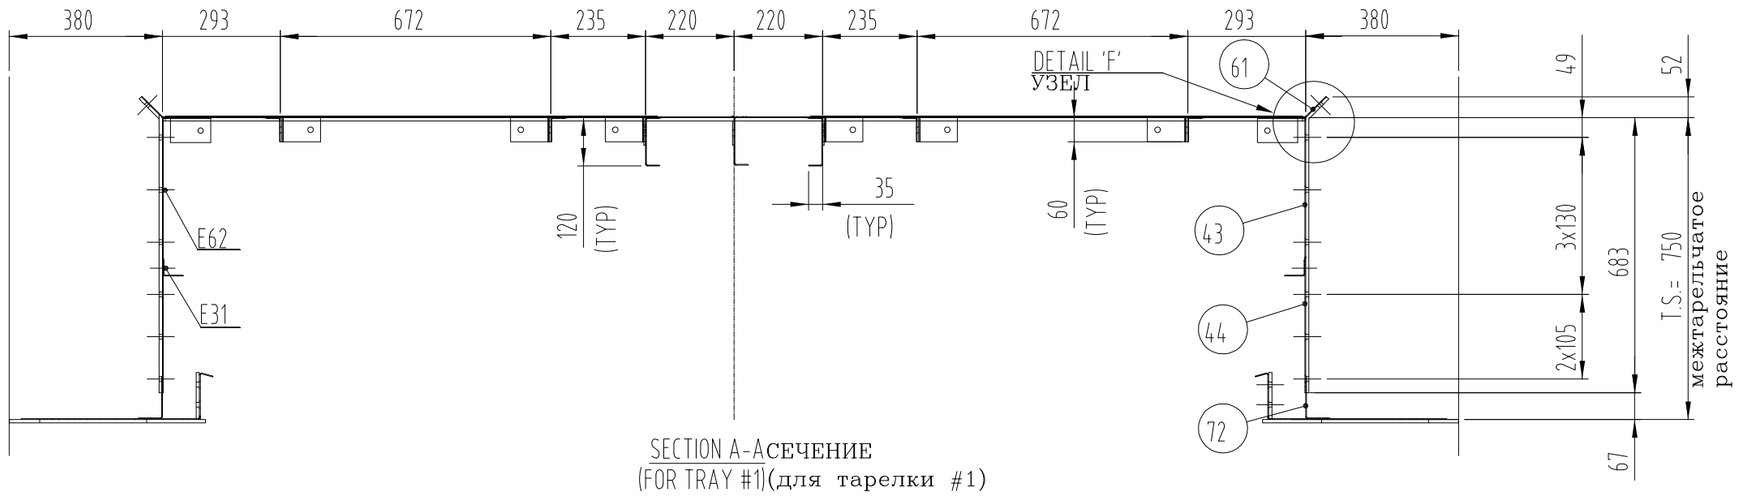

SECTION A-A СЕЧЕНИЕ
(FOR TRAY #1)(для тарелки #1)

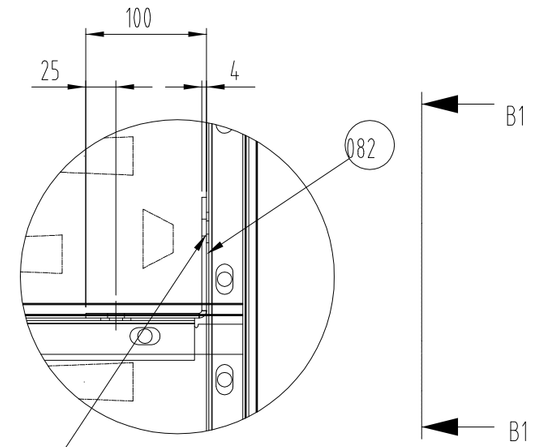

ø14 отверстие на сгибе пластины
ø 14 HOLE ON SHEAR PLATE.
25 X 14 SLOT ON TRAY PANEL.
25x14 слот на полотне

DETAIL 'B'
УЗЕЛ

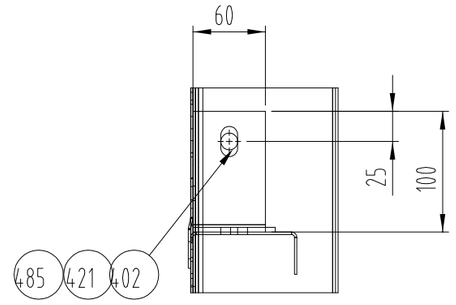

64 x REQ'D

SECTION B1-B1
СЕЧЕНИЕ

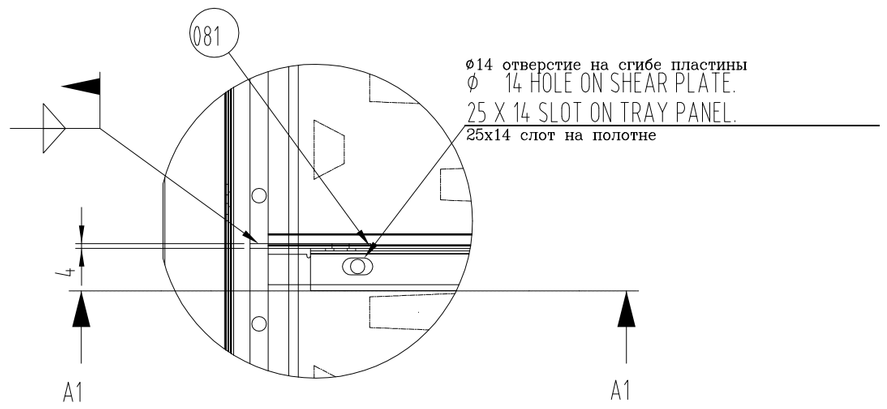

ø14 отверстие на сгибе пластины
ø 14 HOLE ON SHEAR PLATE.
25 X 14 SLOT ON TRAY PANEL.
25x14 слот на полотне

DETAIL 'A'
УЗЕЛ

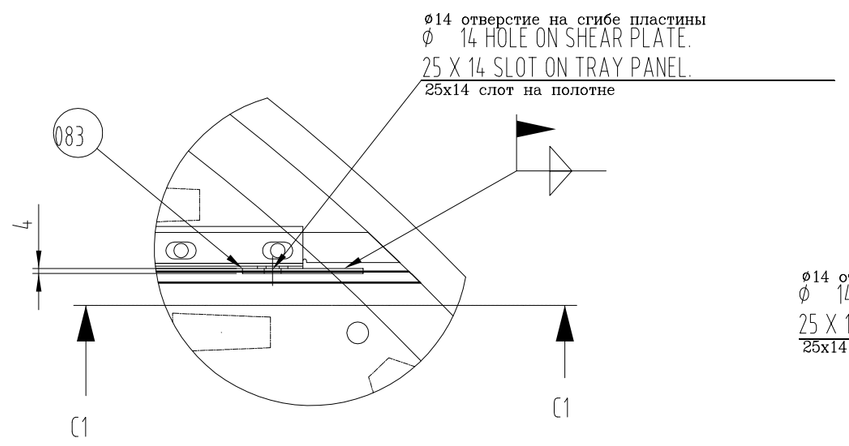

ø14 отверстие на сгибе пластины
ø 14 HOLE ON SHEAR PLATE.
25 X 14 SLOT ON TRAY PANEL.
25x14 слот на полотне

DETAIL 'C'
УЗЕЛ

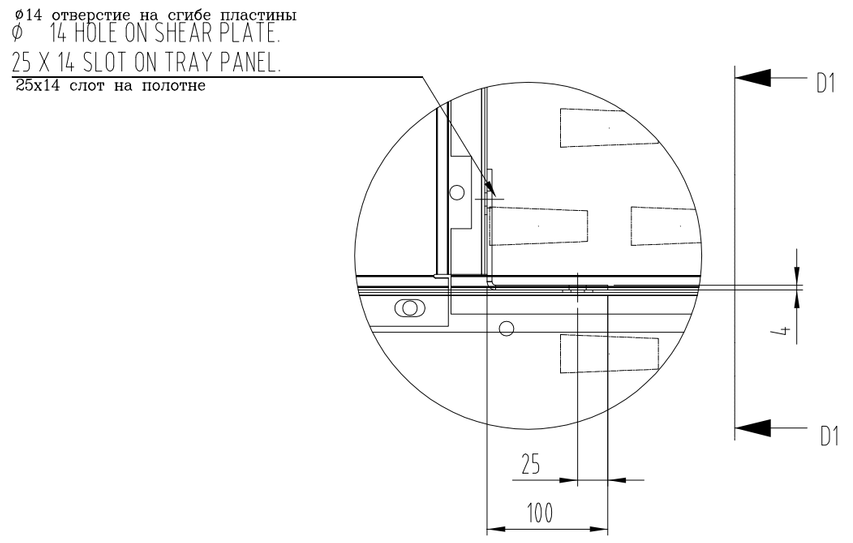

ø14 отверстие на сгибе пластины
ø 14 HOLE ON SHEAR PLATE.
25 X 14 SLOT ON TRAY PANEL.
25x14 слот на полотне

DETAIL 'D'
УЗЕЛ

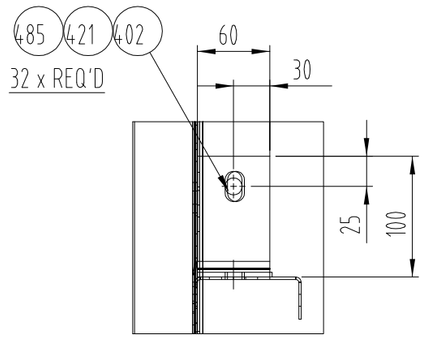

32 x REQ'D

SECTION D1-D1
СЕЧЕНИЕ

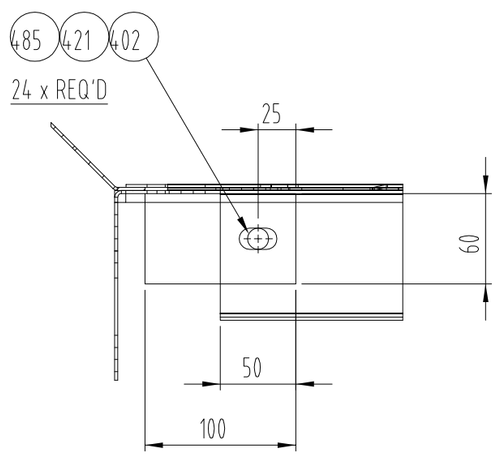

24 x REQ'D

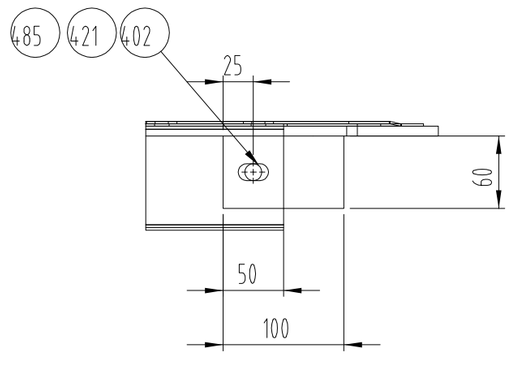

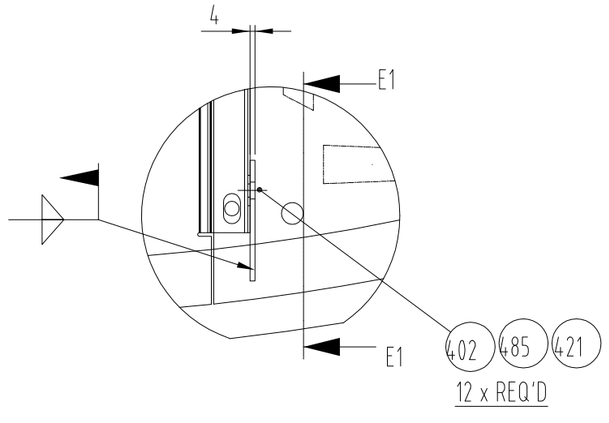

12 x REQ'D

DETAIL 'E'
УЗЕЛ

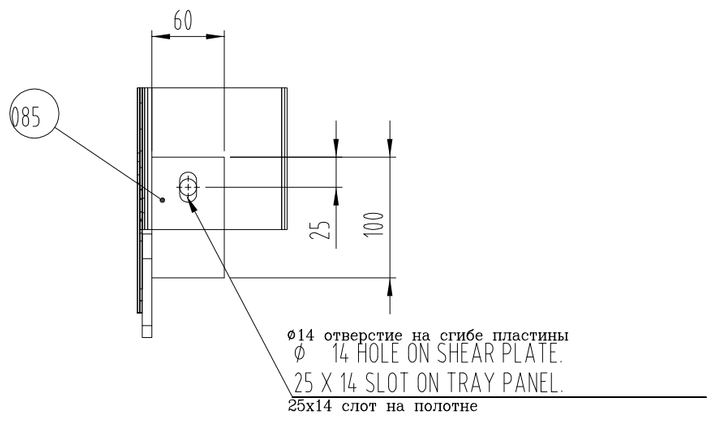

ø14 отверстие на сгибе пластины
ø 14 HOLE ON SHEAR PLATE.
25 X 14 SLOT ON TRAY PANEL.
25x14 слот на полотне

SECTION E1-E1
СЕЧЕНИЕ

	описание изменений	выполнил	дата	проверил	дата	утвердил	дата
01	Design revision.	RASALSH	02.06.2011	PURANIKMA	03.06.2011	HANDESH	03.06.2011
00	Original issue.	RASALSH	24.01.2011	GORECH	24.01.2011	PURANIKMA	25.01.2011
rev	revison remarks	issued by	date	checked	date	approved	date

SAP#300012113 | Project: 213933406 KACNEFT | Size: A2 | scale 1:15
Sec-ID: 3600 | Customer: SALAVATNEFTEORGSINTEZ | Cust.P.O.:2139334.06
Col-No./Tag: 001/K-300 VALSKIN/0.0mm | customer dwg.:
Bed: TRAYS 1-3 | AF | PLANT/AREA | END USER:

SULZER

2 Pass SVG odd trays 1 u/i 3
НЕЧЕТНЫЕ 2-ПОТОЧНЫЕ SVG ТАРЕЛКИ #1-3

drawing-no.: 2139334-001-089-2/3

Drawing-state: стадия
CERTIFIED FINAL

This document is entrusted to the recipient personally. The copyright remains with SULZER CHEMTECH. Recipients must obtain written authority of the said company before wholly or partly use or duplicating the contents or disclosing same to others. All rights reserved.

1000119175-DRW-AF